ВАКУУМНАЯ СТАНЦИЯ — РАСПОЛОЖЕНИЕ ОБОРУДОВАНИЯ И ТРАСС (по компоновке 08.07), М 1:30

ПЛАН (отметки +2.500 / +4.000 / +5.415 / трассы — проекция)

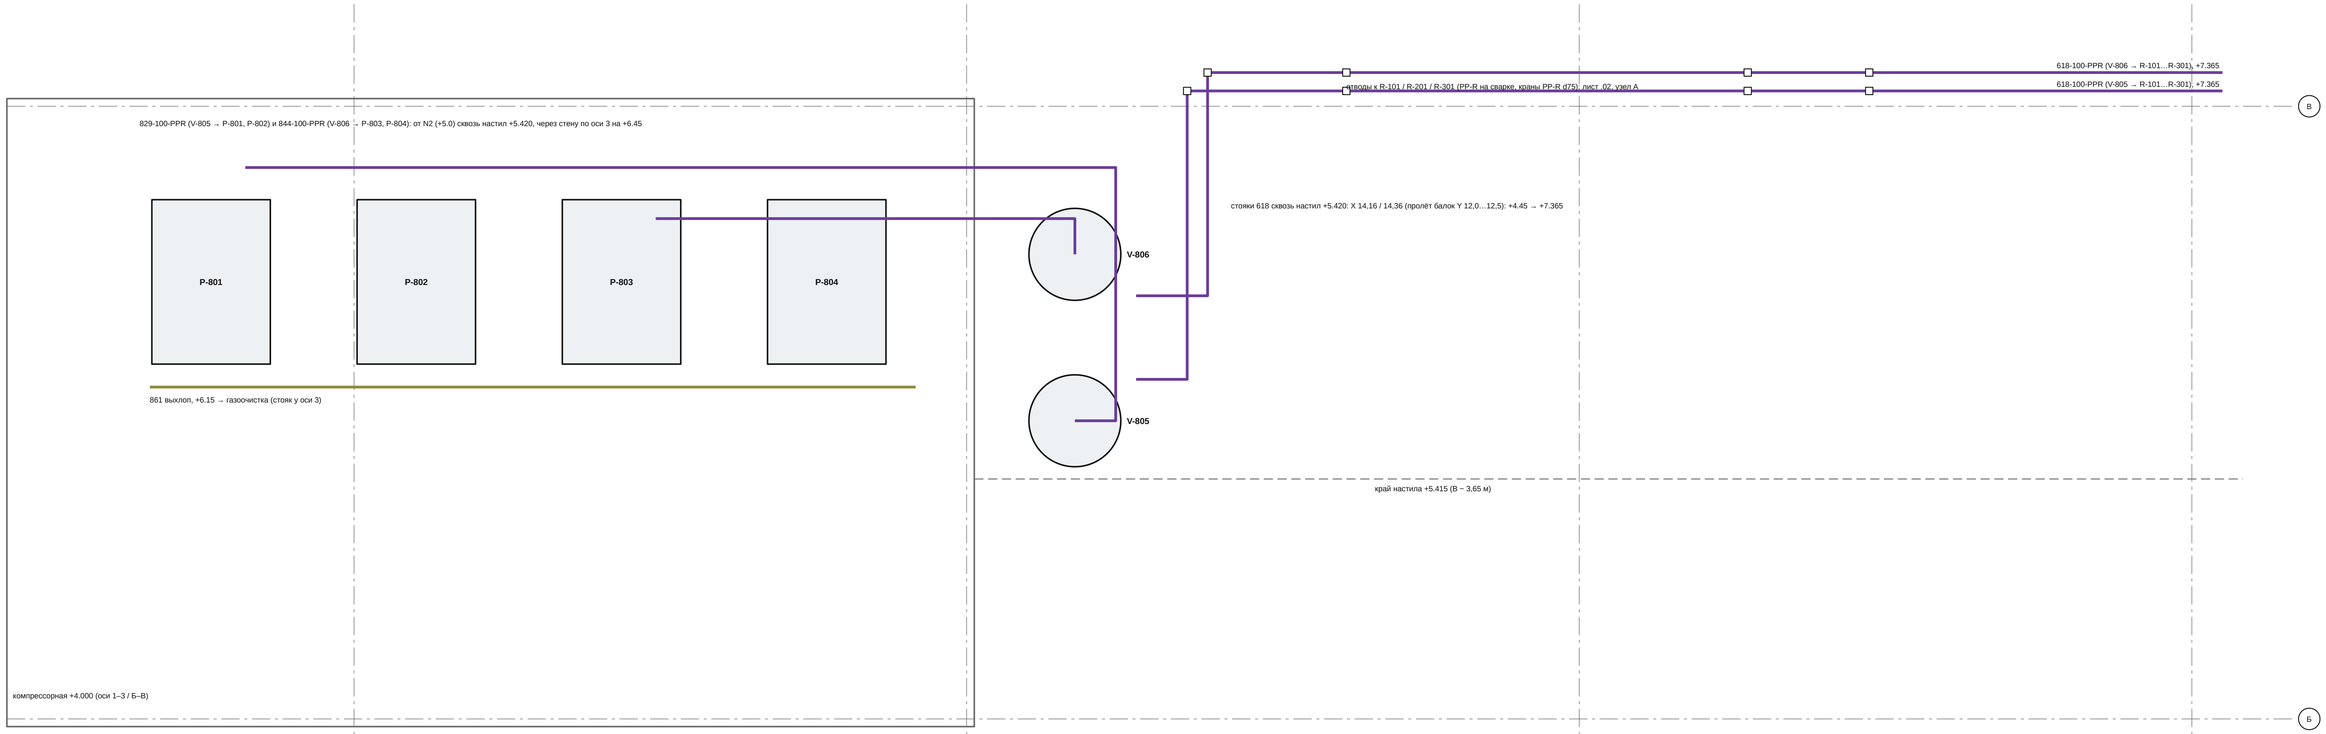

РАЗРЕЗ (вид с ряда Б, проекция Y 8,4…12,4), отметки

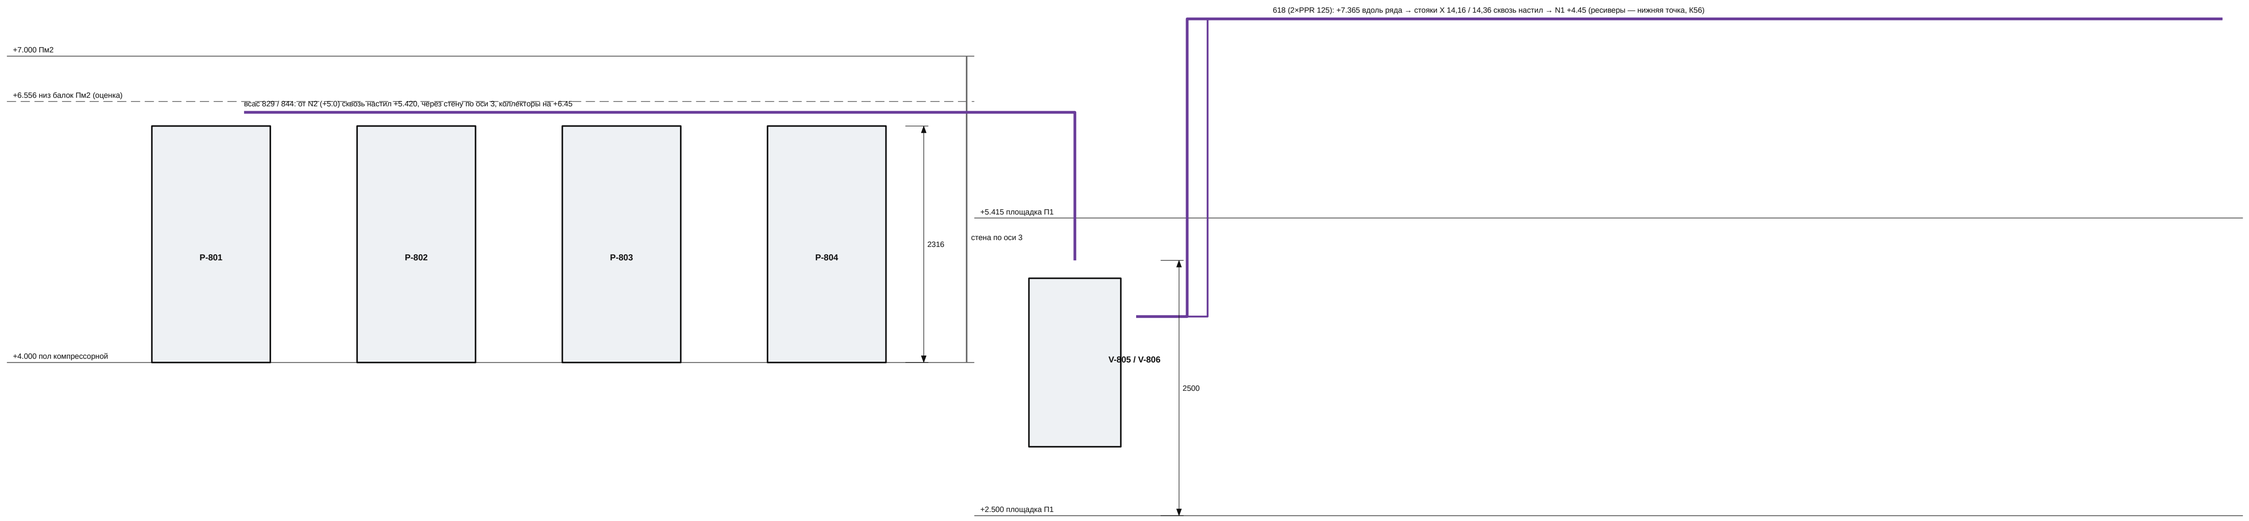

1. Координаты — по компоновке 08.07 (±0,1 м) и 3D-модели узла; X от оси 1, Y от ряда А, Z — отметка.
2. 04.11 (Мареев): ресиверы — этажом ниже, на П1 +2.500 у оси 3 (верх N2 +5.0 — ниже агрегатов): нижняя точка системы (K56); дренаж N5 — сквозь настил.
3. Всас 829/844 — стояки от N2 сквозь настил +5.420 (гильзы), через стену по оси 3 на +6.45; до низа балок Пм2 (+6.556, оценка) ≈ 0,04 м — замерить.

					37-02/26-ТХ.ОБ7.М.СБ	
Изм.	Лист	№ докум.	Подп.	Дата		
Разраб.					**Вакуумная станция: план и разрез** (сборка)	Лит. Р · Масса — · Масштаб 1:30
Пров.						
Т.контр.						
						Лист 1 · Листов 1
Н.контр.						
Утв.					Обвязка, узел 7: вакуумная станция	**Опытно-промышленный участок**