
УСТАНОВКА В СБОРЕ — МОНТАЖНАЯ СХЕМА (аппараты М 1:16, отметки — по 3D-модели). Номера соединений — как в ведомости соединений

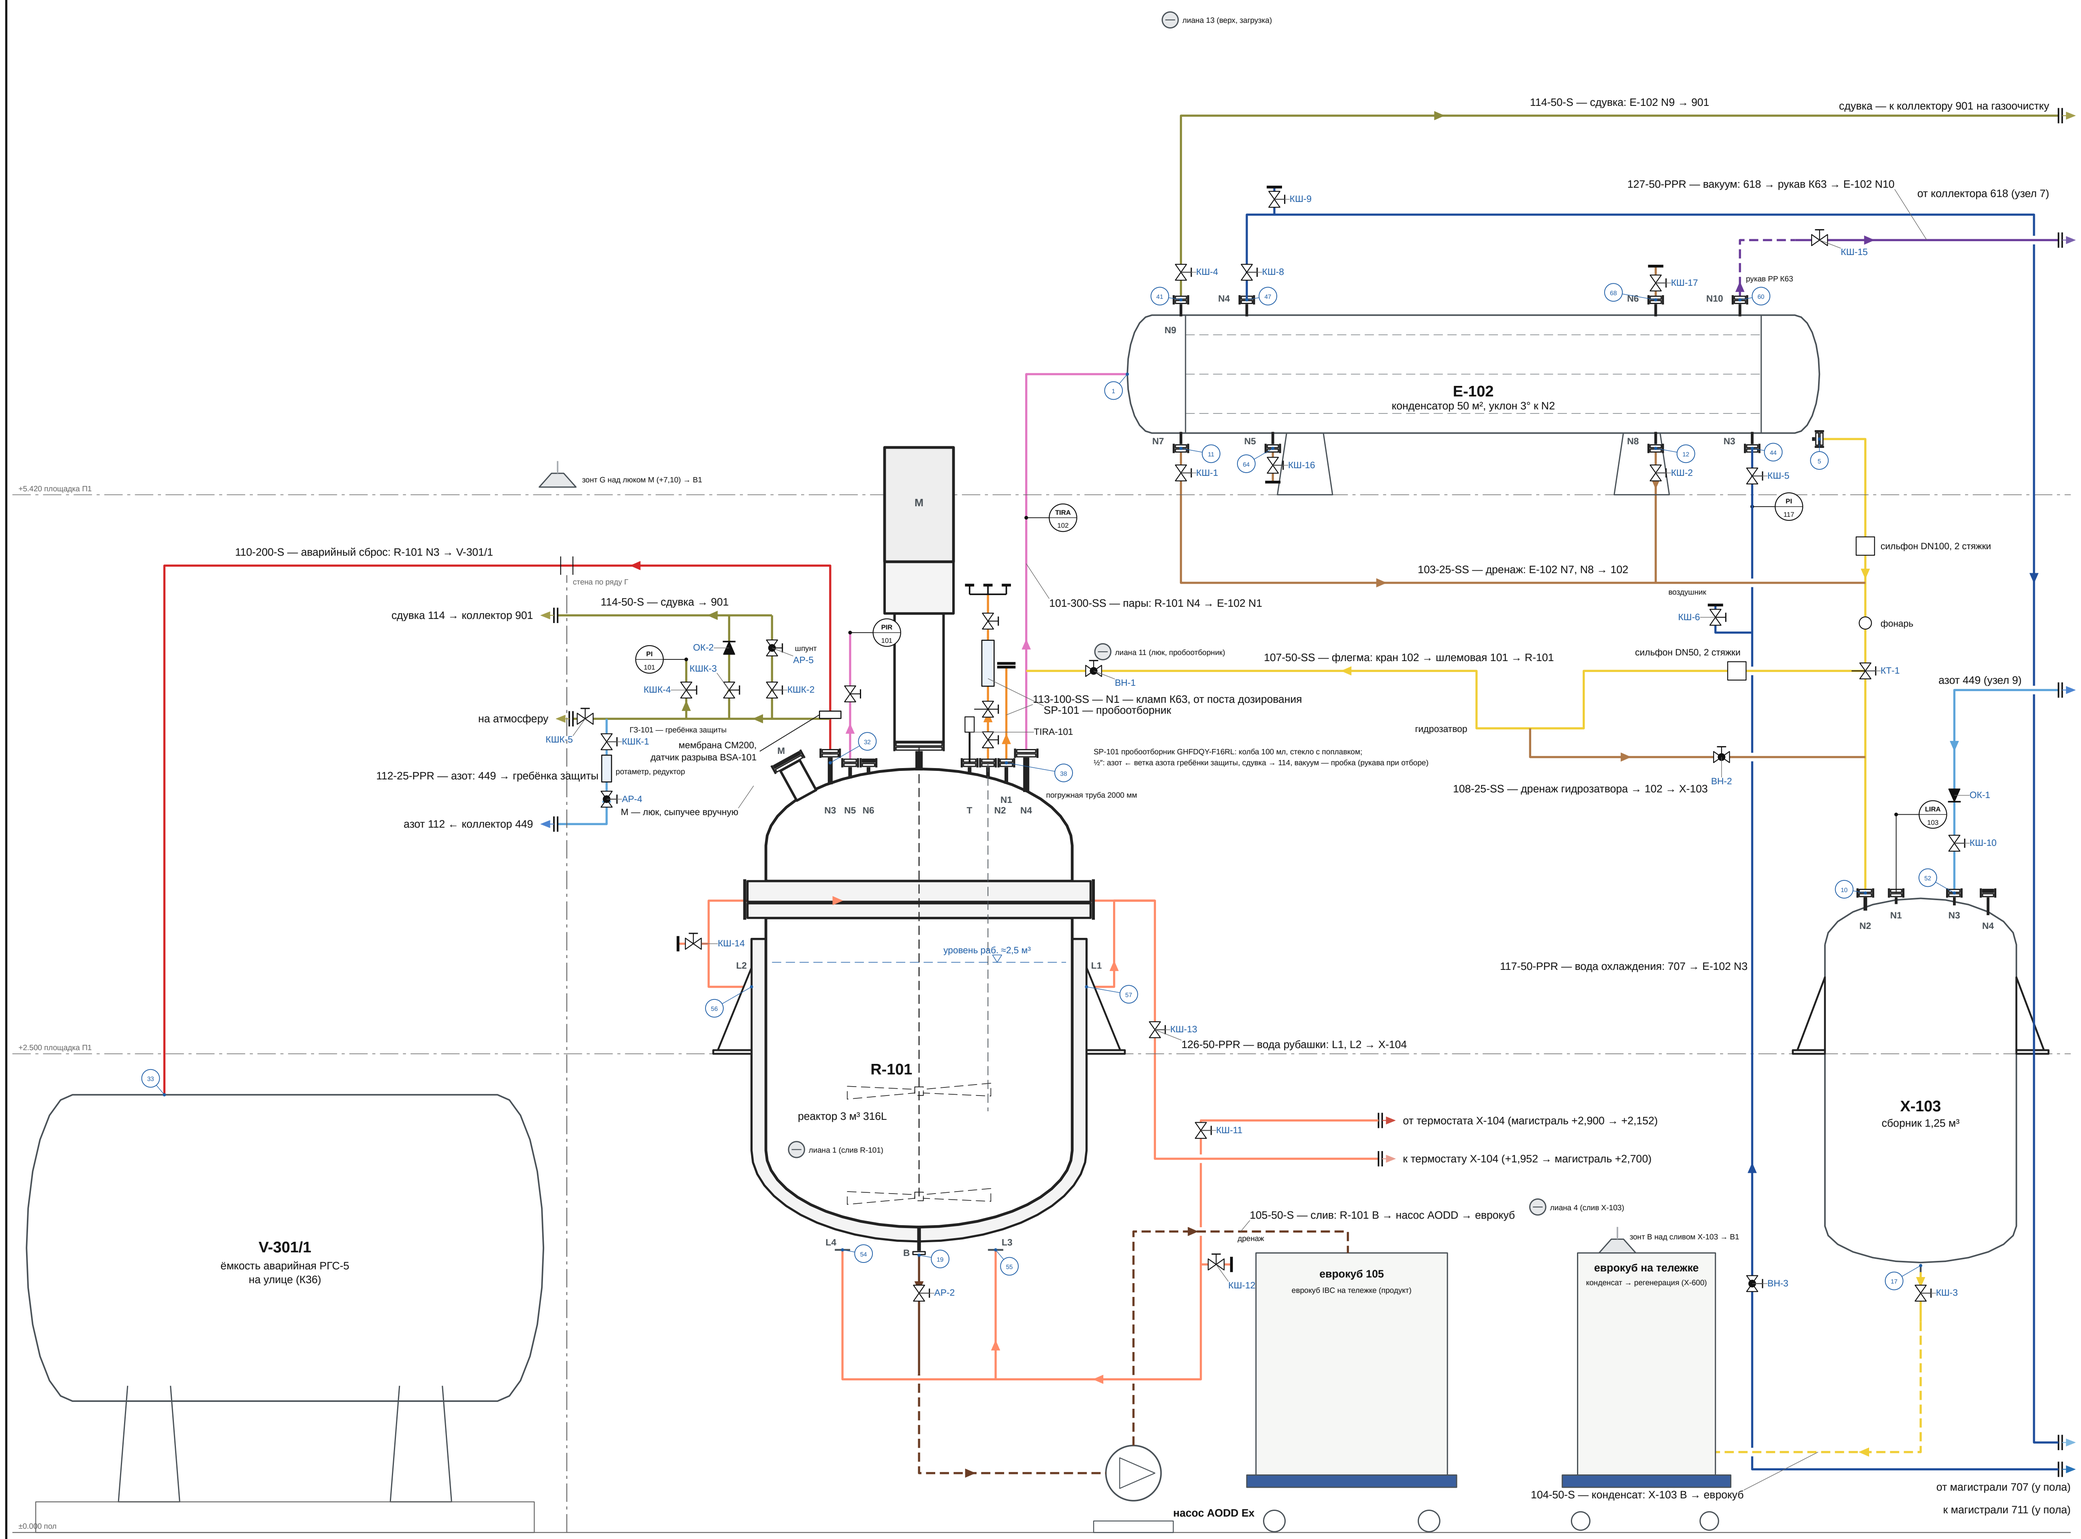

ПЕРЕЧЕНЬ ПОЗИЦИЙ

Поз.	Наименование	Кол.
R-101	Реактор 3 м³ 316L с рубашкой и мешалкой	1
E-102	Конденсатор паров 50 м²	1
X-103	Сборник конденсата 1,25 м³	1
V-301/1	Ёмкость аварийная РГС-5 (улица)	1
105, 104	Еврокубы IBC 1000 *л* на тележках (продукт, конденсат)	2
SP-101	Пробоотборник GHFDQY-F16RL (поставка)	1

Потоки (цвет линии)

- сырьё и загрузка
- пары (реактор → конденсатор)
- конденсат и флегма
- продукт, слив реактора
- дренажи
- аварийный сброс
- вакуум
- азот
- сдувки и дыхание
- вода охлаждающая (оборотная)
- теплоноситель — вода от термостата
- рукав (цвет — по потоку)
- зонт местного отсоса (вентиляция) → магистраль вытяжки B1
- лиана FM-200 — местный отсос на поворотной балке
- очертания аппаратов — проекция 3D-модели
- внутренние устройства (мешалки, вал, гильза, перегородки)
- (12) номер соединения (ведомость соединений)


Примечания


1. Аппараты — М 1:16, отметки — по 3D-модели; положение в плане — условно (трассы — листы 3–9).
2. Обвязка по трассам линий и чертежам поставщика; N1 — клапп K63 с заглушкой (подача от поста, K73).
3. Цвет линии — поток; DN и материал — в номере.
4. Номер в кружке — соединение (ведомость); теги арматуры — ведомость арматуры и КИП.
5. Граница узла — двойной штрих и стрелка; стрелка на линии — направление потока.
6. Свободные штуцеры — заглушки: R-101 N6, V-301/1 N2, N3; X-103 N4 — клапп K63 с заглушкой (задел, K73).

? уставки шпунт-аппарата и обратного клапана ГЗ-101 (ф)

Изм.	Лист	№ докум.	Подп.	Дата	**ОПУ.ОБ.R-101.M.01**		
Разраб.					**Реактор 3 м³ 316L (R-101):** установка в сборе	Лит.	Масса	Масштаб
Пров.						П	—	б/м
Т.контр.						Лист 1		Листов 16
Н.контр.								
Утв.					Опытно-промышленный участок	**Опытно-промышленный участок**		

РЕАКТОР 3 М³ 316L (R-101) — ВИД С ЗАПАДА (с внутренними устройствами) И КРЫШКА СВЕРХУ М 1:25

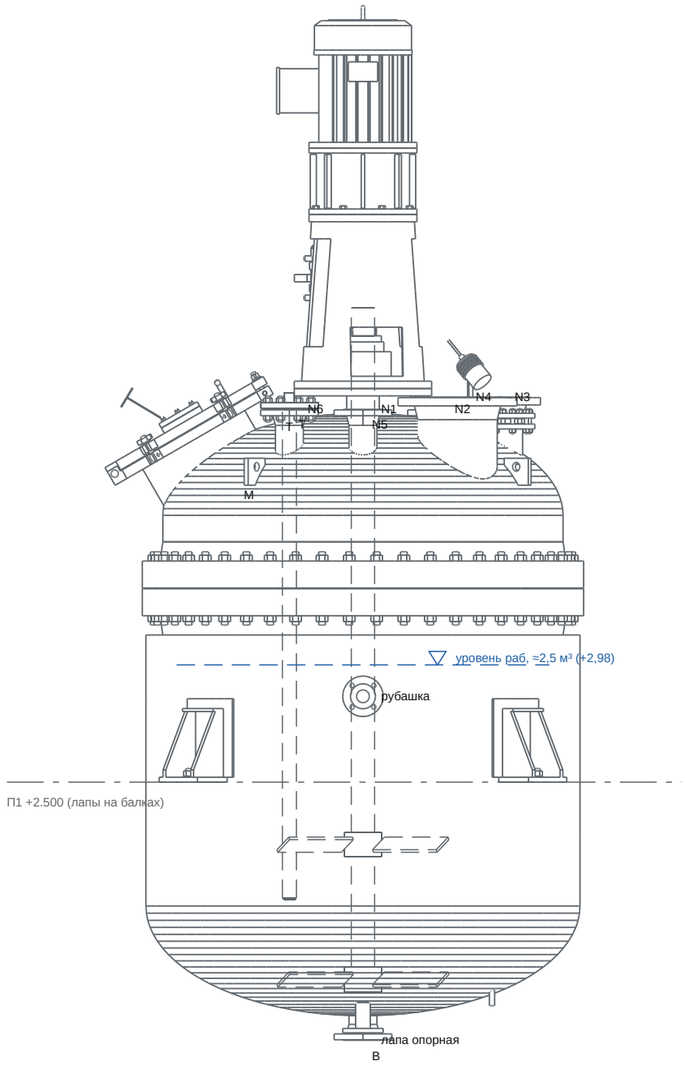

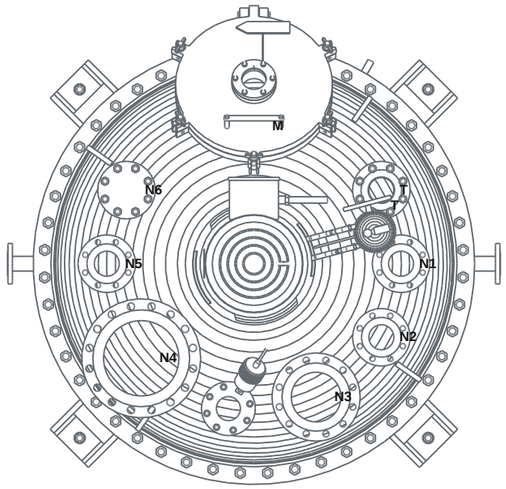

КРЫШКА СВЕРХУ (север — вверх); штуцеры — по л.11

ТАБЛИЦА ШТУЦЕРОВ R-101


Штуцер	Исполнение	Угол	Назначение (что присоединено)	Отм., м
B			штуцер слива PN25 DN100 (под донный клапан F41)	+1,448
G			штуцер вала Ø133×6 с опорным фланцем привода Ø560	
N1	WN100-25	90°	загрузочный: переходник фланец-кламп K63 с заглушкой (K73)	+4,020
N2	WN100-25	120°	пробоотборник ручной вакуумный	+4,020
N3	WN200-25	155°	разрывная мембрана CM200 → 110-200-S; ниже мембраны — гребёнка защиты…	+4,070
N4	WN300-25	230°	пары на E-102 (101-300-SS)	+4,070
N5	WN100-25	270°	датчик давления PIR-101	+4,020
N6	WN100-25	300°	свободный — заглушка	+4,020
T	WN100-25	60°	гильза термометра TIRA-101	+4,020

Рабочий уровень ≈2,5 м³ (80 % номинальных 3,14 м³ — принято, ?) — отметка +2,98 (днище 2:1 + цилиндр Ø1600, л.11). Отметки — по 3D-модели.

Изм.	Лист	№ докум.	Подп.	Дата	ОПУ.ОБ.R-101.М.02		
Разраб.					Реактор 3 м³ 316L (R-101): лист аппарата	Лит.	Масса	Масштаб
Пров.						П	—	1:25
Т.контр.						Лист 2		Листов 16
Н.контр.					Опытно-промышленный участок	Опытно-промышленный участок		
Утв.								

Пары и конденсат по схеме поставщика: шлемовая 101, спуск 102, дренажи 103, байпас флегмы 107, дренаж 108

Аппараты целиком, М 1:16; отметки — по 3D-модели; номера соединений — как в ведомости соединений

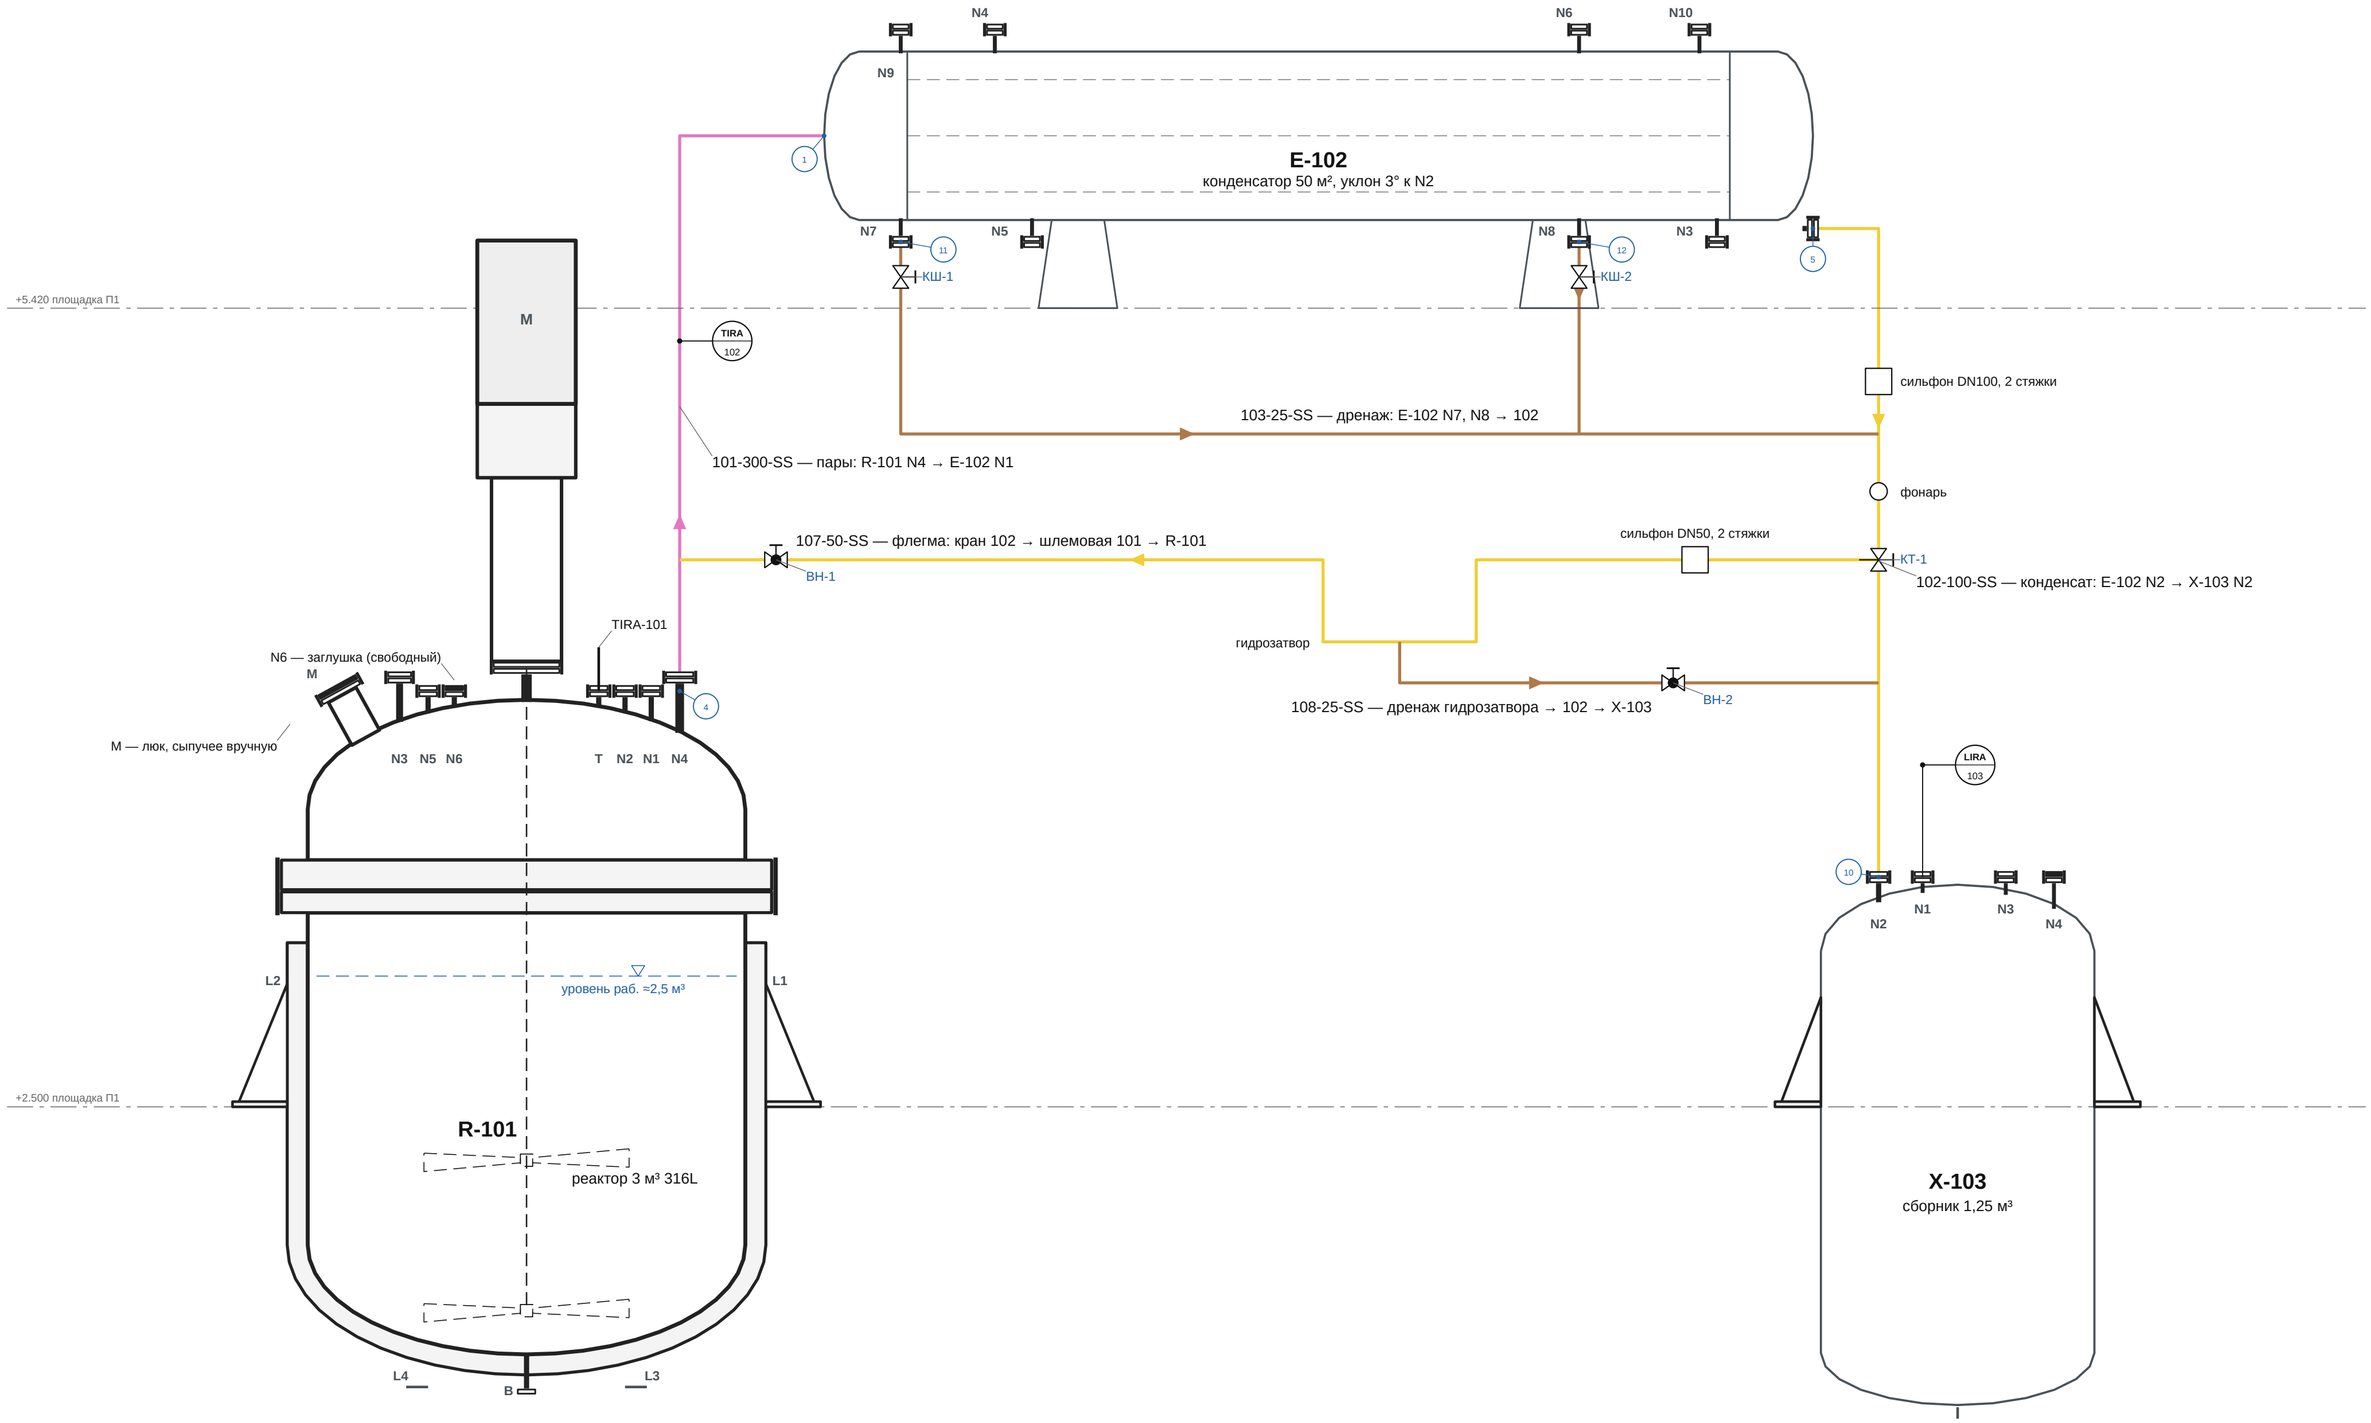

Изм.	Лист	№ докум.	Подп.	Дата
Разраб.				
Пров.				
Т.контр.				
Н.контр.				
Утв.				

ОПУ.ОБ.R-101.М.03

Реактор 3 м³ 316L (R-101): пары и конденсат (схема поставщика)

Лит.	Масса	Масштаб
П	—	б/м


Лист 3 — Листов 16

Опытно-промышленный участок

Опытно-промышленный участок

Крышка реактора (R-101): N1 — переходник фланец-кламп К63 с заглушкой (подача от поста дозирования, К73); N2 — пробоотборник; N5 — PIR-101; N6 — заглушка; M — люк

Аппараты целиком, М 1:13; отметки — по 3D-модели; номера соединений — как в ведомости соединений

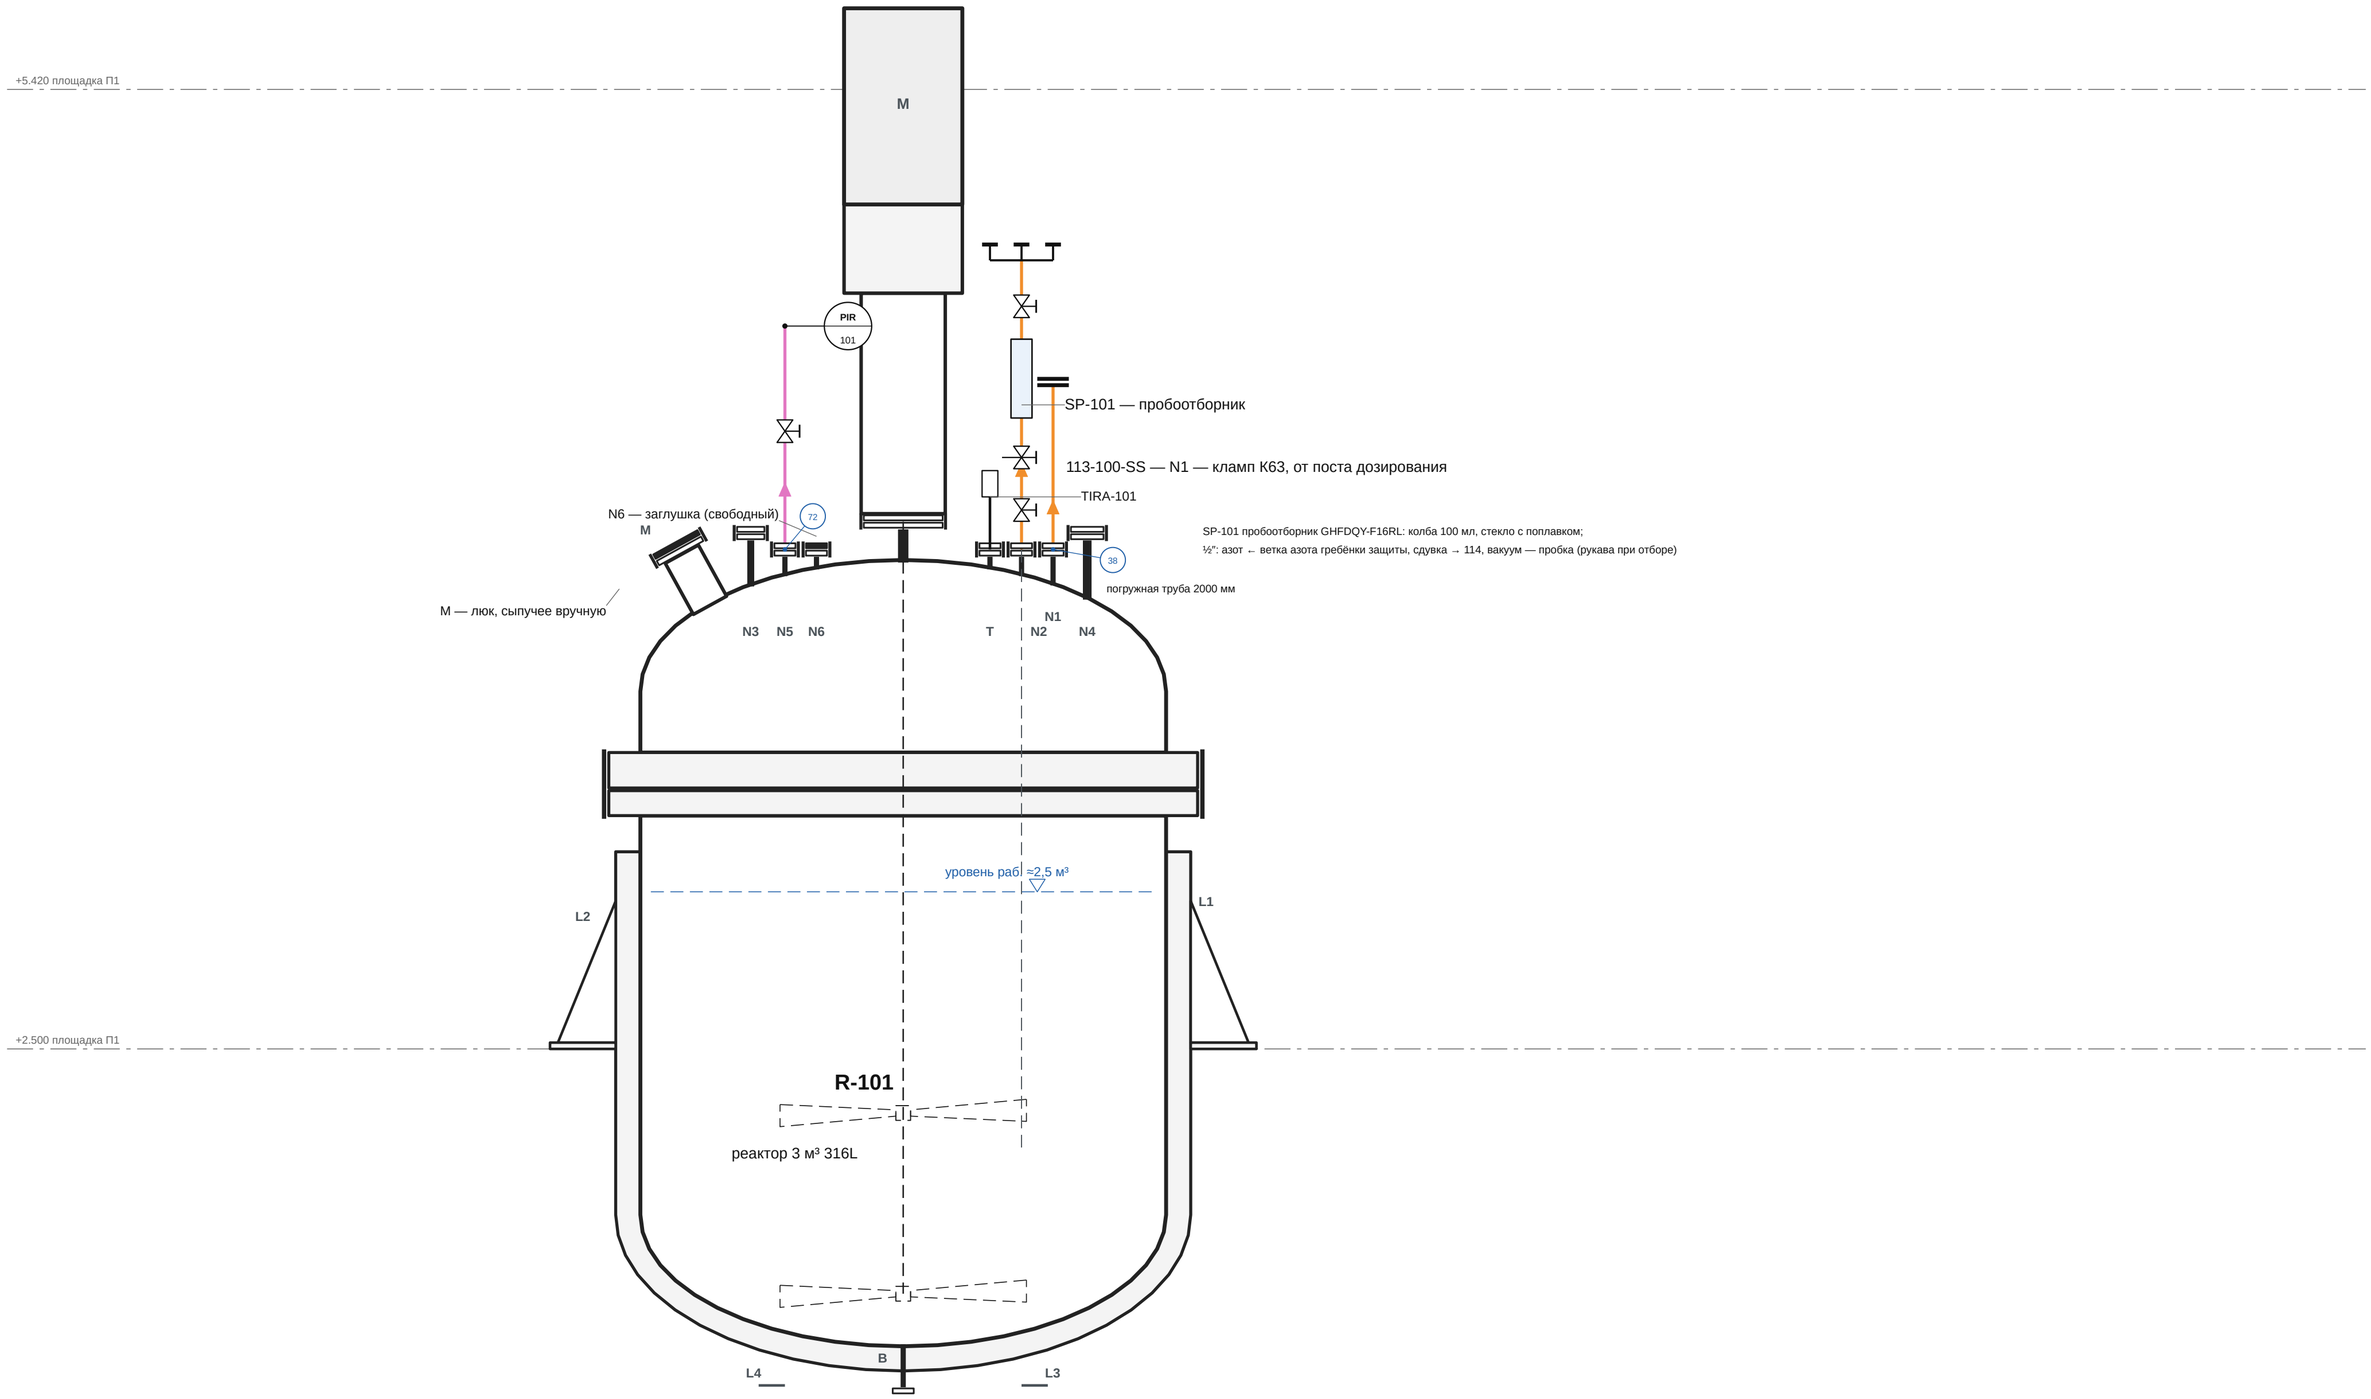

SP-101 пробоотборник GHFDQY-F16RL: колба 100 мл, стекло с поплавком;
½": азот ← ветка азота гребёнки защиты, сдувка → 114, вакуум — пробка (рукава при отборе)

Изм.	Лист	№ докум.	Подп.	Дата
Разраб.				
Пров.				
Т.контр.				
Н.контр.				
Утв.				

ОПУ.ОБ.R-101.M.04

Реактор 3 м³ 316L (R-101): крышка
реактора

Лит.	Масса	Масштаб
П	—	б/м


Лист 4 | Листов 16

Опытно-промышленный участок

Опытно-промышленный участок

Вакуум (K73): коллектор 618 (кран на отводе) → рукав PP K63 → переходник Ду25/K63 на E-102 N10; на N1 — кламп K63 с заглушкой (подача от поста дозирования)


Аппараты целиком, М 1:17; отметки — по 3D-модели; номера соединений — как в ведомости соединений

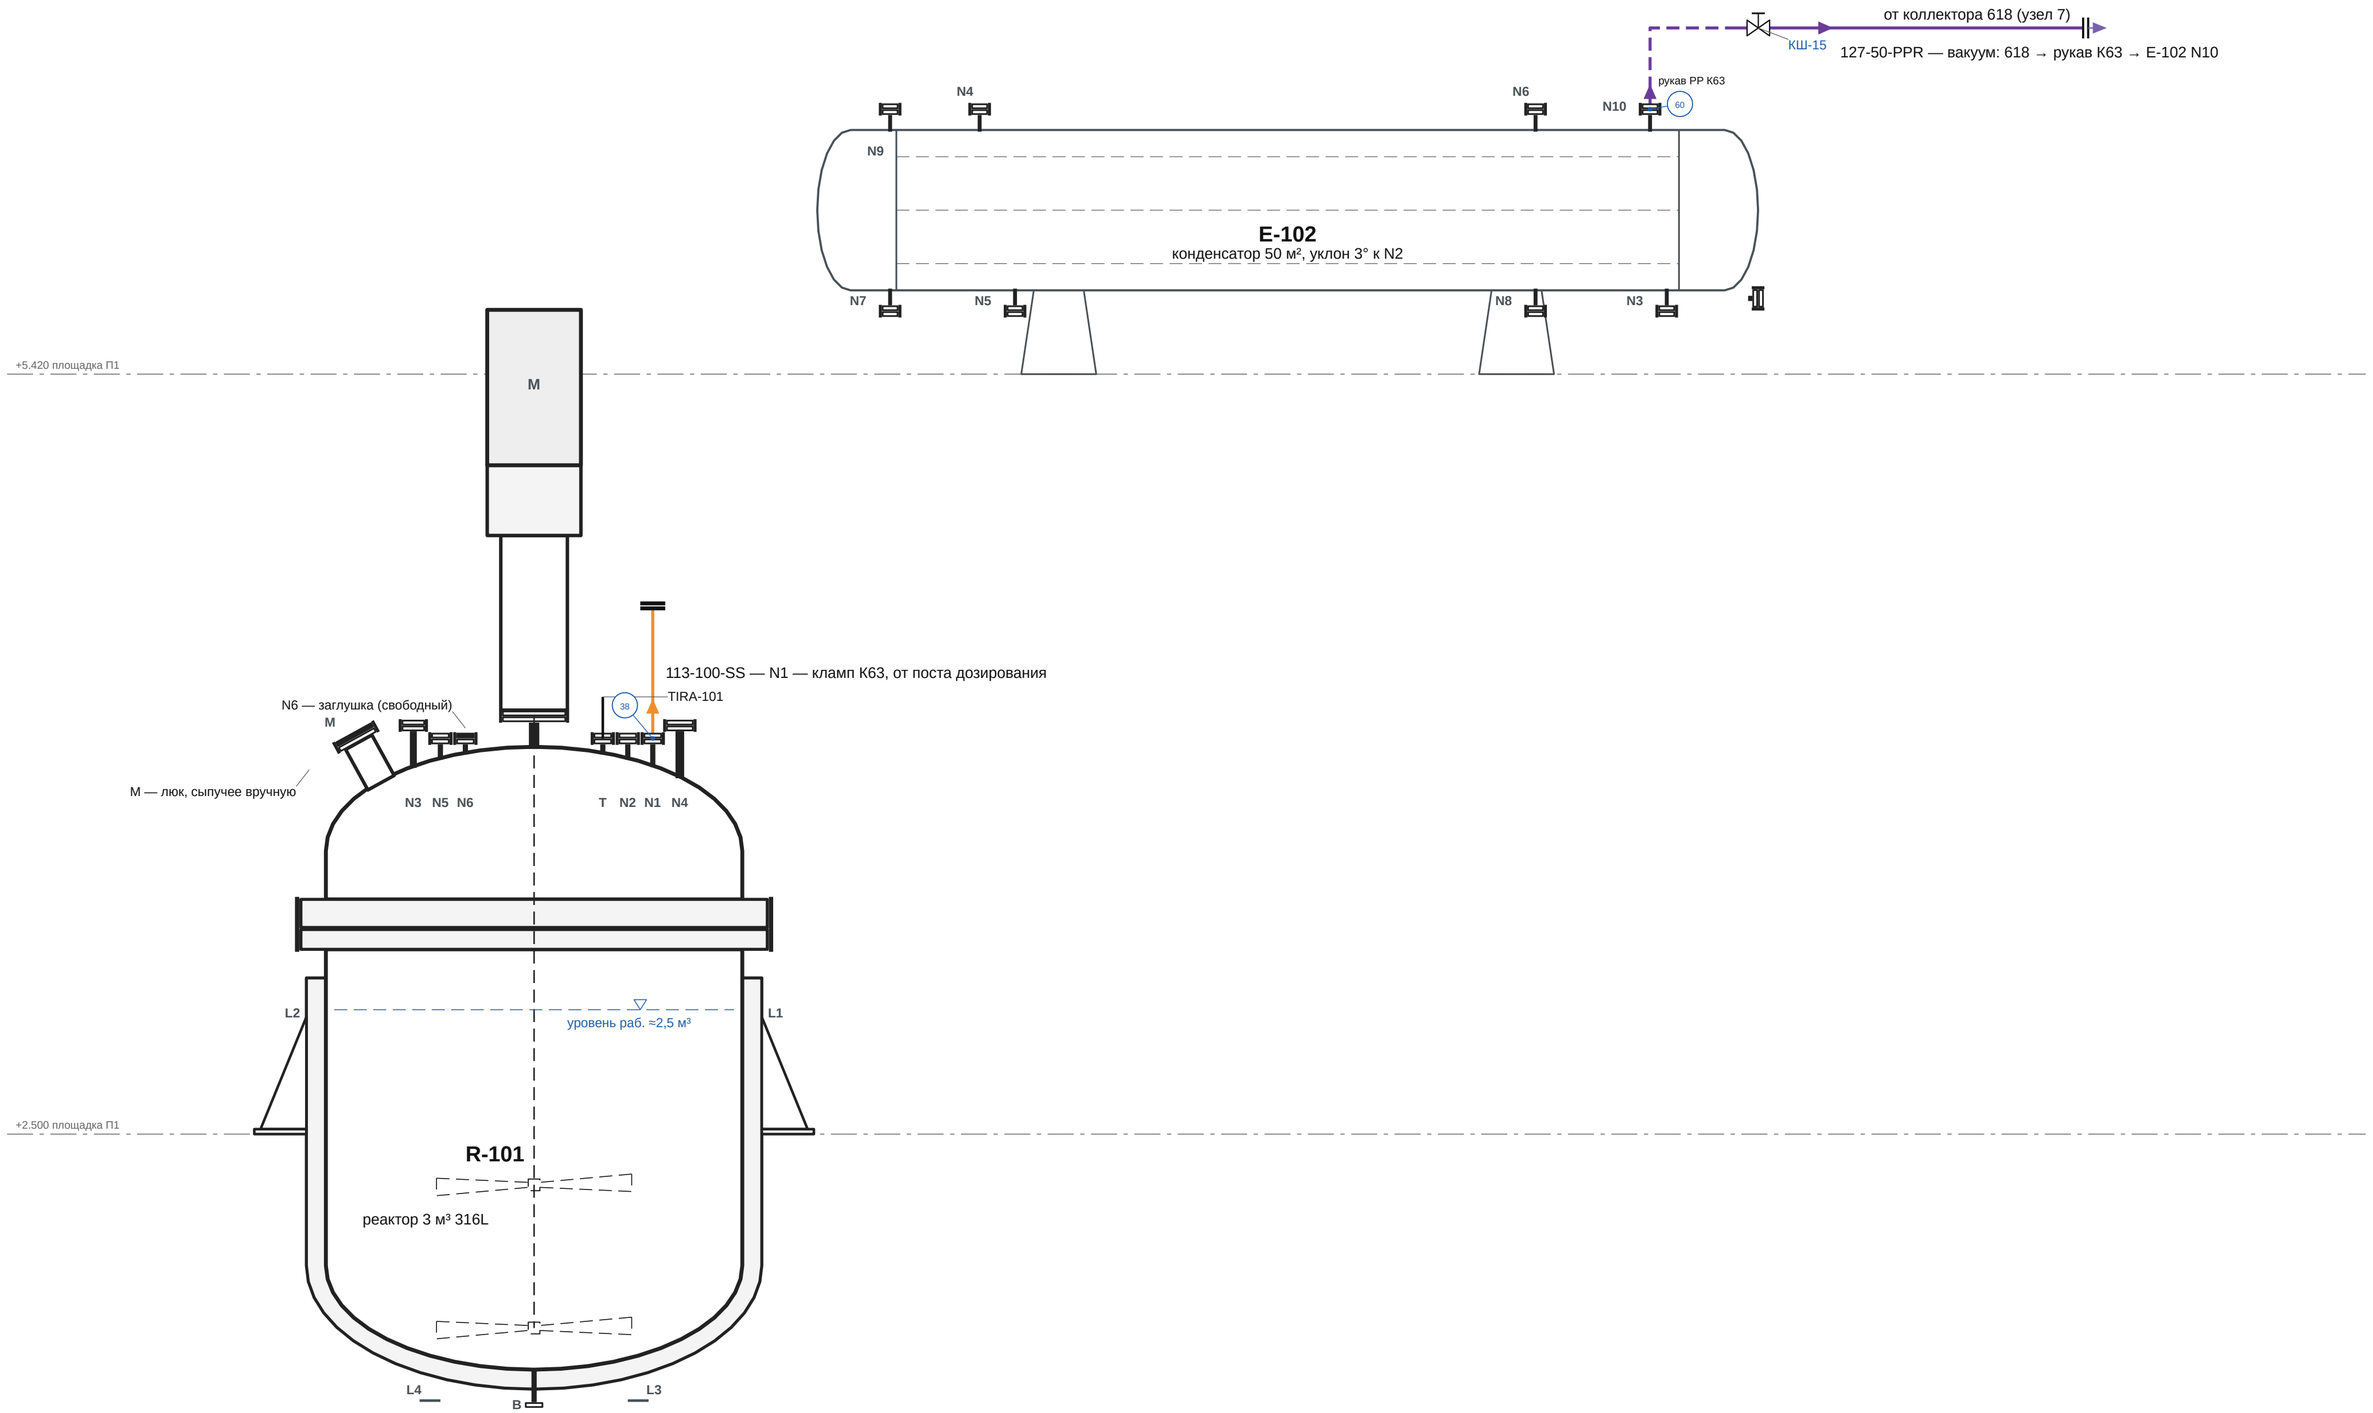

					ОПУ.ОБ.R-101.М.05	
Изм.	Лист	№ докум.	Подп.	Дата		
Разраб.					**Реактор 3 м³ 316L (R-101): вакуум**	Лит. П / Масса — / Масштаб б/м
Пров.						Лист 5 / Листов 16
Т.контр.						
Н.контр.						
Утв.					Опытно-промышленный участок	**Опытно-промышленный участок**

Сдувка 114 с конденсатора (E-102) N9, азот 123 на сборник (X-103)


Аппараты целиком, М 1:19; отметки — по 3D-модели; номера соединений — как в ведомости соединений

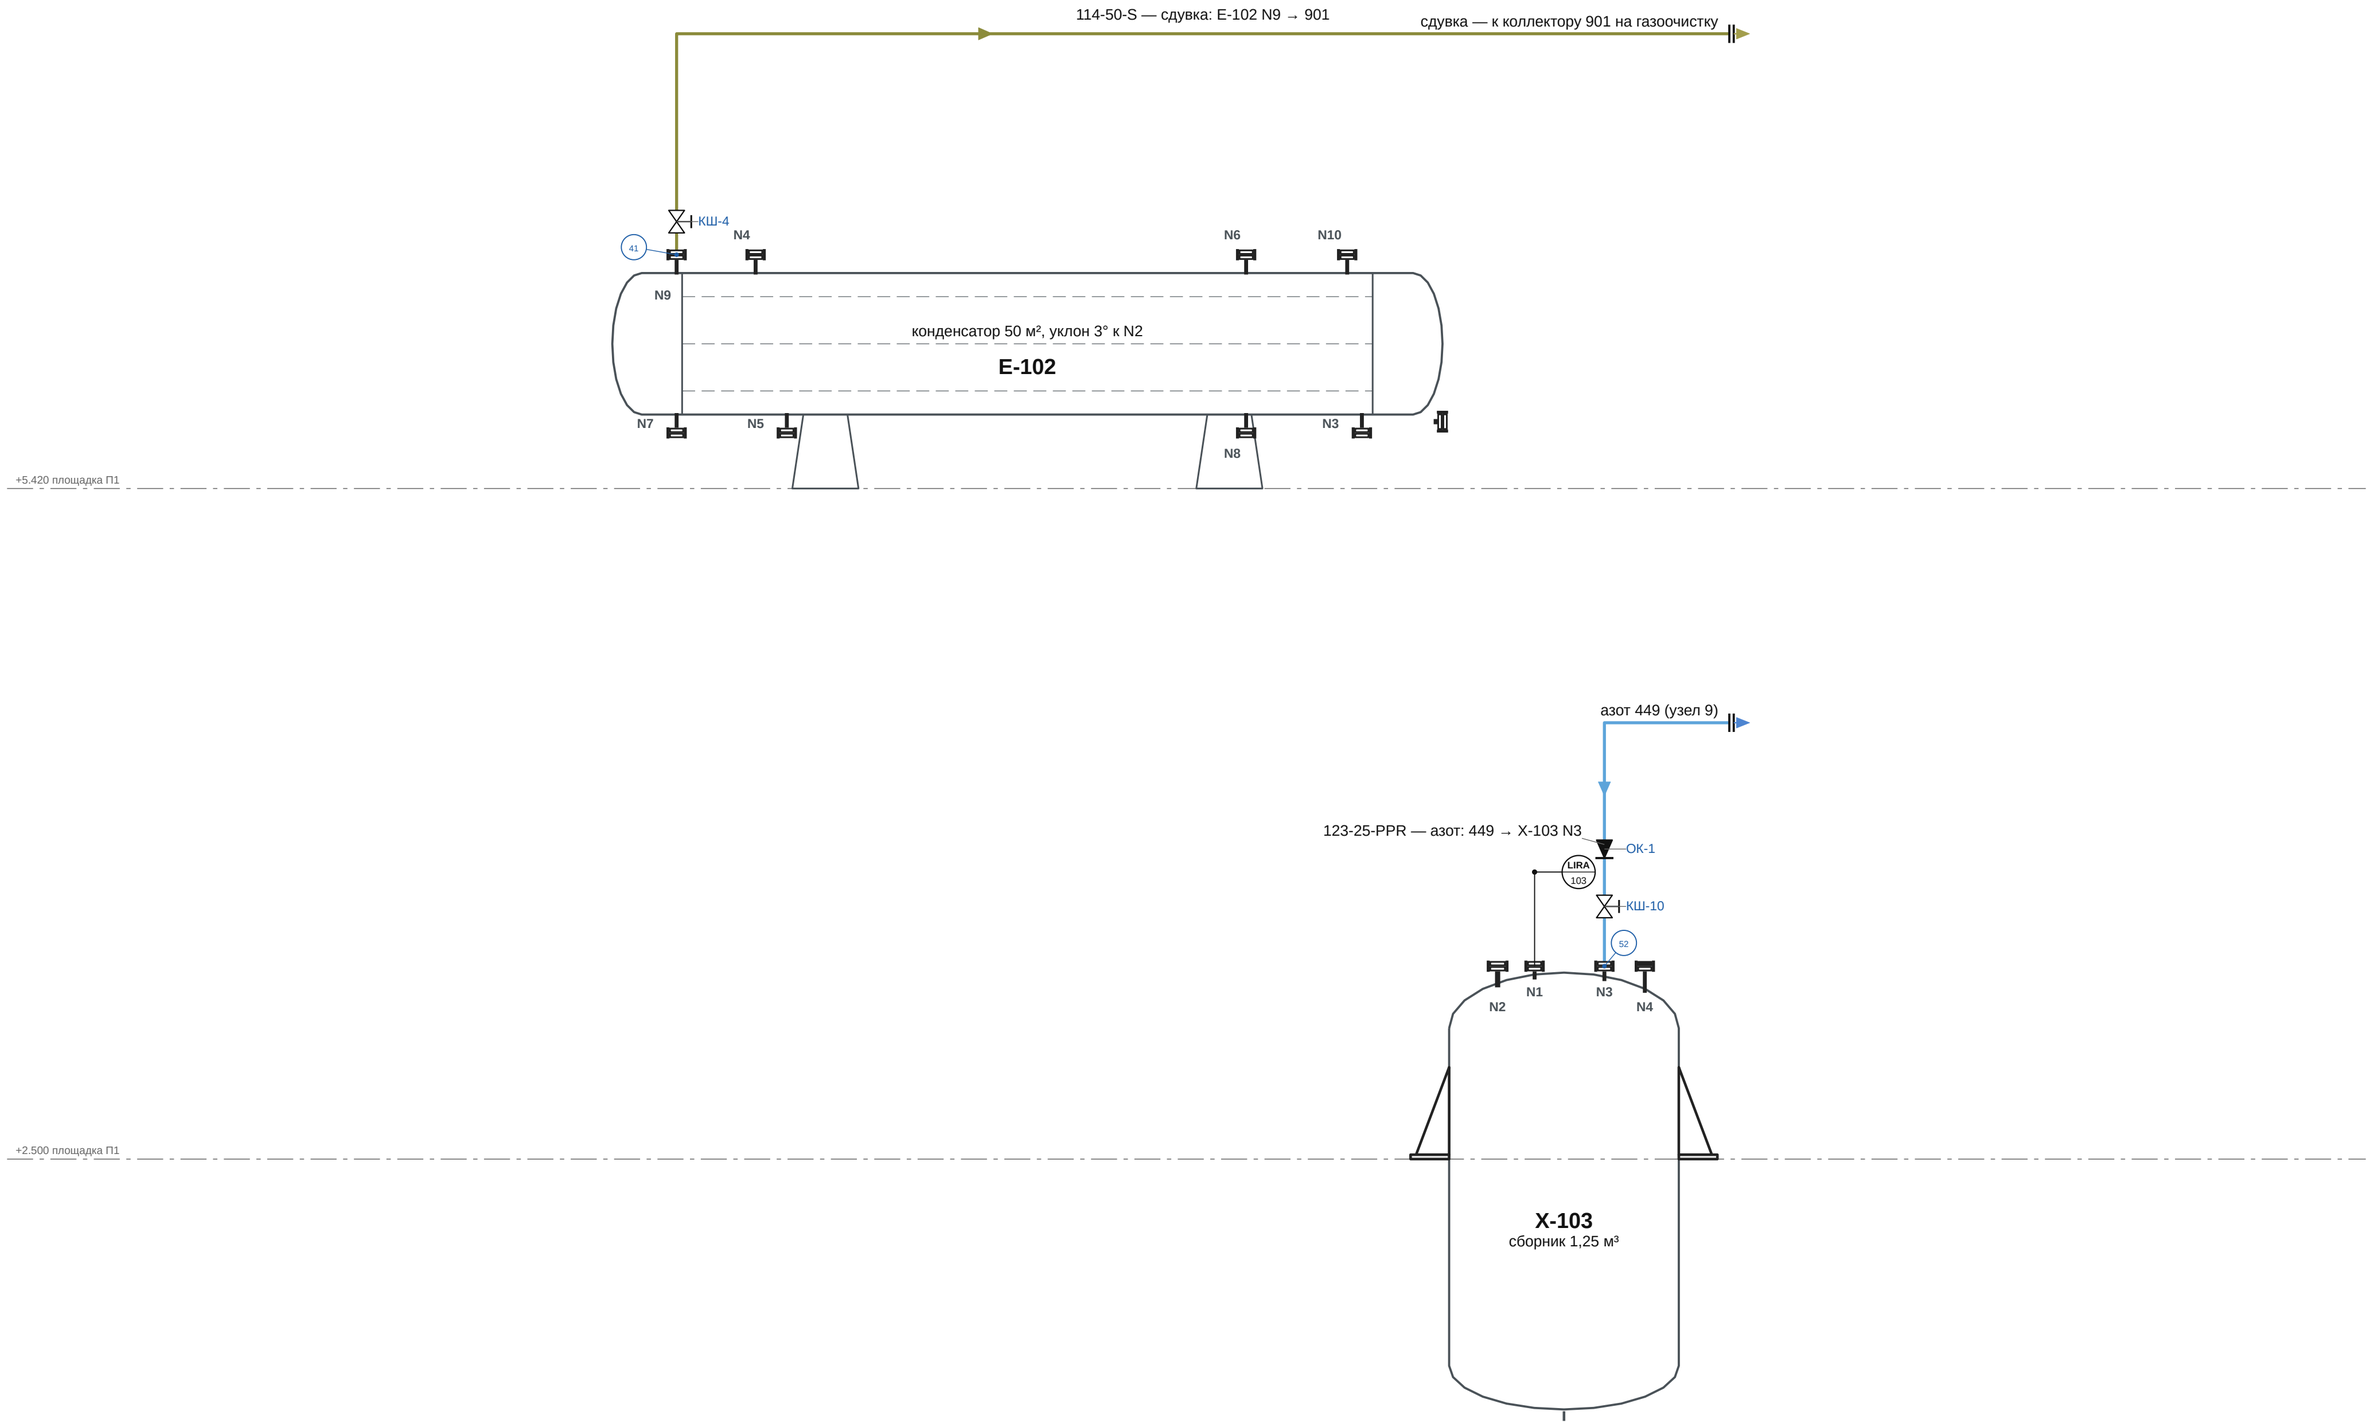

					ОПУ.ОБ.R-101.М.06	
Изм.	Лист	№ докум.	Подп.	Дата		
Разраб.					**Реактор 3 м³ 316L (R-101): сдувка** конденсатора, азот сборника	Лит. П; Масса —; Масштаб б/м
Пров.						Лист 6; Листов 16
Т.контр.						
Н.контр.					Опытно-промышленный участок	**Опытно-промышленный участок**
Утв.						

Вода охлаждения конденсатора (E-102): подача 117 на N3, возврат 118 с N4 (магистрали 707/711 у пола); дренаж и воздушник межтрубного N5, N6


Аппараты целиком, М 1:21; отметки — по 3D-модели; номера соединений — как в ведомости соединений

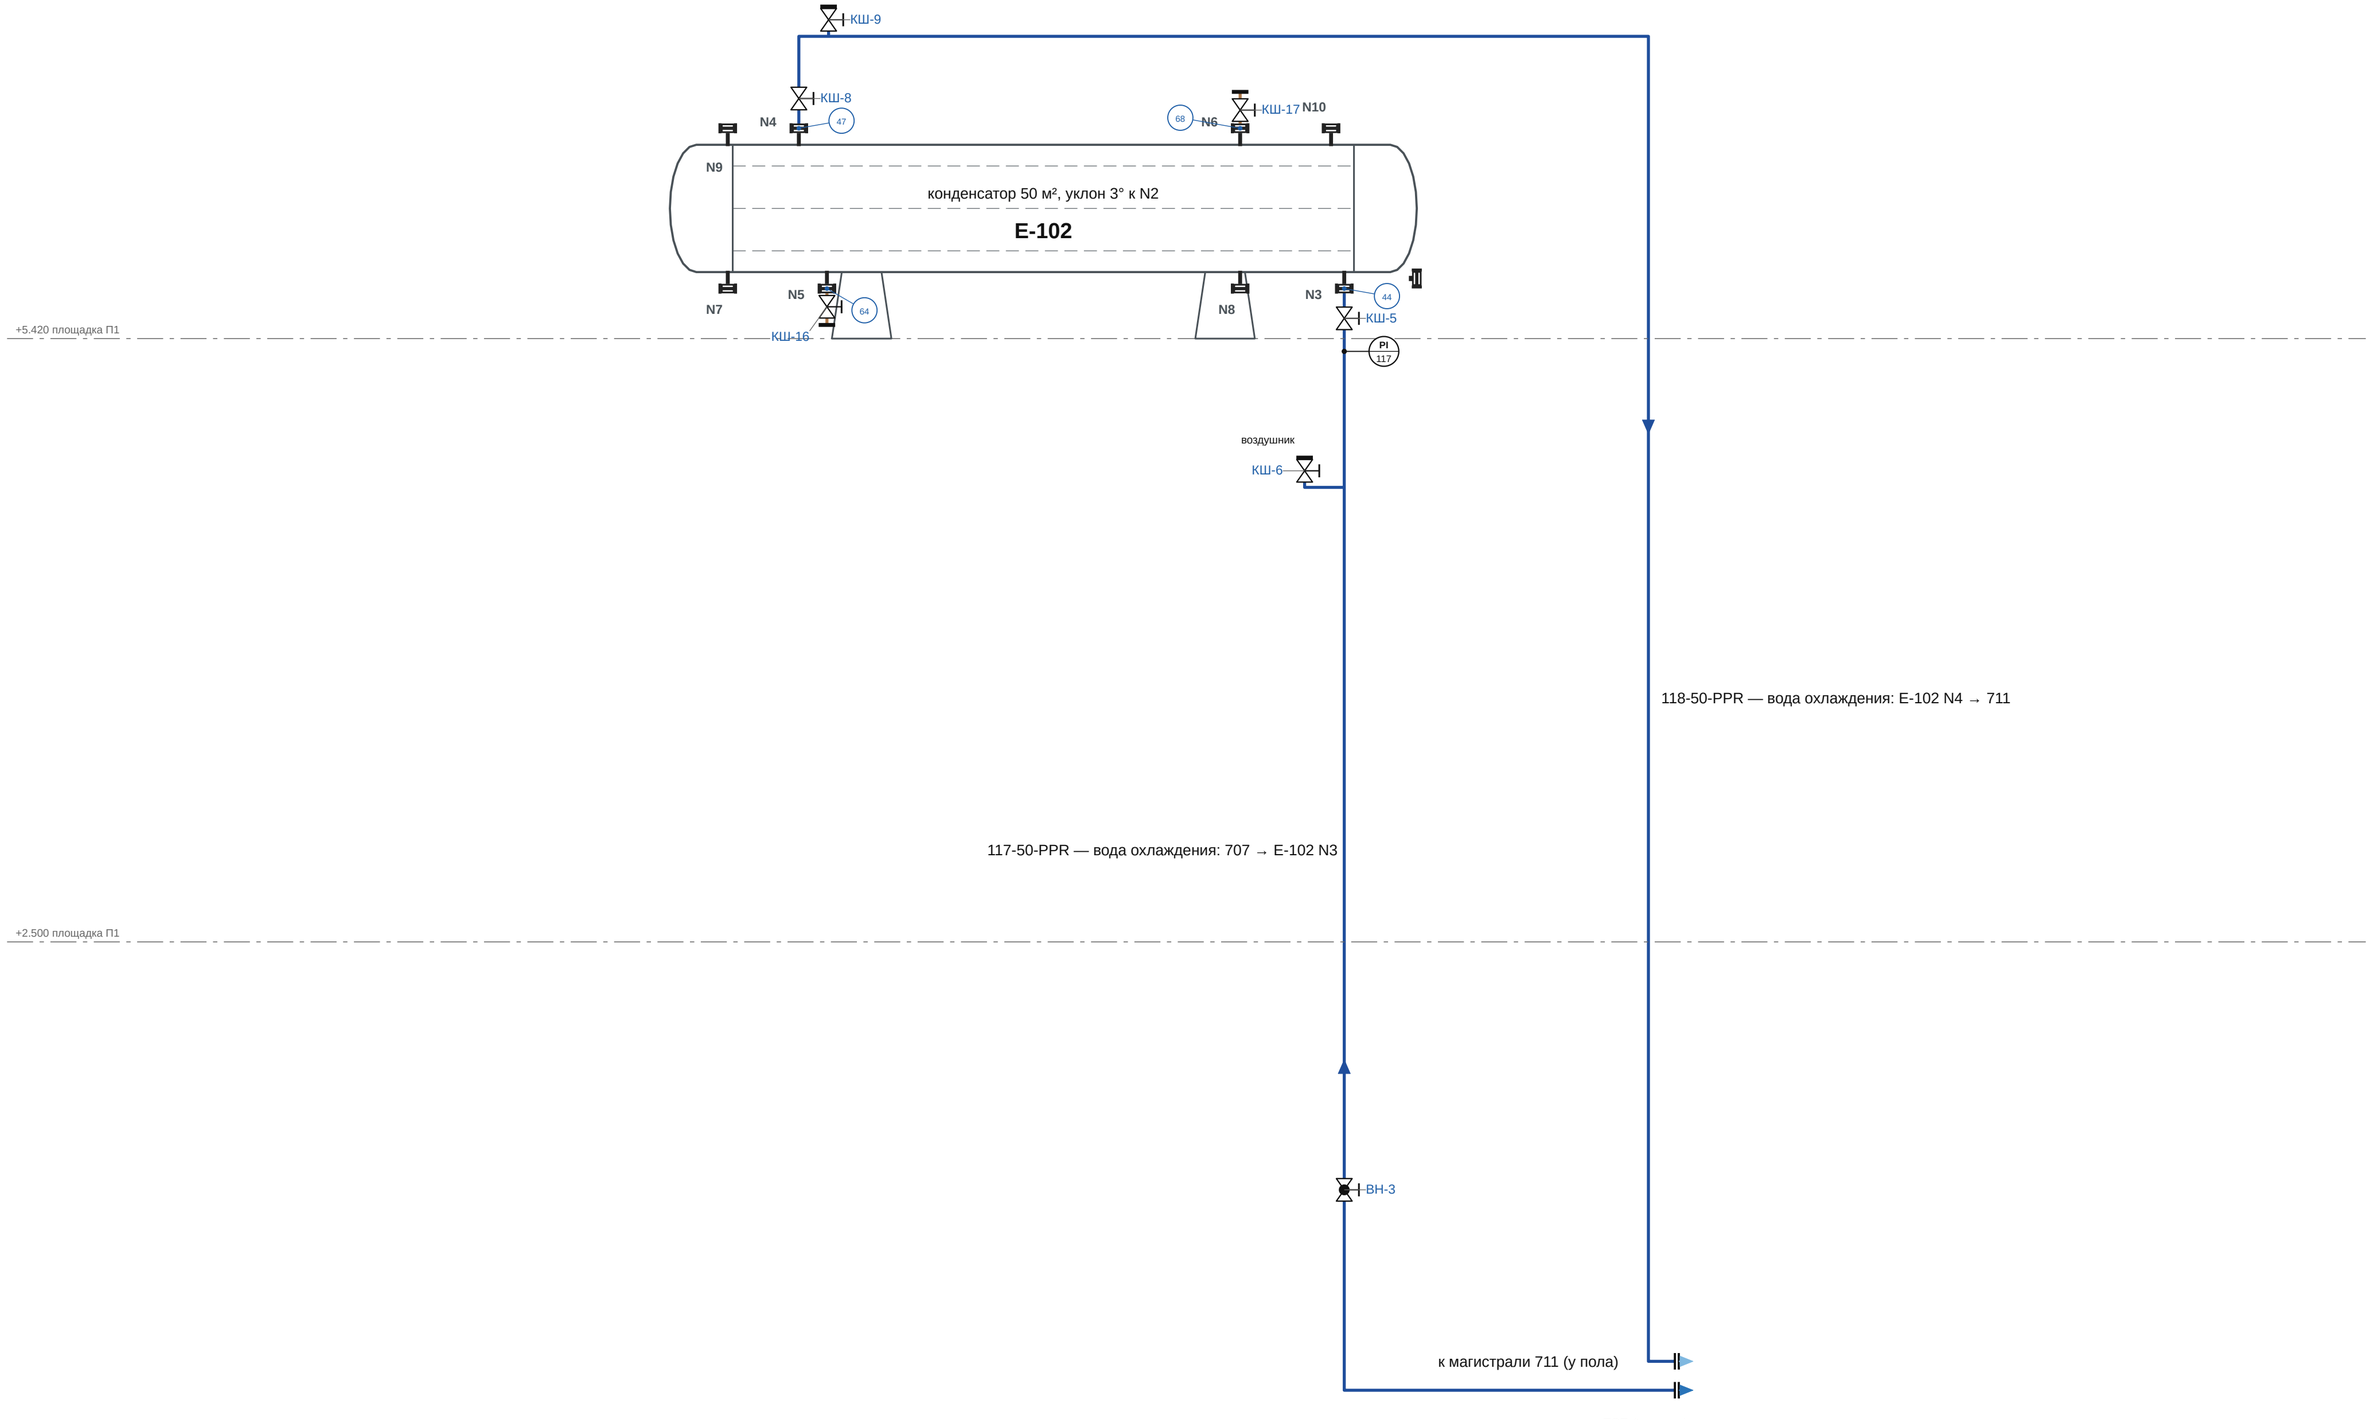

Изм.	Лист	№ докум.	Подп.	Дата	ОПУ.ОБ.R-101.М.07			
Разраб.					Реактор 3 м³ 316L (R-101): вода охлаждения конденсатора	Лит.	Масса	Масштаб
Пров.						П	—	б/м
Т.контр.						Лист 7		Листов 16
Н.контр.					Опытно-промышленный участок	Опытно-промышленный участок		
Утв.								

Рубашка реактора (R-101): подача 125 в L3/L4 (+2,152 под П1), возврат 126 из L1/L2 (+1,952, подъём с краном) — по трассам теплоносителя, от термостата X-104

Аппараты целиком, М 1:15; отметки — по 3D-модели; номера соединений — как в ведомости соединений

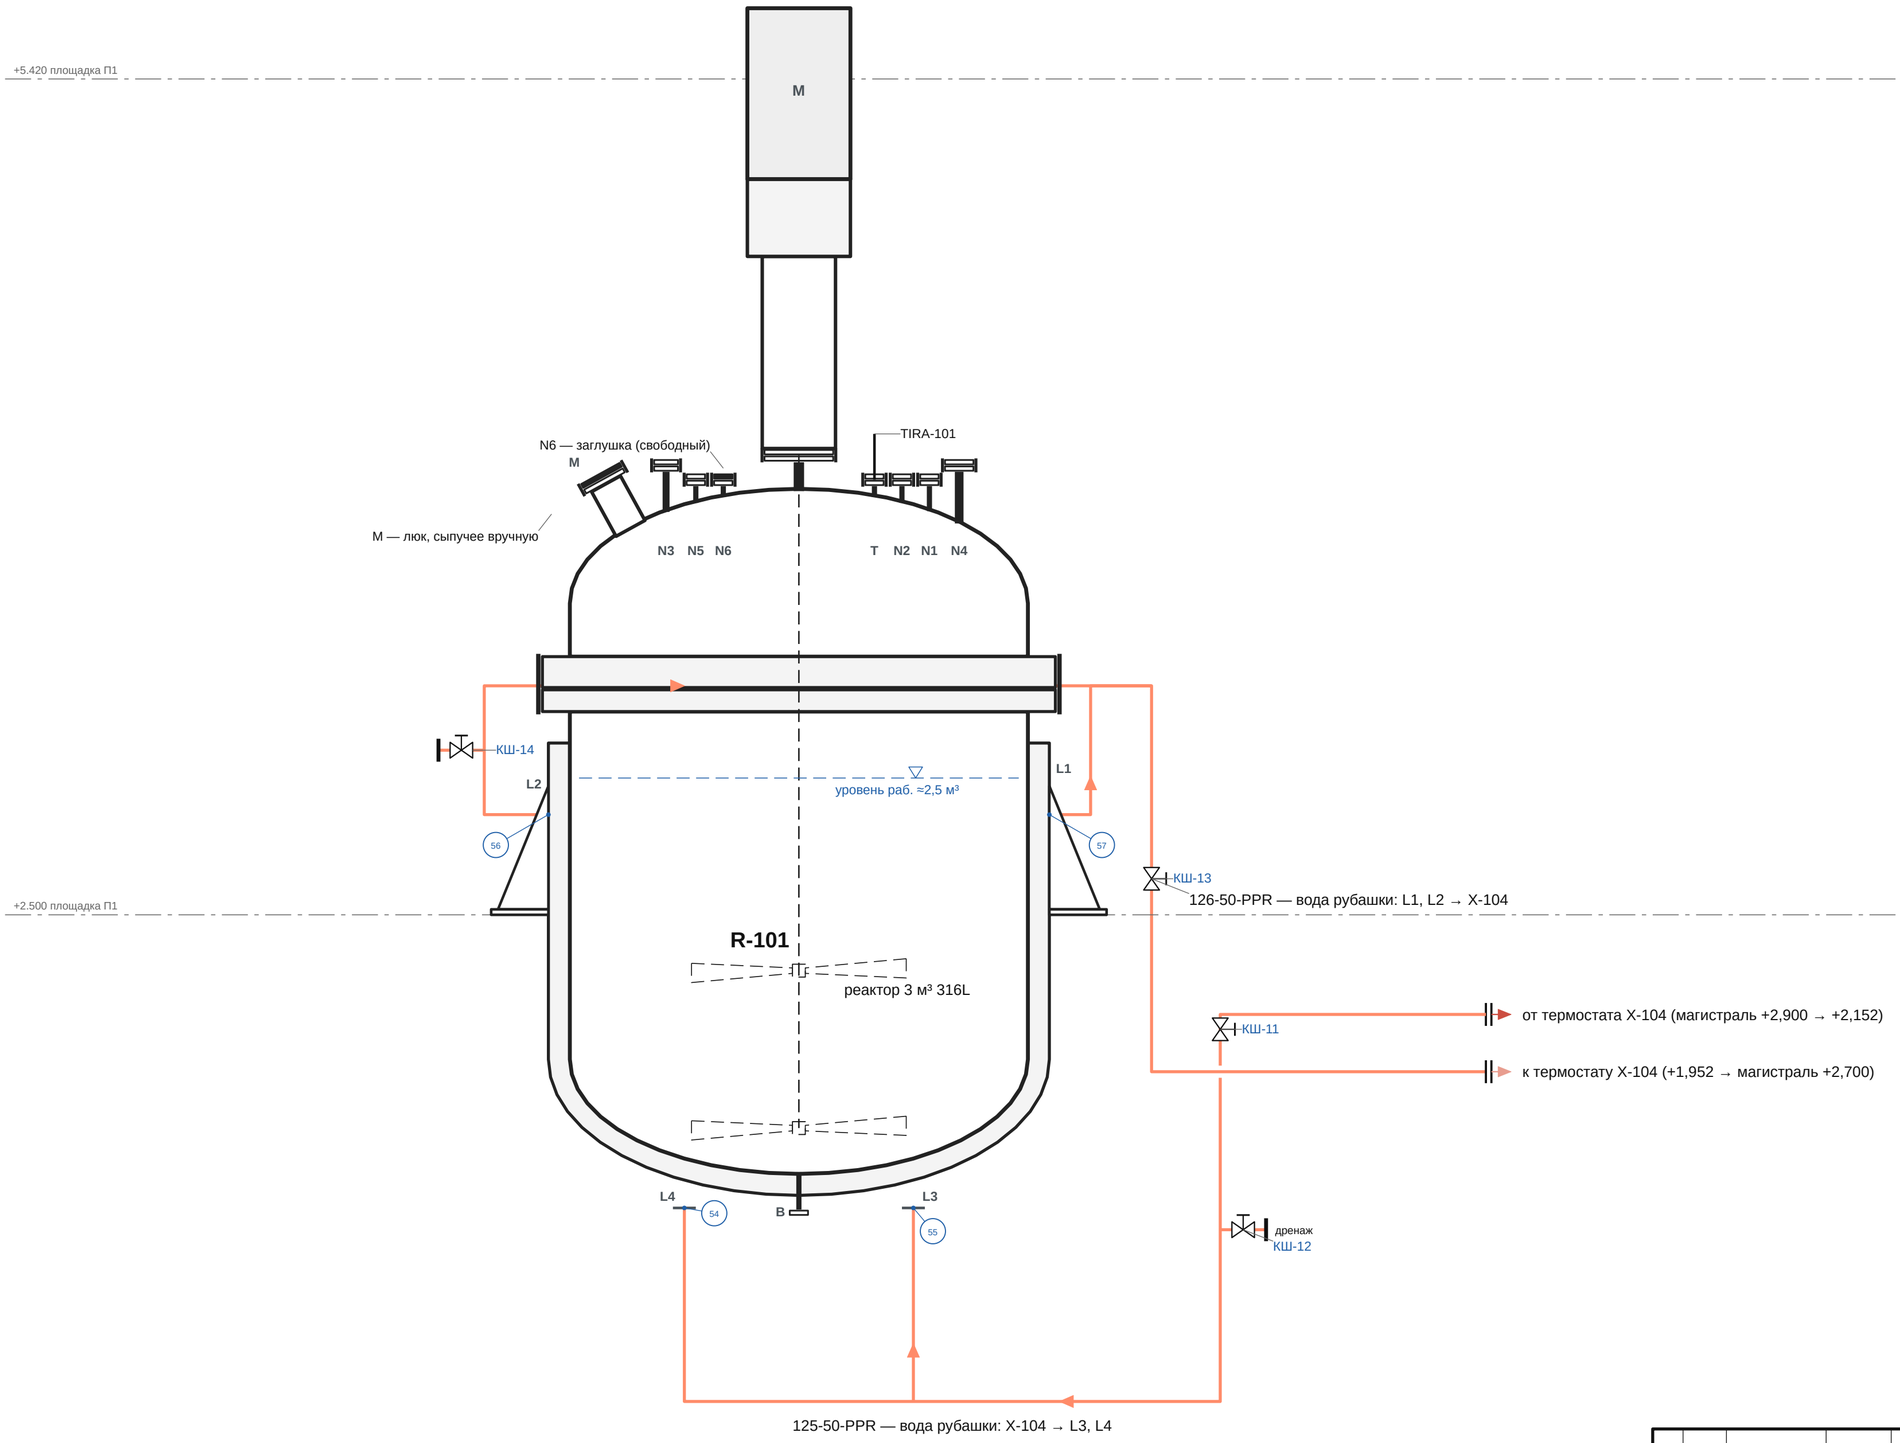

Изм.	Лист	№ докум.	Подп.	Дата	**ОПУ.ОБ.R-101.М.08**	
Разраб.					**Реактор 3 м³ 316L (R-101):** рубашка реактора	Лит. П; Масса —; Масштаб б/м
Пров.						Лист 8; Листов 16
Т.контр.						
Н.контр.					Опытно-промышленный участок	**Опытно-промышленный участок**
Утв.						

Аварийный сброс 110-200-S: мембрана на N3 → ёмкость аварийная (V-301/1) на улице; ниже мембраны — гребёнка защиты ГЗ-101 (К73): шпунт-аппарат, обратный клапан → 114, азот 112, мановакуумметр, сброс на атмосферу

Аппараты целиком, М 1:18; отметки — по 3D-модели; номера соединений — как в ведомости соединений

+5.420 площадка П1

+2.500 площадка П1

±0.000 пол

110-200-S — аварийный сброс: R-101 N3 → V-301/1

114-50-S — сдувка → 901

сдувка 114 → коллектор 901

PI 101

ОК-2

шпунт АР-5

КШК-3

КШК-4

КШК-2

на атмосферу

КШК-5

ГЗ-101 — гребёнка защиты

КШК-1

мембрана СМ200, датчик разрыва BSA-101

112-25-PPR — азот: 449 → гребёнка защиты

ротаметр, редуктор

АР-4

азот 112 ← коллектор 449

М — люк, сыпучее вручную

33

32

M

TIRA-101

N3 N5 N6

T N2 N1 N4

L2

L1

уровень раб. ≈2,5 м³

R-101

реактор 3 м³ 316L

L4

L3

B

V-301/1

ёмкость аварийная РГС-5
на улице (К36)

Изм.	Лист	№ докум.	Подп.	Дата
Разраб.				
Пров.				
Т.контр.				
Н.контр.				
Утв.				

ОПУ.ОБ.R-101.М.09

Реактор 3 м³ 316L (R-101):
аварийный сброс 110, гребёнка защиты

Лит.	Масса	Масштаб
П	—	б/м


Лист 9 | Листов 16

Опытно-промышленный участок

Опытно-промышленный участок

Продукты в еврокубы (K71): реактор (R-101) — 105 через насос AODD в еврокуб на тележке; сборник (X-103) — 104 рукавом в еврокуб на тележке → регенерация (X-600)

Аппараты целиком, М 1:18; отметки — по 3D-модели; номера соединений — как в ведомости соединений

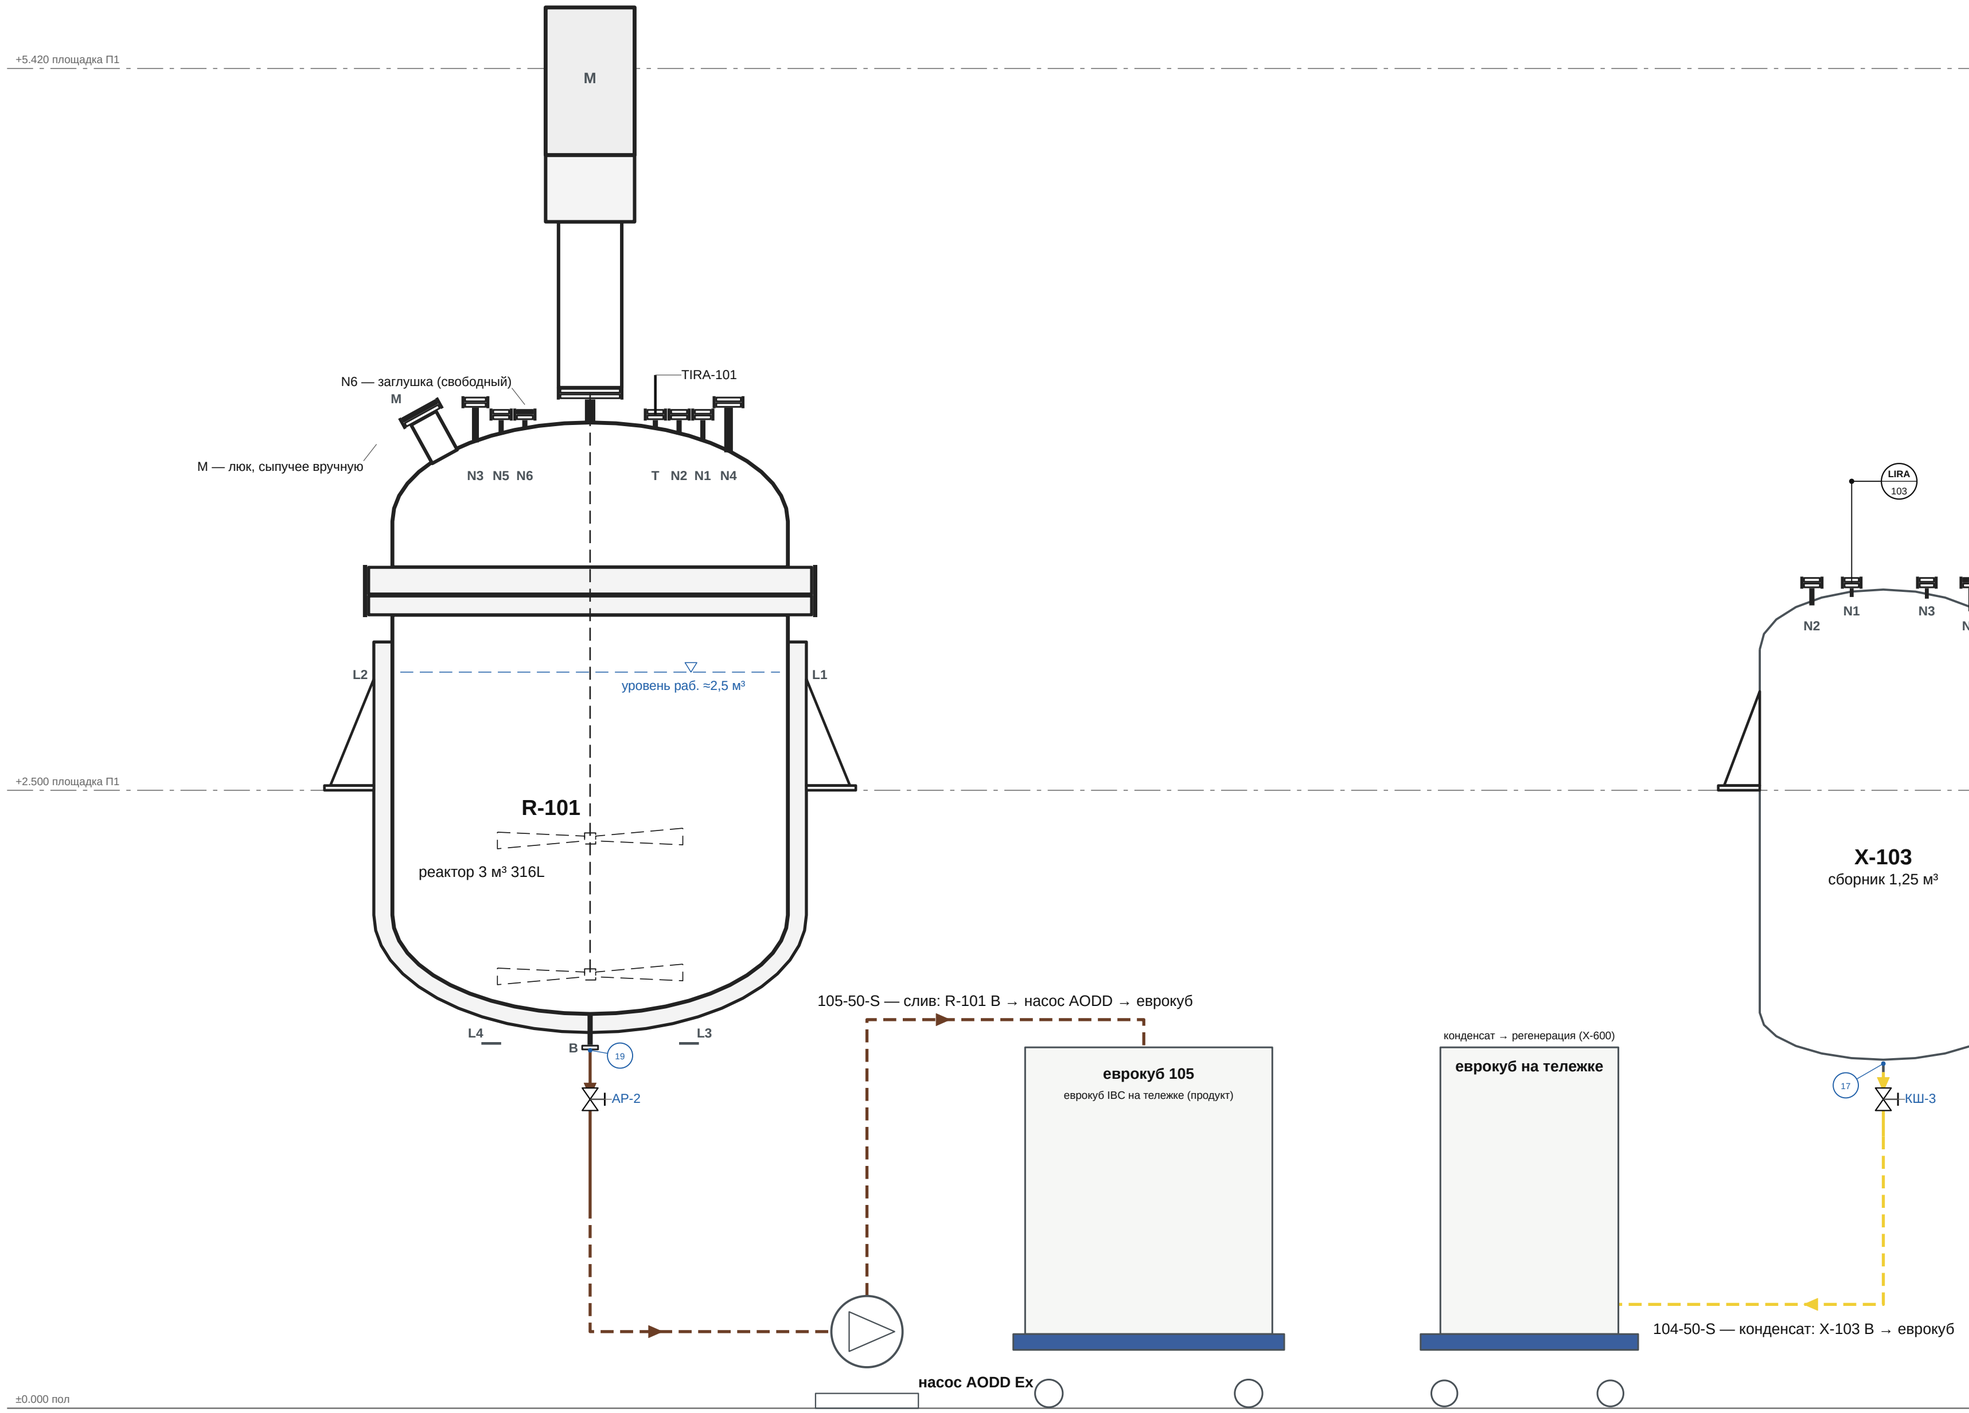

Изм.	Лист	№ докум.	Подп.	Дата
Разраб.				
Пров.				
Т.контр.				
Н.контр.				
Утв.				

ОПУ.ОБ.R-101.М.10

Реактор 3 м³ 316L (R-101):
продукты в еврокубы

Лит.	Масса	Масштаб
П	—	б/м

Лист 10 | Листов 16

Опытно-промышленный участок

Опытно-промышленный участок

ВЕДОМОСТЬ СОЕДИНЕНИЙ (1)

№	Линия	DN	Тип	Крепёж и прокладка	X, мм	Y, мм	Отм., м
1	101-300-SS	300	фланцевое	16 шпилек M27×143 с гайками (A2-70), прокладка PTFE (фторопласт-4)	15010	13026	+6,05
2	101-300-SS	300	фланцевое	соединение фланцевое DN300 PN25 — разъём шлемовой трубы (верх), 16 шпилек M27, прокладка PTFE	15010	13624	+5,48
3	101-300-SS	300	фланцевое	соединение фланцевое DN300 PN25 — разъём шлемовой трубы (середина), 16 шпилек M27, прокладка PTFE	15010	13624	+4,84
4	101-300-SS	300	фланцевое	16 шпилек M27×143 с гайками (A2-70), прокладка PTFE (фторопласт-4)	15010	13624	+4,07
5	102-100-SS	100	фланцевое	8 шпилек M20×106 с гайками (A2-70), прокладка PTFE (фторопласт-4)	15010	9422	+5,71
6	102-100-SS	100	фланцевое	8 шпилек M20×106 с гайками (A2-70), прокладка PTFE (фторопласт-4)	15010	9188	+5,03
7	102-100-SS	100	фланцевое	8 шпилек M20×106 с гайками (A2-70), прокладка PTFE (фторопласт-4)	15010	9188	+4,79
8	102-100-SS	100	фланцевое	8 шпилек M20×106 с гайками (A2-70), прокладка PTFE (фторопласт-4)	15010	9188	+4,58
9	102-100-SS	100	фланцевое	8 шпилек M20×106 с гайками (A2-70), прокладка PTFE (фторопласт-4)	15010	9188	+4,26
10	102-100-SS	80	фланцевое	8 шпилек M16×88 с гайками (A2-70), прокладка PTFE (фторопласт-4)	15010	9188	+3,28
11	103-25-SS	25	фланцевое	4 шпилек M12×73 с гайками (A2-70), прокладка PTFE (фторопласт-4)	15010	12571	+5,60
12	103-25-SS	25	фланцевое	4 шпилек M12×73 с гайками (A2-70), прокладка PTFE (фторопласт-4)	15010	9924	+5,46
13	103-25-SS	25	фланцевое	4 шпилек M12×73 с гайками (A2-70), прокладка PTFE (фторопласт-4)	15130	9945	+5,06
14	103-25-SS	25	фланцевое	4 шпилек M12×73 с гайками (A2-70), прокладка PTFE (фторопласт-4)	15257	9945	+5,06
15	103-25-SS	25	фланцевое	4 шпилек M12×73 с гайками (A2-70), прокладка PTFE (фторопласт-4)	15130	12599	+5,06
16	103-25-SS	25	фланцевое	4 шпилек M12×73 с гайками (A2-70), прокладка PTFE (фторопласт-4)	15257	12599	+5,06
17	104-50-S	50	фланцевое	4 шпилек M16×84 с гайками (A2-70), прокладка PTFE (фторопласт-4)	15280	9320	+1,39
18	104-50-S	50	фланцевое	4 шпилек M16×84 с гайками (A2-70), прокладка PTFE (фторопласт-4)	15280	9320	+1,24
19	105-50-S	100	фланцевое	8 шпилек M20×106 с гайками (A2-70), прокладка PTFE (фторопласт-4)	15470	14010	+1,45
20	105-50-S	100	фланцевое	8 шпилек M20×106 с гайками (A2-70), прокладка PTFE (фторопласт-4)	15470	13797	+1,15
21	105-50-S	50	фланцевое	4 шпилек M16×84 с гайками (A2-70), прокладка PTFE (фторопласт-4)	15470	13703	+1,05
22	107-50-SS	100	фланцевое	8 шпилек M20×106 с гайками (A2-70), прокладка PTFE (фторопласт-4)	15010	9346	+4,42
23	107-50-SS	50	фланцевое	4 шпилек M16×88 с гайками (A2-70), прокладка PTFE (фторопласт-4)	15010	9562	+4,42
24	107-50-SS	50	фланцевое	4 шпилек M16×88 с гайками (A2-70), прокладка PTFE (фторопласт-4)	15010	9754	+4,42
25	107-50-SS	50	фланцевое	4 шпилек M16×88 с гайками (A2-70), прокладка PTFE (фторопласт-4)	15010	12743	+4,30
26	107-50-SS	50	фланцевое	4 шпилек M16×88 с гайками (A2-70), прокладка PTFE (фторопласт-4)	15010	12974	+4,29
27	107-50-SS	50	фланцевое	4 шпилек M16×88 с гайками (A2-70), прокладка PTFE (фторопласт-4)	15010	13322	+4,27
28	108-25-SS	25	фланцевое	4 шпилек M12×73 с гайками (A2-70), прокладка PTFE (фторопласт-4)	15010	11008	+3,70
29	108-25-SS	25	фланцевое	4 шпилек M12×73 с гайками (A2-70), прокладка PTFE (фторопласт-4)	15010	10846	+3,69
30	110-200-S	200	фланцевое	12 шпилек M20 насквозь, прокладки — в держателе	15724	13466	+4,64
31	110-200-S	200	фланцевое	12 шпилек M24, прокладка паронит	15724	13466	+4,27
32	110-200-S	200	фланцевое	12 шпилек M24×128 с гайками (A2-70), прокладка PTFE (фторопласт-4)	15724	13466	+4,07
33	110-200-S	200	фланцевое	12 шпилек M20×106 с гайками (A2-70), прокладка PTFE (фторопласт-4)	17700	20000	+2,46
34	112-25-PPR		кламповое	соединение кламповое Ø25 (хомут AISI 304 с барашковой гайкой, прокладка PTFE)	14853	12976	+4,46
35	112-25-PPR		кламповое	соединение кламповое Ø25 (хомут AISI 304 с барашковой гайкой, прокладка PTFE)	14853	12976	+4,37
36	112-25-PPR	25	фланцевое	4 шпилек M12×86 с гайками (A2-70), прокладка EPDM	14848	12966	+3,83
37	113-100-SS		кламповое	соединение кламповое Ø64 (хомут AISI 304 с барашковой гайкой, прокладка PTFE)	16060	14010	+4,11
38	113-100-SS	100	фланцевое	8 шпилек M20×106 с гайками (A2-70), прокладка PTFE (фторопласт-4)	16070	14010	+4,02
39	114-50-S	50	фланцевое	4 шпилек M16×84 с гайками (A2-70), прокладка PTFE (фторопласт-4)	15583	12740	+6,92
40	114-50-S	50	фланцевое	4 шпилек M16×84 с гайками (A2-70), прокладка PTFE (фторопласт-4)	15735	12740	+6,92

Изм.	Лист	№ докум.	Подп.	Дата
Разраб.				
Пров.				
Т.контр.				
Н.контр.				
Утв.				

ОПУ.ОБ.R-101.М.11

Реактор 3 м³ 316L (R-101):
ведомость соединений (1)

Лит.	Масса	Масштаб
П	—	б/м

Лист 11 | Листов 16

Опытно-промышленный участок

Опытно-промышленный участок

ВЕДОМОСТЬ СОЕДИНЕНИЙ (2)

№	Линия	DN	Тип	Крепёж и прокладка	X, мм	Y, мм	Отм., м
41	114-50-S	25	фланцевое	4 шпилек M12×73 с гайками (A2-70), прокладка PTFE (фторопласт-4)	15010	12526	+6,45
42	114-50-S		кламповое	соединение кламповое Ø25 (хомут AISI 304 с барашковой гайкой, прокладка PTFE)	15313	12904	+5,01
43	114-50-S		кламповое	соединение кламповое Ø25 (хомут AISI 304 с барашковой гайкой, прокладка PTFE)	15298	12961	+4,95
44	117-50-PPR	50	фланцевое	4 шпилек M16×84 с гайками (A2-70), прокладка паронитовая ПОН-Б	15010	10189	+5,47
45	117-50-PPR	50	фланцевое	4 шпилек M16×97 с гайками (A2-70), прокладка EPDM	15010	10211	+5,05
46	117-50-PPR	50	фланцевое	4 шпилек M16×109 с гайками (A2-70), прокладка EPDM	15490	11180	+0,21
47	118-50-PPR	50	фланцевое	4 шпилек M16×97 с гайками (A2-70), прокладка EPDM	15010	12261	+6,45
48	118-50-PPR	50	фланцевое	4 шпилек M16×109 с гайками (A2-70), прокладка EPDM	15630	11804	+0,21
49	123-25-PPR	25	фланцевое	4 шпилек M12×86 с гайками (A2-70), прокладка EPDM	15212	9610	+3,92
50	123-25-PPR	25	фланцевое	4 шпилек M12×73 с гайками (A2-70), прокладка PTFE (фторопласт-4)	15212	9610	+3,75
51	123-25-PPR	25	фланцевое	4 шпилек M12×73 с гайками (A2-70), прокладка PTFE (фторопласт-4)	15212	9610	+3,63
52	123-25-PPR	50	фланцевое	4 шпилек M16×84 с гайками (A2-70), прокладка PTFE (фторопласт-4)	15031	9488	+3,28
53	125-50-PPR	50	фланцевое	4 шпилек M16×109 с гайками (A2-70), прокладка EPDM	14002	16378	+2,15
54	125-50-PPR	50	фланцевое	4 шпилек M16×97 с гайками (A2-70), прокладка EPDM	15070	14010	+1,47
55	125-50-PPR	50	фланцевое	4 шпилек M16×97 с гайками (A2-70), прокладка EPDM	15870	14010	+1,47
56	126-50-PPR	50	фланцевое	4 шпилек M16×97 с гайками (A2-70), прокладка EPDM	14458	14010	+2,85
57	126-50-PPR	50	фланцевое	4 шпилек M16×97 с гайками (A2-70), прокладка EPDM	16482	14010	+2,85
58	126-50-PPR	50	фланцевое	4 шпилек M16×109 с гайками (A2-70), прокладка EPDM	14002	16378	+1,95
59	127-50-PPR		кламповое	соединение кламповое Ø64 (хомут AISI 304 с барашковой гайкой, прокладка PTFE)	15010	9865	+6,40
60	127-50-PPR	25	фланцевое	4 шпилек M12×73 с гайками (A2-70), прокладка PTFE (фторопласт-4)	15010	9879	+6,32
61	127-50-PPR		кламповое	соединение кламповое Ø64 (хомут AISI 304 с барашковой гайкой, прокладка PTFE)	15709	10508	+5,87
62	127-50-PPR	50	фланцевое	4 шпилек M16×96 с гайками (A2-70), прокладка PTFE (фторопласт-4)	15719	10508	+5,78
63	127-50-PPR	50	фланцевое	4 шпилек M16×109 с гайками (A2-70), прокладка EPDM	15719	10632	+5,06
64	E-102 N5	25	фланцевое	4 шпилек M12×73 с гайками (A2-70), прокладка PTFE (фторопласт-4)	15010	12306	+5,58
65	E-102 N5	25	фланцевое	4 шпилек M12×73 с гайками (A2-70), прокладка PTFE (фторопласт-4)	15097	12310	+5,51
66	E-102 N5	25	фланцевое	4 шпилек M12×73 с гайками (A2-70), прокладка PTFE (фторопласт-4)	15224	12310	+5,51
67	E-102 N6	25	фланцевое	4 шпилек M12×73 с гайками (A2-70), прокладка PTFE (фторопласт-4)	15010	10137	+6,46
68	E-102 N6	25	фланцевое	4 шпилек M12×73 с гайками (A2-70), прокладка PTFE (фторопласт-4)	15010	10144	+6,33
69	LIRA-103	50	фланцевое	4 шпилек M16×84 с гайками (A2-70), прокладка PTFE (фторопласт-4)	15259	9021	+3,28
70	PIR-101	25	фланцевое	4 шпилек M12×73 с гайками (A2-70), прокладка PTFE (фторопласт-4)	14870	14010	+4,28
71	PIR-101	25	фланцевое	4 шпилек M12×73 с гайками (A2-70), прокладка PTFE (фторопласт-4)	14870	14010	+4,15
72	PIR-101	100	фланцевое	8 шпилек M20×106 с гайками (A2-70), прокладка PTFE (фторопласт-4)	14870	14010	+4,02
73	SP-101	25	фланцевое	4 шпилек M12×73 с гайками (A2-70), прокладка PTFE (фторопласт-4)	15990	13710	+5,14
74	SP-101	25	фланцевое	4 шпилек M12×73 с гайками (A2-70), прокладка PTFE (фторопласт-4)	15990	13710	+5,02
75	SP-101	25	фланцевое	4 шпилек M12×73 с гайками (A2-70), прокладка PTFE (фторопласт-4)	15990	13710	+4,91
76	SP-101	25	фланцевое	4 шпилек M12×73 с гайками (A2-70), прокладка PTFE (фторопласт-4)	15990	13710	+4,66
77	SP-101	25	фланцевое	4 шпилек M12×73 с гайками (A2-70), прокладка PTFE (фторопласт-4)	15990	13710	+4,56
78	SP-101	25	фланцевое	4 шпилек M12×73 с гайками (A2-70), прокладка PTFE (фторопласт-4)	15886	13710	+4,46
79	SP-101	25	фланцевое	4 шпилек M12×73 с гайками (A2-70), прокладка PTFE (фторопласт-4)	15990	13710	+4,35
80	SP-101	25	фланцевое	4 шпилек M12×73 с гайками (A2-70), прокладка PTFE (фторопласт-4)	15990	13710	+4,24

Изм.	Лист	№ докум.	Подп.	Дата
Разраб.				
Пров.				
Т.контр.				
Н.контр.				
Утв.				

ОПУ.ОБ.R-101.М.12

Реактор 3 м³ 316L (R-101):
ведомость соединений (2)

Лит.	Масса	Масштаб
П	—	б/м

Лист 12 | Листов 16

Опытно-промышленный участок

Опытно-промышленный участок

ВЕДОМОСТЬ СОЕДИНЕНИЙ (3)

№	Линия	DN	Тип	Крепёж и прокладка	X, мм	Y, мм	Отм., м
81	SP-101	25	фланцевое	4 шпилек M12×73 с гайками (A2-70), прокладка PTFE (фторопласт-4)	15990	13710	+4,11
82	SP-101	100	фланцевое	8 шпилек M20×106 с гайками (A2-70), прокладка PTFE (фторопласт-4)	15990	13710	+4,02
83	TIRA-101	100	фланцевое	8 шпилек M20×106 с гайками (A2-70), прокладка PTFE (фторопласт-4)	15990	14310	+4,02
84	X-103 N4		кламповое	соединение кламповое Ø64 (хомут AISI 304 с барашковой гайкой, прокладка PTFE)	15291	9619	+3,36
85	X-103 N4	50	фланцевое	4 шпилек M16×84 с гайками (A2-70), прокладка PTFE (фторопласт-4)	15301	9619	+3,28
86	ГЗ-101		кламповое	соединение кламповое Ø25 (хомут AISI 304 с барашковой гайкой, прокладка PTFE)	15442	12976	+4,89
87	ГЗ-101		кламповое	соединение кламповое Ø25 (хомут AISI 304 с барашковой гайкой, прокладка PTFE)	15369	12976	+4,89
88	ГЗ-101		кламповое	соединение кламповое Ø25 (хомут AISI 304 с барашковой гайкой, прокладка PTFE)	15303	12976	+4,83
89	ГЗ-101		кламповое	соединение кламповое Ø25 (хомут AISI 304 с барашковой гайкой, прокладка PTFE)	15533	12976	+4,81
90	ГЗ-101		кламповое	соединение кламповое Ø25 (хомут AISI 304 с барашковой гайкой, прокладка PTFE)	15303	12976	+4,78
91	ГЗ-101		кламповое	соединение кламповое Ø25 (хомут AISI 304 с барашковой гайкой, прокладка PTFE)	15533	12976	+4,67
92	ГЗ-101		кламповое	соединение кламповое Ø25 (хомут AISI 304 с барашковой гайкой, прокладка PTFE)	15303	12976	+4,67
93	ГЗ-101		кламповое	соединение кламповое Ø25 (хомут AISI 304 с барашковой гайкой, прокладка PTFE)	15073	12976	+4,67
94	ГЗ-101		кламповое	соединение кламповое Ø25 (хомут AISI 304 с барашковой гайкой, прокладка PTFE)	15533	12976	+4,58
95	ГЗ-101		кламповое	соединение кламповое Ø25 (хомут AISI 304 с барашковой гайкой, прокладка PTFE)	15303	12976	+4,58
96	ГЗ-101		кламповое	соединение кламповое Ø25 (хомут AISI 304 с барашковой гайкой, прокладка PTFE)	15073	12976	+4,58
97	ГЗ-101	50	фланцевое	4 шпилек M16×84 с гайками (A2-70), прокладка PTFE (фторопласт-4)	15724	13265	+4,52
98	ГЗ-101		кламповое	соединение кламповое Ø25 (хомут AISI 304 с барашковой гайкой, прокладка PTFE)	15662	12976	+4,51
99	ГЗ-101		кламповое	соединение кламповое Ø25 (хомут AISI 304 с барашковой гайкой, прокладка PTFE)	15599	12976	+4,51
100	ГЗ-101		кламповое	соединение кламповое Ø25 (хомут AISI 304 с барашковой гайкой, прокладка PTFE)	15478	12976	+4,51
101	ГЗ-101		кламповое	соединение кламповое Ø25 (хомут AISI 304 с барашковой гайкой, прокладка PTFE)	15369	12976	+4,51
102	ГЗ-101		кламповое	соединение кламповое Ø25 (хомут AISI 304 с барашковой гайкой, прокладка PTFE)	15248	12976	+4,51
103	ГЗ-101		кламповое	соединение кламповое Ø25 (хомут AISI 304 с барашковой гайкой, прокладка PTFE)	15139	12976	+4,51
104	ГЗ-101		кламповое	соединение кламповое Ø25 (хомут AISI 304 с барашковой гайкой, прокладка PTFE)	15018	12976	+4,51
105	ГЗ-101		кламповое	соединение кламповое Ø25 (хомут AISI 304 с барашковой гайкой, прокладка PTFE)	14909	12976	+4,51
106	ГЗ-101		кламповое	соединение кламповое Ø25 (хомут AISI 304 с барашковой гайкой, прокладка PTFE)	14788	12976	+4,51
107	ГЗ-101		кламповое	соединение кламповое Ø25 (хомут AISI 304 с барашковой гайкой, прокладка PTFE)	14725	12976	+4,51
108	ГЗ-101		кламповое	соединение кламповое Ø25 (хомут AISI 304 с барашковой гайкой, прокладка PTFE)	14632	12976	+4,51
109	ГЗ-101		кламповое	соединение кламповое Ø25 (хомут AISI 304 с барашковой гайкой, прокладка PTFE)	15729	13028	+4,51
110	ГЗ-101		кламповое	соединение кламповое Ø25 (хомут AISI 304 с барашковой гайкой, прокладка PTFE)	15729	13181	+4,51

Изм.	Лист	№ докум.	Подп.	Дата
Разраб.				
Пров.				
Т.контр.				
Н.контр.				
Утв.				

ОПУ.ОБ.R-101.М.13

Реактор 3 м³ 316L (R-101):
ведомость соединений (3)

Лит.	Масса	Масштаб
П	—	б/м

Лист 13 | Листов 16

Опытно-промышленный участок

Опытно-промышленный участок

ВЕДОМОСТЬ ТОЧЕК СТЫКА И ГРАНИЦ УЗЛА

Линия / точка	DN	X, мм	Y, мм	Отм., м	Куда идёт (продолжение — общая модель)
112-25-PPR	25	16495	16660	+4,772	азот на гребёнку защиты R-101: к коллектору азота 449 — граница с трассой…
114-50-S	50	17952	17345	+5,664	сдувки R-101 и E-102 на газоочистку: к коллектору 901 — граница с трассой
117-50-PPR	50	15490	11182	+0,213	подача воды охлаждения: из тройника магистрали 707 (у пола) — граница с т…
118-50-PPR	50	15630	11802	+0,214	возврат воды охлаждения: в тройник магистрали 711 (у пола) — граница с тр…
123-25-PPR	25	15212	8728	+4,400	азот: в тройник DN25 коллектора азота 449 (+4,400) — граница с трассой аз…
125-50-PPR	50	14000	16378	+2,152	подача воды в рубашку: от термостата X-104 (техзона; магистраль +2,900, о…
126-50-PPR	50	14000	16378	+1,952	возврат воды из рубашки: к термостату X-104 (техзона; +1,952, подъём на м…
127-50-PPR	50	15719	10633	+5,060	вакуум: из тройника DN100×50 коллектора вакуума 618 (Y 10 790) — граница …

Изм.	Лист	№ докум.	Подп.	Дата	ОПУ.ОБ.R-101.М.14			
Разраб.					**Реактор 3 м³ 316L (R-101):** ведомость точек стыка и границ узла	Лит.	Масса	Масштаб
Пров.						П	—	б/м
Т.контр.						Лист 14		Листов 16
Н.контр.					Опытно-промышленный участок	**Опытно-промышленный участок**		
Утв.								

ВЕДОМОСТЬ АРМАТУРЫ И КИП

Тег	Наименование	Линия	X, мм	Y, мм	Отм., м
LIRA-103	LIRA-103 (LT-103) — уровнемер радарный, 4–20 мА HART, Ex ia/db, антенна TFM-PTFE, шкала 0…1400 мм (уровень ЭХГ; сигнализация 1350, блокировка 1400), …		15259	9021	+3,28
PIR-101	PIR-101 (PT-101) — датчик избыточного давления, шкала −0,1…0,5 кгс/см², 0Ex ia, 4–20 мА HART, мембрана 316L, присоединение M20×1,5		14870	14010	+4,34
SP-101	SP-101 поз. 2: основание монтажное DN100 PN25 (316L) с патрубком DN25 и погружной трубой		15990	13710	+4,02
TIRA-101	TIRA-101 (TT-101) — термопреобразователь с трубной защитной арматурой 12Х18Н10Т ø10, погружная часть 2030 мм, 0Ex ia, шкала 0…38 °C, M27×2 (в гильзе …		15990	14310	+4,09
TIRA-102	TIRA-102 (TT-102) — термопреобразователь с трубной защитной арматурой 12Х18Н10Т ø10, погружная часть 150 мм, 0Ex ia, шкала 0…40 °C (сигнализация 40 °…		15217	13624	+4,49
AP-1	Еврокуб IBC 1000 л (104) — конденсат Х-103 (ЭХГ, вода, толуол) → на регенерацию в Х-600: кран нижний DN50 (дисковый затвор PP/EPDM) с кулачковой полу…	104-50-S			
AP-2	R-101 B: клапан донного слива F41W DN100 PN25 (поставка), корпус CF3M (316L), крышка на 4 шпильках, сальник графит, бугель, шток, маховик Ø250; выход…	105-50-S	15470	13904	+1,30
AP-3	Еврокуб IBC 1000 л (105) — продукт / водная фаза / промывные воды R-101: кран нижний DN50 (дисковый затвор PP/EPDM) с кулачковой полумуфтой 2″ и загл…	105-50-S			
AP-4	PCV ГЗ-101 — редуктор давления азота с манометром, G1/2, AISI 316	112-25-PPR	14848	12966	+3,96
AP-5	шпунт-аппарат (регулятор-ограничитель давления) K25 с манометром Ø63, AISI 316L/PTFE ГЗ-101	ГЗ-101	15491	12966	+4,85
ВН-1	клапан запорный (вентиль) фланцевый DN50 PN25 AISI 316L, сильфонное уплотнение штока (EN 558 сер.1) — 107: у реактора (по схеме поставщика)	107-50-SS	15010	12858	+4,30
ВН-2	клапан запорный (вентиль) фланцевый DN25 PN25 AISI 316L, сильфонное уплотнение штока (EN 558 сер.1) — 108: дренаж гидрозатвора	108-25-SS	15010	10927	+3,69
ВН-3	вентиль запорно-регулирующий PPRF/SV-2(X)-63 PN20 (раструбная сварка) — 117 (регулирование расхода воды на E-102)	117-50-PPR	16110	11000	+1,25
КТ-1	кран шаровой трёхходовой фланцевый DN100 PN25 AISI 316L/PTFE, L-проход, редуктор с маховиком — 102: в сборник Х-103 / флегма 107 в реактор (по схеме …	102-100-SS	15010	9188	+4,42
КШ-1	кран шаровой фланцевый DN25 PN25 AISI 316L/PTFE, полнопроходной (EN 558 сер.27) — 103: дренаж N7 (под балками П1)	103-25-SS	15193	12599	+5,06
КШ-2	кран шаровой фланцевый DN25 PN25 AISI 316L/PTFE, полнопроходной (EN 558 сер.27) — 103: дренаж N8 (под балками П1)	103-25-SS	15193	9945	+5,06
КШ-3	кран шаровой фланцевый ABRA-BV41-50 AISI 316 (CF8M), PN40, класс герметичности A — 104 (слив конденсата Х-103 в еврокуб: кран DN50)	104-50-S	15280	9320	+1,32
КШ-4	кран шаровой фланцевый ABRA-BV41-50 AISI 316 (CF8M), PN40, класс герметичности A — 114 (сдувка E-102 N9)	114-50-S	15659	12740	+6,92
КШ-5	кран шаровой полипропиленовый PPR-20 PN20 (раструбная сварка) — воздушник 117	117-50-PPR	15924	10236	+4,73
КШ-6	кран шаровой полипропиленовый PPR-20 PN20 (раструбная сварка) — манометр 117 (кран 20×G1/2)	117-50-PPR	15010	10376	+4,71
КШ-7	кран шаровой полипропиленовый PPR-63 PN20 (раструбная сварка) — 117 (кран у E-102 N3)	117-50-PPR	15010	10219	+4,90
КШ-8	кран шаровой полипропиленовый PPR-20 PN20 (раструбная сварка) — воздушник 118	118-50-PPR	15495	12414	+7,13
КШ-9	кран шаровой полипропиленовый PPR-63 PN20 (раструбная сварка) — 118 (кран у E-102 N4)	118-50-PPR	15010	12253	+6,60
КШ-10	кран шаровой фланцевый DN25 PN16 AISI 316L/PTFE, полнопроходной (EN 558 сер.27) — 123 (азот на Х-103: кран DN25)	123-25-PPR	15212	9610	+3,69
КШ-11	кран шаровой полипропиленовый PPR-63 PN20 (раструбная сварка) — 125 (кран DN50 на опуске подачи)	125-50-PPR	15470	15185	+1,96
КШ-12	кран шаровой полипропиленовый PPR-25 PN20 (раструбная сварка) — дренаж 125	125-50-PPR	15621	15185	+1,76
КШ-13	кран шаровой полипропиленовый PPR-63 PN20 (раструбная сварка) — 126 (кран DN50 на подъёме возврата, трасса теплоносителя)	126-50-PPR	15470	16450	+2,68
КШ-14	кран шаровой полипропиленовый PPR-25 PN20 (раструбная сварка) — дренаж 126	126-50-PPR	14870	15185	+2,71
КШ-15	кран шаровой полипропиленовый PPR-63 PN20 (раструбная сварка) — вакуум к E-102 (кран на отводе от коллектора 618, над настилом П1 +5.420)	127-50-PPR	15719	10508	+5,62
КШ-16	кран шаровой фланцевый DN25 PN10 AISI 316L/PTFE, полнопроходной (EN 558 сер.27) — E-102 N5	E-102 N5	15160	12310	+5,51
КШ-17	кран шаровой фланцевый DN25 PN10 AISI 316L/PTFE, полнопроходной (EN 558 сер.27) — E-102 N6	E-102 N6	15010	10141	+6,39
КШК-1	кран шаровой санитарный K25 с клампами, AISI 316L/PTFE, рукоятка ГЗ-101 — ввод азота (азотная подушка)	112-25-PPR	14848	12966	+4,41
КШК-2	кран шаровой санитарный K25 с клампами, AISI 316L/PTFE, рукоятка ГЗ-101 — перед шунт-аппаратом	ГЗ-101	15538	12966	+4,63
КШК-3	кран шаровой санитарный K25 с клампами, AISI 316L/PTFE, рукоятка ГЗ-101 — перед обратным клапаном аварийного сброса (закрыт только на время вакуумиро…	ГЗ-101	15308	12966	+4,63
КШК-4	кран шаровой санитарный K25 с клампами, AISI 316L/PTFE, рукоятка ГЗ-101 — перед мановакуумметром	ГЗ-101	15078	12966	+4,63
КШК-5	кран шаровой санитарный K25 с клампами, AISI 316L/PTFE, рукоятка ГЗ-101 — сброс на атмосферу	ГЗ-101	14678	12966	+4,52
КШМ-1	кран шаровой муфтовый DN20 (G3/4) AISI 316/PTFE, PN40 — g (воздушник рубашки)	рубашка g	15966	14870	+3,03
КШМ-2	кран шаровой муфтовый DN15 (G1/2) AISI 316/PTFE, PN40 — k (дренаж рубашки)	рубашка k	15278	13484	+1,56
ОК-1	клапан обратный подъёмный фланцевый DN25 PN16 AISI 316L (EN 558 сер.1) — 123 (азот: обратный клапан DN25, поток — к Х-103)	123-25-PPR	15212	9610	+3,84
ОК-2	клапан обратный пружинный K25 с клампами (AISI 316L / PTFE), поток → ГЗ-101 — аварийный сброс	ГЗ-101	15308	12966	+4,73

					ОПУ.ОБ.R-101.М.15
Изм.	Лист	№ докум.	Подп.	Дата	
Разраб.					**Реактор 3 м³ 316L (R-101):** ведомость арматуры и кип
Пров.					
Т.контр.					
					Лит. П | Масса — | Масштаб б/м
Н.контр.					Лист 15 | Листов 16
Утв.					
					Опытно-промышленный участок
					Опытно-промышленный участок

УСЛОВНЫЕ ОБОЗНАЧЕНИЯ

Потоки (цвет линии)

- сырьё и загрузка
- пары (реактор → конденсатор)
- конденсат и флегма
- продукт, слив реактора
- дренажи
- аварийный сброс
- вакуум
- азот
- сдувки и дыхание
- вода охлаждающая (оборотная)
- теплоноситель — вода от термостата
- рукав (цвет — по потоку)
- зонт местного отсоса (вентиляция) → магистраль вытяжки В1
- лиана FM-200 — местный отсос на поворотной балке
- очертания аппаратов — проекция 3D-модели
- внутренние устройства (мешалки, вал, гильза, перегородки)
- 12 — номер соединения (ведомость соединений)

Символы (ГОСТ 2.785, ГОСТ 21.206)

- кран, вентиль, клапан запорный
- клапан обратный (по потоку)
- конец линии: штуцер, точка стыка, граница, заглушка
- рабочий уровень в аппарате

Сокращение	Что это
КШ	кран шаровой фланцевый
КШК	кран шаровой санитарный (кламп К64)
КШМ	кран шаровой муфтовый
ОК	клапан обратный
ВН	вентиль (клапан запорный)
КТ	кран трёхходовой
КД	клапан донный F41
КИ	клапан игольчатый
PIR, TIRA, LIRA	датчики давления, температуры, уровня
SP	пробоотборник верхний GHFDQY-F16RL (поставка)
N1…N10, T, B, M, L1…L4	штуцеры аппаратов (по чертежам поставщика)

Изм.	Лист	№ докум.	Подп.	Дата	ОПУ.ОБ.R-101.М.16			
Разраб.					Условные обозначения монтажных листов	Лит.	Масса	Масштаб
Пров.						П	—	б/м
Т.контр.						Лист 16		Листов 16
Н.контр.					Опытно-промышленный участок	Опытно-промышленный участок		
Утв.								