

МЕРНИКИ ЗАГРУЗКИ V-401…V-409 НА ПЛОЩАДКЕ +6.400 — УСТАНОВКА В СБОРЕ (ПЛАН И ВИД С ЮГА)

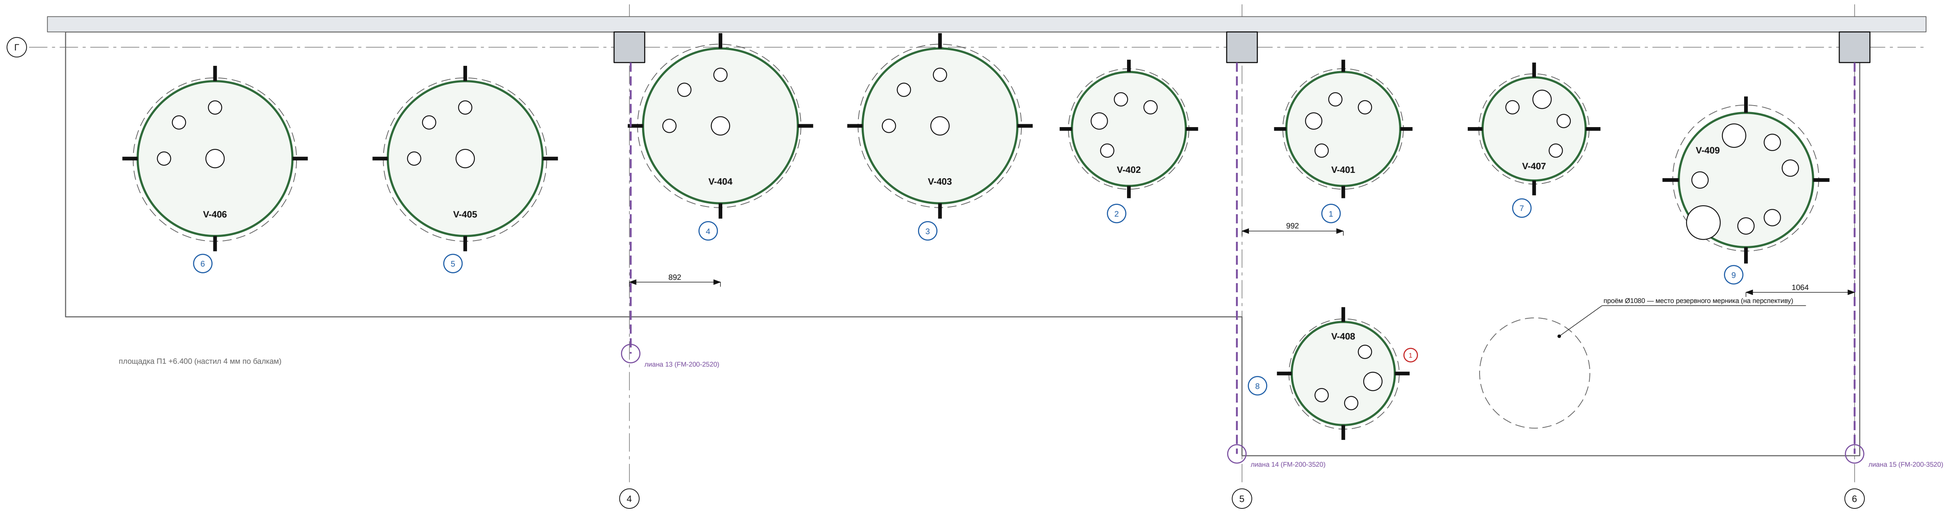

Поз.	Обозначение	Наименование	Кол.	Примечание
1	V-401	мерник 1,25 м³ с рубашкой (F1000L), резерв	1	лапы на настиле +6.400
2	V-402	мерник 1,25 м³ с рубашкой (F1000L), резерв; рубашка — вода	1	лапы на настиле +6.400
3	V-403	мерник 3 м³ (F3000L), резерв	1	лапы на настиле +6.400
4	V-404	мерник 3 м³ (F3000L), резерв	1	лапы на настиле +6.400
5	V-405	мерник 3 м³ (F3000L), резерв	1	лапы на настиле +6.400
6	V-406	мерник воды обессоленной 3 м³ (F3000L)	1	лапы на настиле +6.400
7	V-407	мерник 1,25 м³ (F1000L), резерв	1	лапы на настиле +6.400
8	V-408	мерник 1,25 м³ (F1000L), резерв	1	лапы на настиле +6.400
9	V-409	ёмкость 1,21 м³ с рубашкой и мешалкой (K1000L); резерв	1	лапы на настиле +6.400
10	лианы 13–15	местный отсос FM-200 с рукавом KUA-200 (ОВ)	3	на колоннах ряда Г

ВИД С ЮГА (площадка +6.400 в разрезе, стена ряда Г — за аппаратами)

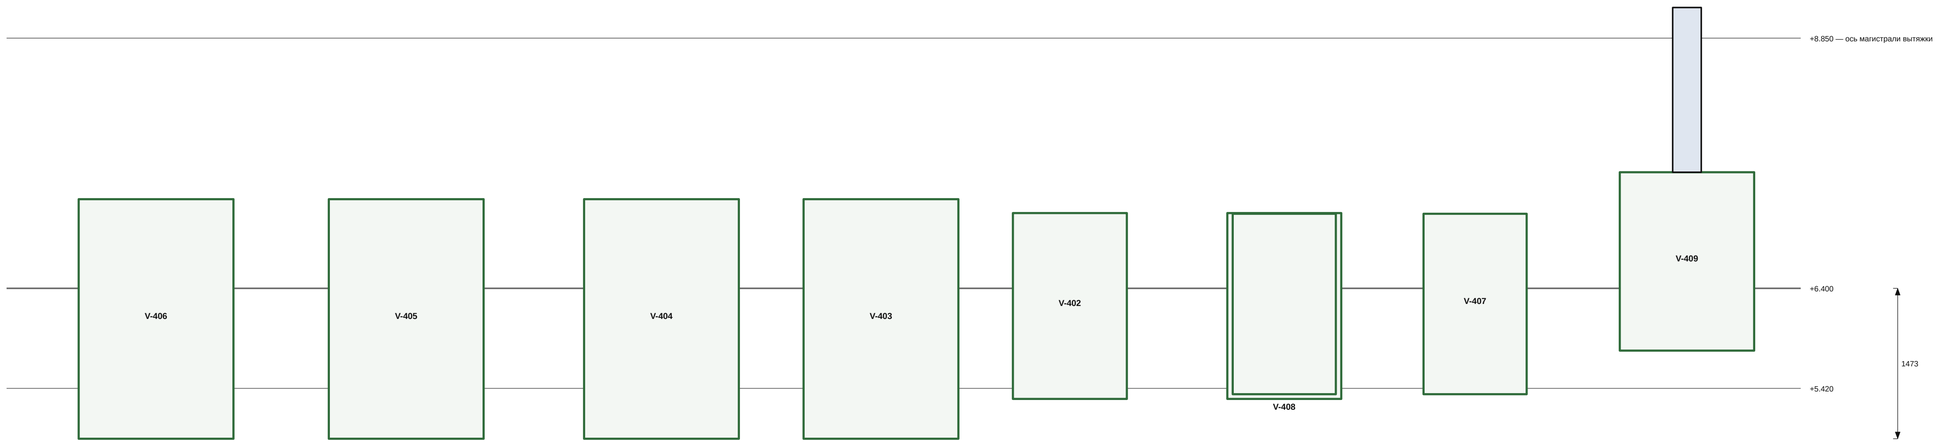

1. Мерники пока не в работе: штуцеры закрыты заглушками фланцевыми с прокладкой PTFE и крепежом (лист 2).
2. Мерники висят в проёмах настила +6.400; лапы — на настиле, болты M20. Проёмы — по металлоконструкциям площадки.
3. Под полосой мерников настила +5.420 нет; под V-408 — проём в настиле +5.420 (уточнить, кружок ⑤).
4. Отметки — от чистого пола 0.000. Размеры — мм.

Изм.	Лист	№ докум.	Подп.	Дата
Разраб.				
Пров.				
Т.контр.				
Н.контр.				
Утв.				

ОПУ.ОБ.МЕРН.М.01

Мерники загрузки V-401…V-409 на площадке +6.400. Установка в сборе

Лит.	Масса	Масштаб
П	—	1:30

Лист 1 — Листов 4

Мерники загрузки V-401…V-409 (узел 10)

Опытно-промышленный участок

ШТУЦЕРЫ МЕРНИКОВ — ЗАГЛУШКИ (МЕРНИКИ НЕ В РАБОТЕ) И НАЗНАЧЕНИЕ НА БУДУЩЕЕ

Мерник	Штуцер	DN	PN	Отм. торца	Сейчас	На будущее
V-401	B	50	PN10	+5.217	заглушка	резерв
V-401	L1	32	PN10	+6.620	заглушка	резерв
V-401	L2	32	PN10	+6.620	заглушка	резерв
V-401	L3	32	PN10	+5.252	заглушка	резерв
V-401	L4	32	PN10	+5.252	заглушка	резерв
V-401	N1	50	PN10	+7.207	заглушка	резерв
V-401	N2	80	PN10	+7.207	заглушка	резерв
V-401	N3	50	PN10	+7.207	заглушка	азот 425
V-401	N4	50	PN10	+7.207	заглушка	дыхание 423
V-402	B	50	PN10	+5.217	заглушка	резерв
V-402	L1	32	PN10	+6.620	заглушка	вода из рубашки 150
V-402	L2	32	PN10	+6.620	заглушка	вода из рубашки 150
V-402	L3	32	PN10	+5.252	заглушка	вода в рубашку 186
V-402	L4	32	PN10	+5.252	заглушка	вода в рубашку 186
V-402	N1	50	PN10	+7.207	заглушка	резерв
V-402	N2	80	PN10	+7.207	заглушка	резерв
V-402	N3	50	PN10	+7.207	заглушка	азот 426
V-402	N4	50	PN10	+7.207	заглушка	дыхание 427
V-403	B	65	PN10	+4.827	заглушка	резерв
V-403	N1	100	PN10	+7.393	заглушка	резерв
V-403	N2	50	PN10	+7.298	заглушка	резерв
V-403	N3	50	PN10	+7.298	заглушка	дыхание 429
V-403	N4	50	PN10	+7.298	заглушка	азот 428
V-404	B	65	PN10	+4.827	заглушка	резерв
V-404	N1	100	PN10	+7.393	заглушка	резерв
V-404	N2	50	PN10	+7.298	заглушка	резерв
V-404	N3	50	PN10	+7.298	заглушка	дыхание 432
V-404	N4	50	PN10	+7.298	заглушка	азот 431
V-405	B	65	PN10	+4.827	заглушка	резерв
V-405	N1	100	PN10	+7.393	заглушка	резерв

Мерник	Штуцер	DN	PN	Отм. торца	Сейчас	На будущее
V-405	N2	50	PN10	+7.298	заглушка	резерв
V-405	N3	50	PN10	+7.298	заглушка	дыхание 435
V-405	N4	50	PN10	+7.298	заглушка	азот 434
V-406	B	65	PN10	+4.827	заглушка	выдача воды 419
V-406	N1	100	PN10	+7.393	заглушка	резерв
V-406	N2	50	PN10	+7.298	заглушка	резерв
V-406	N3	50	PN10	+7.298	заглушка	воздушник 436
V-406	N4	50	PN10	+7.298	заглушка	вода обессоленная 437
V-407	B	50	PN10	+5.270	заглушка	резерв
V-407	N1	50	PN10	+7.200	заглушка	резерв
V-407	N2	100	PN10	+7.200	заглушка	резерв
V-407	N3	50	PN10	+7.200	заглушка	азот 438
V-407	N4	50	PN10	+7.200	заглушка	дыхание 439
V-408	B	50	PN10	+5.270	заглушка	резерв
V-408	N1	50	PN10	+7.200	заглушка	резерв
V-408	N2	100	PN10	+7.200	заглушка	резерв
V-408	N3	50	PN10	+7.200	заглушка	азот 440
V-408	N4	50	PN10	+7.200	заглушка	дыхание 441
V-409	B	100	PN25	+5.677	заглушка	резерв
V-409	H	250	PN25	+7.561	заглушка	резерв
V-409	L1	40	PN10	+6.670	заглушка	резерв
V-409	L2	40	PN10	+6.670	заглушка	резерв
V-409	L3	40	PN10	+5.755	заглушка	резерв
V-409	L4	40	PN10	+5.755	заглушка	резерв
V-409	N1	150	PN25	+7.586	заглушка	резерв
V-409	N2	80	PN25	+7.586	заглушка	дыхание 444
V-409	N3	80	PN25	+7.586	заглушка	резерв
V-409	N4	80	PN25	+7.586	заглушка	азот 443
V-409	N5	80	PN25	+7.586	заглушка	резерв
V-409	T	80	PN25	+7.586	заглушка	резерв

Изм.	Лист	№ докум.	Подп.	Дата	ОПУ.ОБ.МЕРН.М.02			
Разраб.					**Штуцеры мерников: заглушки и** назначение на будущее	Лит.	Масса	Масштаб
Пров.						П	—	б/м
Т.контр.						Лист 2		Листов 4
Н.контр.					Мерники загрузки V-401…V-409 (узел 10)	Опытно-промышленный участок		
Утв.								

ВЕДОМОСТЬ СОЕДИНЕНИЙ (ЗАГЛУШКИ ФЛАНЦЕВЫЕ, ЛАПЫ, ЛИАНЫ)

№	Соединение	Кол.	Шпильки (на 1)	Прокладка
1	заглушка фланцевая DN32 PN10 на штуцере	8	4 шт. M16×84 с гайками (A2-70)	PTFE DN32
2	заглушка фланцевая DN40 PN16 на штуцере	4	4 шт. M16×84 с гайками (A2-70)	PTFE DN40
3	заглушка фланцевая DN50 PN10 на штуцере	28	4 шт. M16×84 с гайками (A2-70)	PTFE DN50
4	заглушка фланцевая DN65 PN10 на штуцере	4	8 шт. M16×84 с гайками (A2-70)	PTFE DN65
5	заглушка фланцевая DN80 PN10 на штуцере	2	8 шт. M16×88 с гайками (A2-70)	PTFE DN80
6	заглушка фланцевая DN80 PN25 на штуцере	5	8 шт. M16×96 с гайками (A2-70)	PTFE DN80
7	заглушка фланцевая DN100 PN10 на штуцере	6	8 шт. M16×88 с гайками (A2-70)	PTFE DN100
8	заглушка фланцевая DN100 PN25 на штуцере	1	8 шт. M20×106 с гайками (A2-70)	PTFE DN100
9	заглушка фланцевая DN150 PN25 на штуцере	1	8 шт. M24×124 с гайками (A2-70)	PTFE DN150
10	лапа опорная — настил +6.400	36	1 болт M20 с шайбой и гайкой	—
11	лиана FM-200 — колонна К1 (плита 3)	3	4 болта M16 с гайками	—

Изм.	Лист	№ докум.	Подп.	Дата	ОПУ.ОБ.МЕРН.М.03		
Разраб.					**Ведомость соединений: заглушки** штуцеров и лапы	Лит.	Масса	Масштаб
Пров.						П	—	б/м
Т.контр.						Лист 3		Листов 4
Н.контр.					Мерники загрузки V-401…V-409 (узел 10)	Опытно-промышленный участок		
Утв.								

УСЛОВНЫЕ ОБОЗНАЧЕНИЯ



мерник (корпус в плане), позиция — в кружке



проём в настиле +6.400



штуцер крышки на заглушке фланцевой

лапа опорная (плита на настиле, болт М20)



лиана FM-200: балка в рабочем положении, воронка рукава KUA-200



номер позиции по перечню



открытый вопрос (README узла)

					ОПУ.ОБ.МЕРН.М.04	
Изм.	Лист	№ докум.	Подп.	Дата		
Разраб.					**Условные обозначения**	Лит. П / Масса — / Масштаб б/м
Пров.						
Т.контр.						Лист 4 / Листов 4
Н.контр.					Мерники загрузки V-401…V-409 (узел 10)	**Опытно-промышленный участок**
Утв.						