
УСТАНОВКА В СБОРЕ — МОНТАЖНАЯ СХЕМА (аппараты М 1:16, отметки — по 3D-модели). Номера соединений — как в ведомости соединений

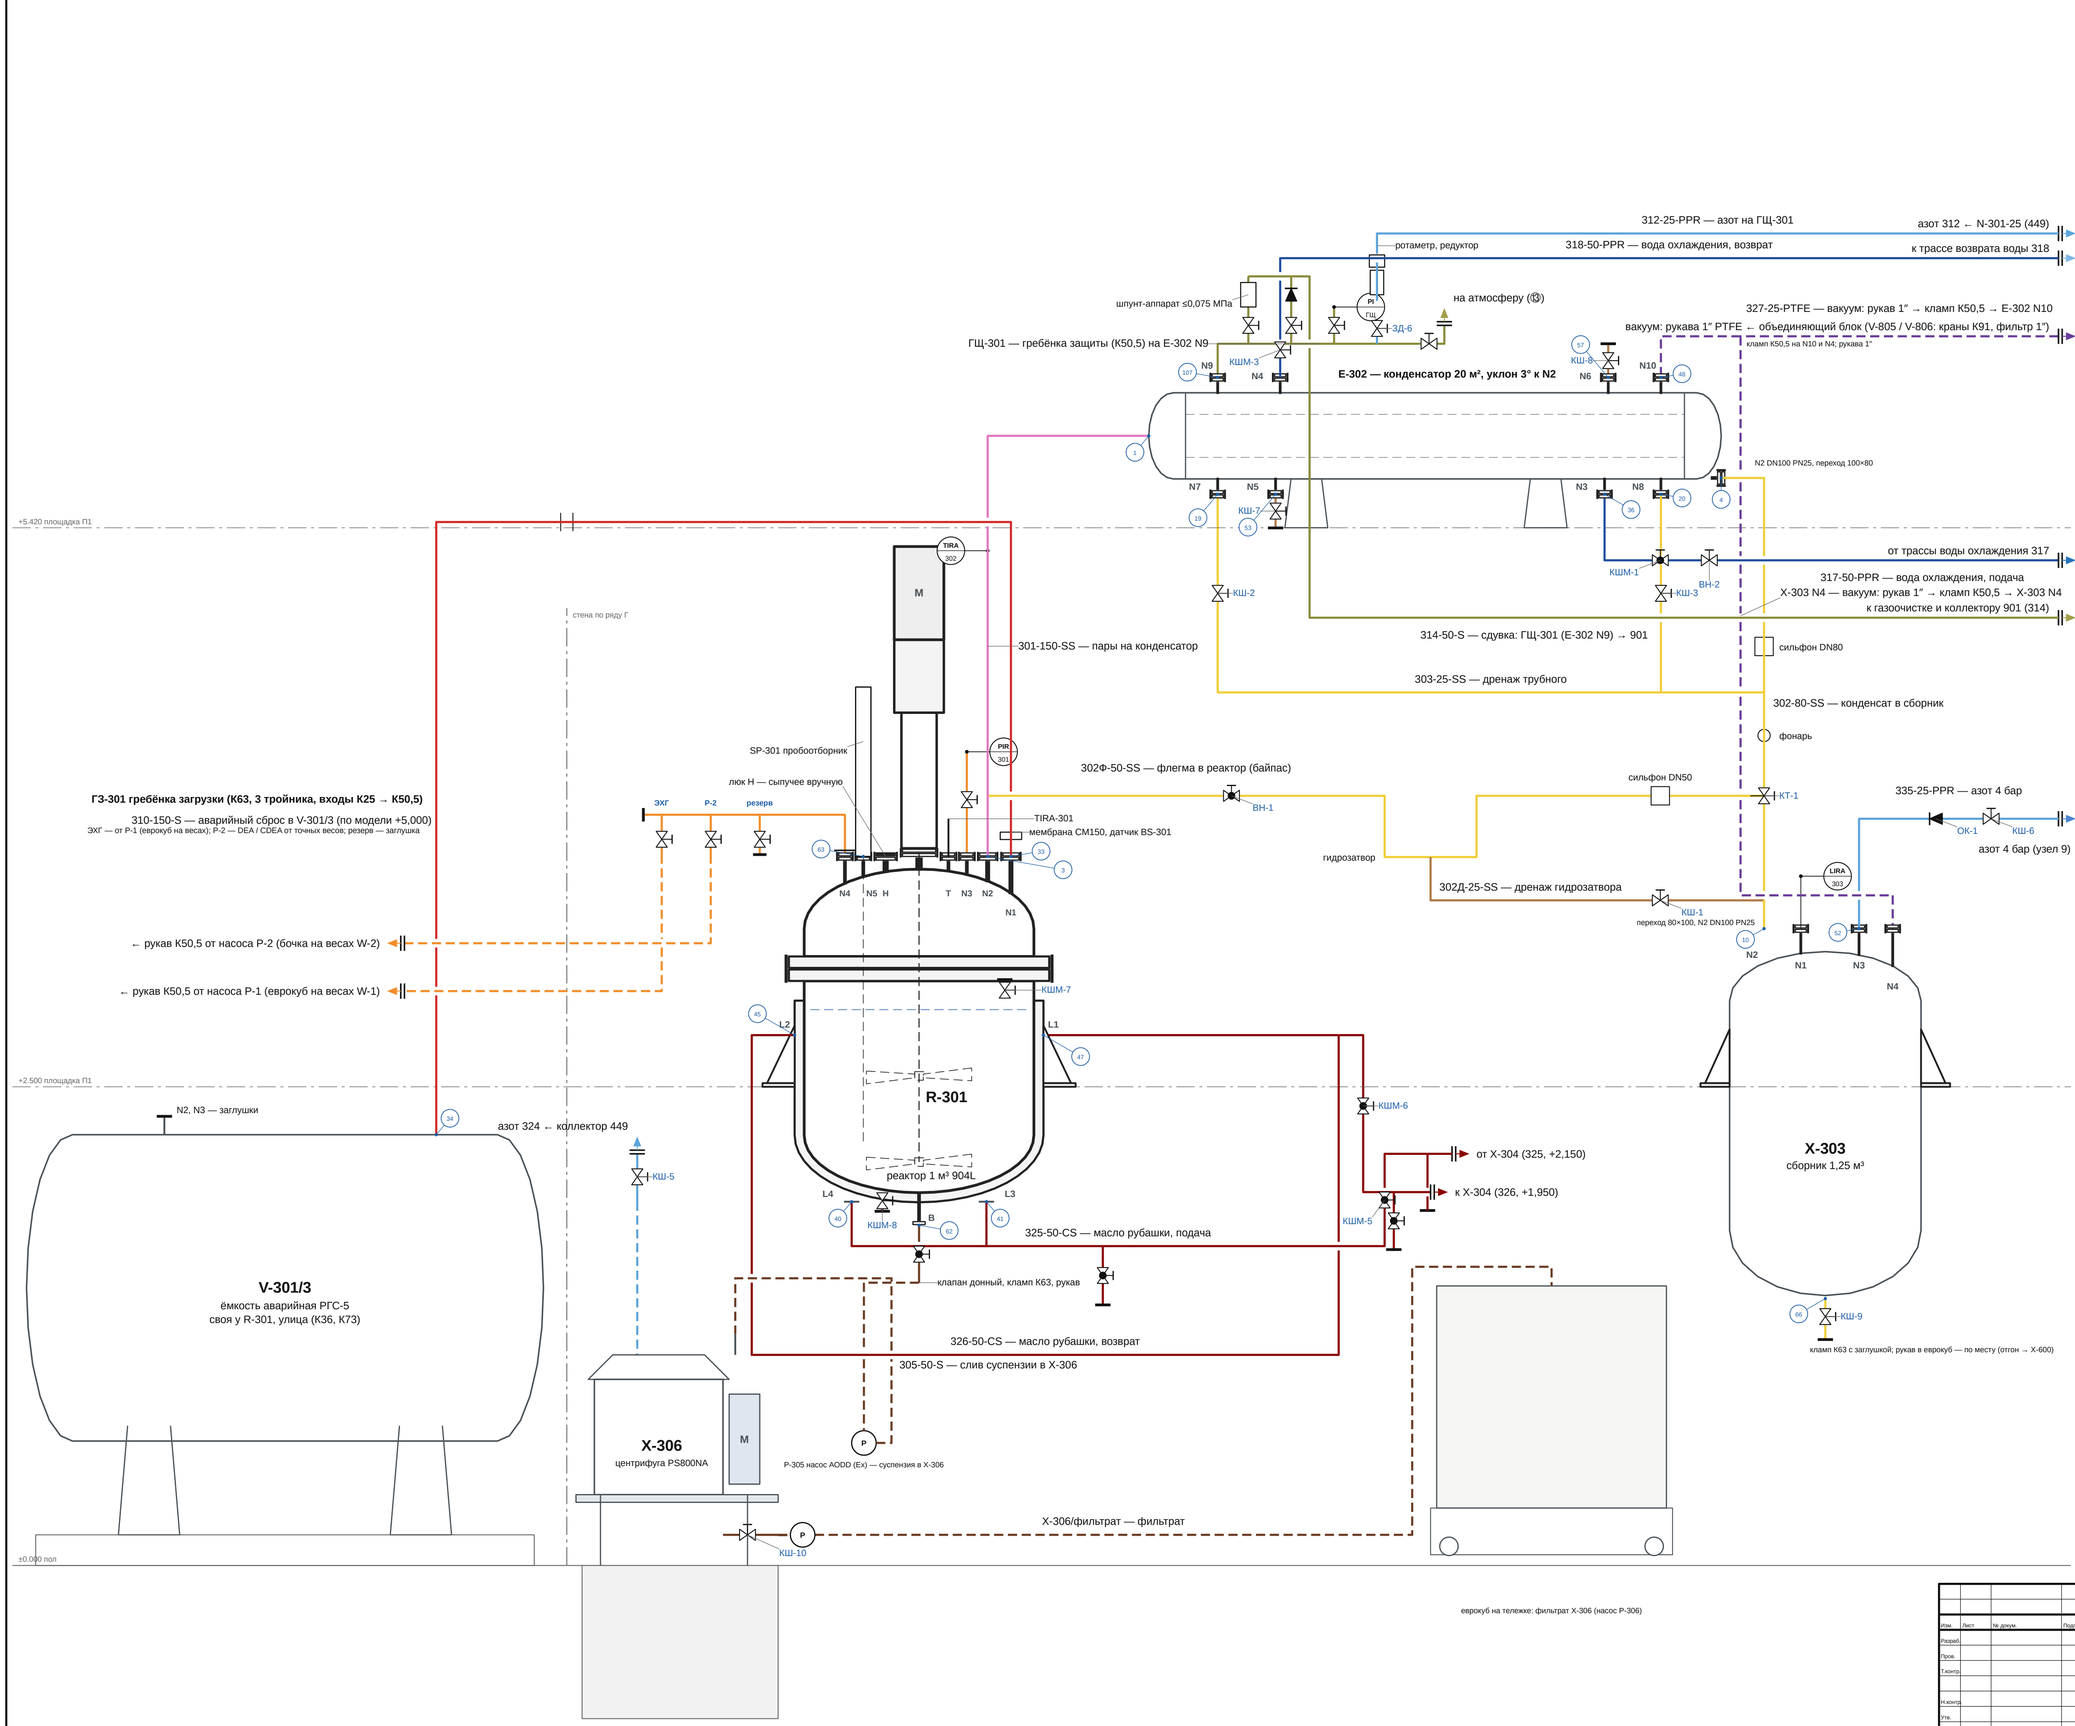

ПЕРЕЧЕНЬ ПОЗИЦИЙ

Поз.	Наименование	Кол.
R-301	Реактор 1 м³ 904L с рубашкой и мешалкой	1
E-302	Конденсатор паров 20 м²	1
X-303	Сборник конденсата 1,25 м³	1
V-301/3	Ёмкость аварийная РГС-5 R-301 (улица)	1
X-306	Центрифуга PS800NA (фундамент Фо1)	1
ГЗ-301	Гребёнка загрузки на N4: K63, 3 тройника, входы K50,5	1
ГЩ-301	Гребёнка защиты на E-302 N9, K50,5	1
SP-301	Пробоотборник верхний GHFDQY-PFA16RL на N5	1
P-306	Насос мембранный (Ex) — фильтрат X-306	1
P-305	Насос мембранный (Ex) — суспензия R-301 → X-306	1
IBC	Еврокуб 1000 л на тележке (фильтрат, оттон)	2
—	Местные отсосы: лиана FM-200 №2, зонт I, бортовой A	3

Потоки (цвет линии)

- сырьё и загрузка
- пары (реактор → конденсатор)
- конденсат и флегма
- продукт, слив реактора
- дренажи
- аварийный сброс
- вакуум
- азот
- сжатый воздух
- сдувки и дыхание
- вода охлаждающая (оборотная)
- теплоноситель — масло
- рукав (цвет — по потоку)
- очертания аппаратов — проекция 3D-модели
- внутренние устройства (мешалки, вал, гильза, перегородки)
- (12) номер соединения (ведомость соединений)


Примечания


1. Аппараты — М 1:16, отметки — по 3D-модели; положение в плане — условно (трассы — листы 3–9).
2. Обвязка — по трассам линий и чертежам поставщика; гребёнки — на клампах K50,5 / K63.
3. Цвет линии — поток; DN и материал — в номере.
4. Номер в кружке — соединение (ведомость); теги арматуры — ведомость арматуры и КИП.
5. Граница узла — двойной штрих и стрелка.
6. 310 на схеме — над приводом (по модели +5,000).

? место ресиверов вакуума (①); дисковые затворы на клампах (⑩)
? уставки ГЩ-301 (⑦); V-301/3 N2, N3 (⑫)

Изм.	Лист	№ докум.	Подп.	Дата	**ОПУ.ОБ.R-301.M.01**
Разраб.					**Реактор 1 м³ 904L (R-301):** установка в сборе
Пров.					Лит. П; Масса —; Масштаб б/м
Т.контр.					Лист 1; Листов 16
Н.контр.					**Опытно-промышленный участок**
Утв.					Опытно-промышленный участок

РЕАКТОР 1 М³ 904L (R-301) — ВИД С ЗАПАДА (с внутренними устройствами) И КРЫШКА СВЕРХУ М 1:25

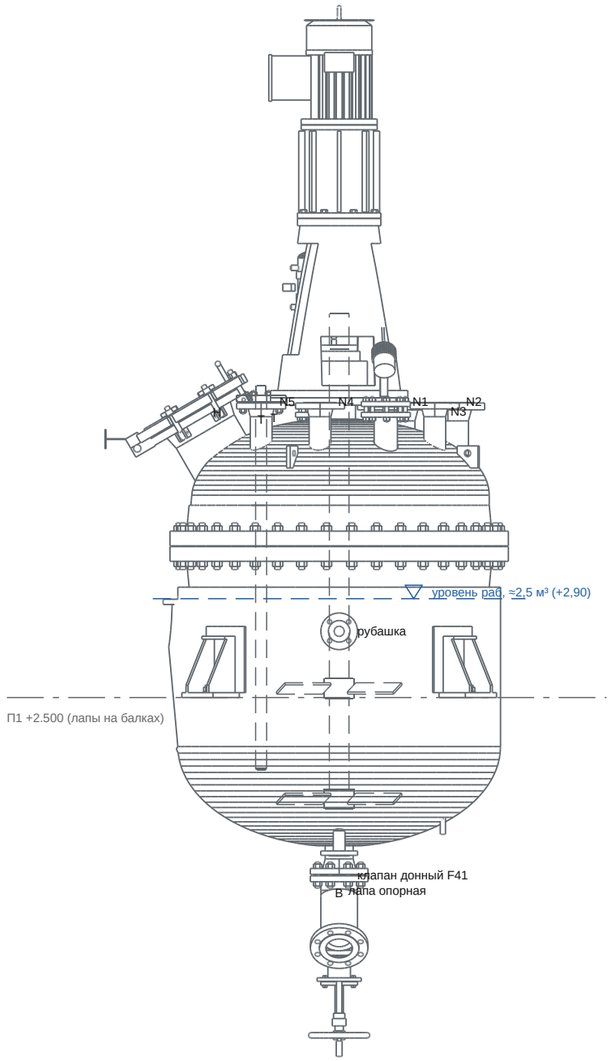

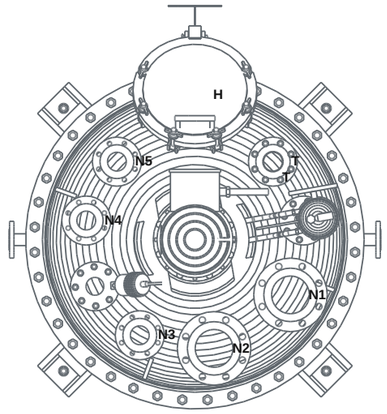

КРЫШКА СВЕРХУ (север — вверх); штуцеры — по чертежу поставщика, назначение — по схеме узла

ТАБЛИЦА ШТУЦЕРОВ R-301


Штуцер	Исполнение	Угол	Назначение (что присоединено)	Отм., м
B			штуцер слива PN25 DN100 (под донный клапан F41Y-25 904L)	+1,777
G			штуцер вала Ø133×6 с опорным фланцем привода Ø560	
H			крышка люка DN250 быстрооткрываемая на петле: откидные болты M20 с ба…	
H			люк DN250 PN25 (HG/T 21530): горловина Ø273×8 с фланцем; крышка с быс…	+3,661
N1	WN150-25	120°	тройник: мембрана CM150 → аварийный сброс 310-150-S, сдувка 314-50-S	+3,703
N2	WN150-25	170°	пары на E-302 (301-150-SS)	+3,703
N3	WN80-25	210°	датчик давления PT-301 (PIR-301): фланец переходной 80/25, кран DN25	+3,703
N4	WN80-25	280°	загрузка жидкостей (K73): переходник фланец-кламп K63, гребёнка загру…	+3,703
N5	WN80-25	315°	пробоотборник верхний SP-301 GHFDQY-PFA16RL (воронка 309 убрана)	+3,703
T	WN80-25	45°	гильза термометра TT-301 (TIRA-301)	+3,703

Рабочий уровень (принято, ?) — отметка +2,90 по 3D-модели (днище 2:1 + цилиндр Ø1200). Отметки — по 3D-модели.

Изм.	Лист	№ докум.	Подп.	Дата	**ОПУ.ОБ.R-301.М.02**		
Разраб.					**Реактор 1 м³ 904L (R-301): лист аппарата**	Лит.	Масса	Масштаб
Пров.						П	—	1:25
Т.контр.						Лист 2		Листов 16
Н.контр.					Опытно-промышленный участок	**Опытно-промышленный участок**		
Утв.								

Пары и конденсат по схеме поставщика: шлемовая 301, спуск 302, дренажи 303, байпас флегмы 302Ф, дренаж 302Д

Аппараты целиком, М 1:15; отметки — по 3D-модели; номера соединений — как в ведомости соединений

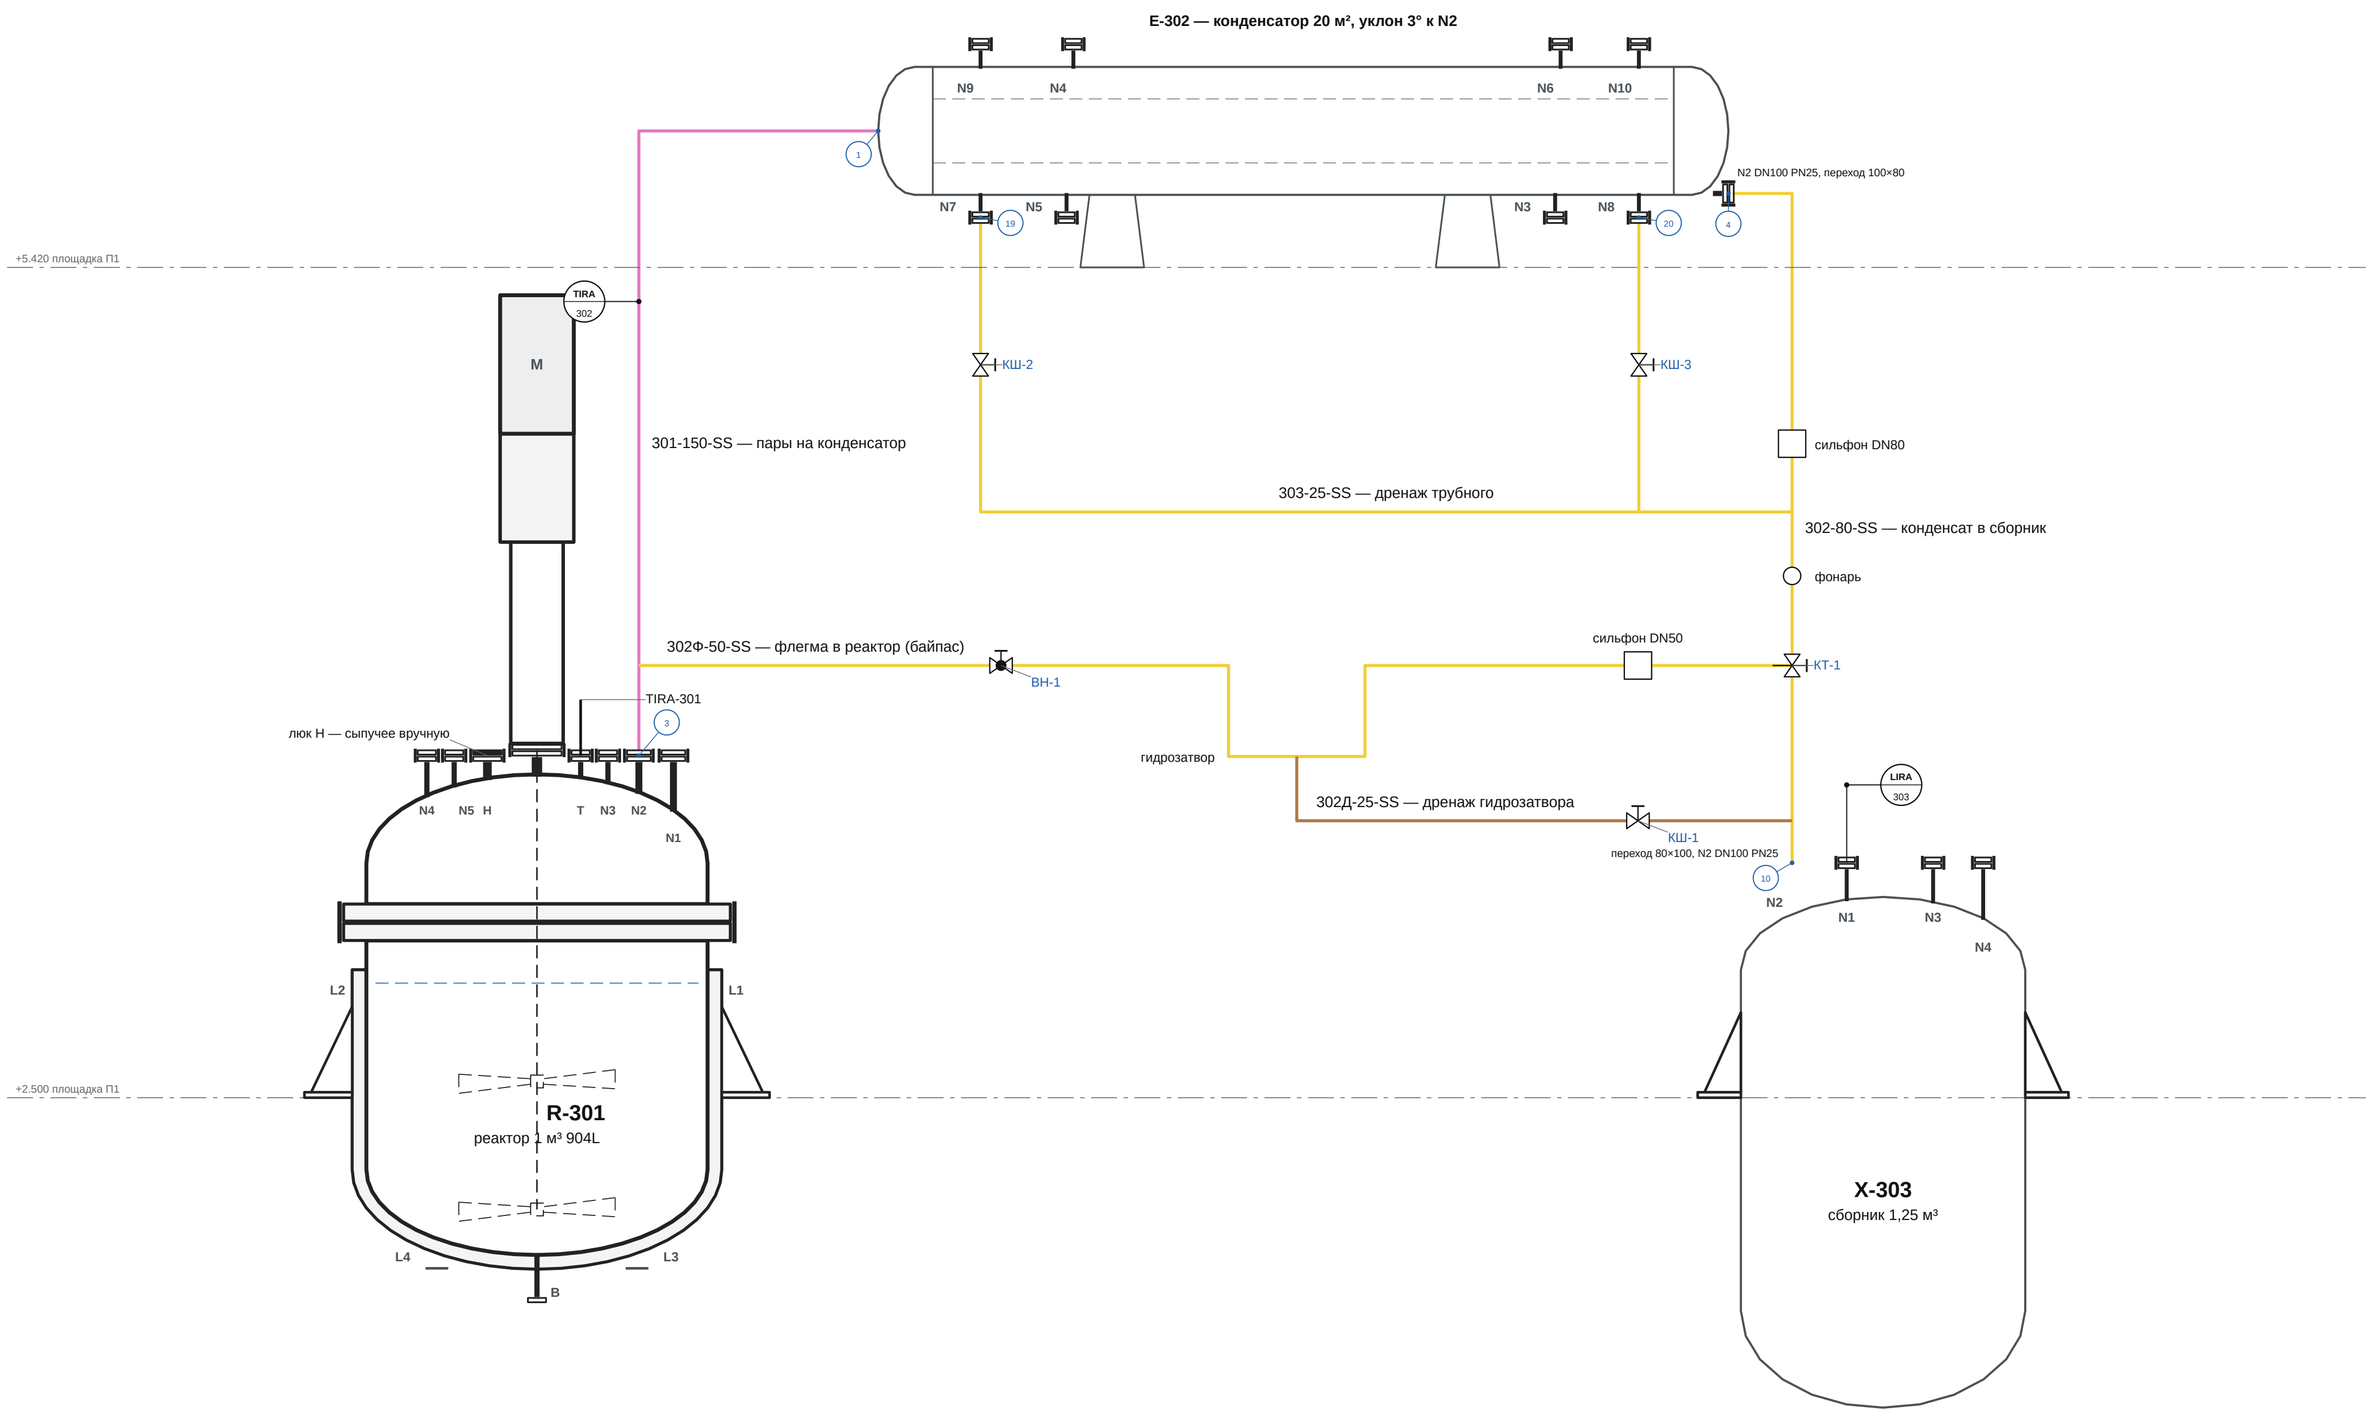

Изм.	Лист	№ докум.	Подп.	Дата
Разраб.				
Пров.				
Т.контр.				
Н.контр.				
Утв.				

ОПУ.ОБ.R-301.М.03

Реактор 1 м³ 904L (R-301): пары и конденсат (схема поставщика)

Лит.	Масса	Масштаб
П	—	б/м


Лист 3 | Листов 16

Опытно-промышленный участок

Опытно-промышленный участок

Крышка реактора (R-301): N4 — гребёнка загрузки ГЗ-301 (К63, входы К25, рукав от Р-1); N1 — гребёнка защиты ГЩ-301 (вместо КДЗТ), азот 312; N3 — PIR-301; N5 — SP-301; H — люк

Аппараты целиком, М 1:20; отметки — по 3D-модели; номера соединений — как в ведомости соединений

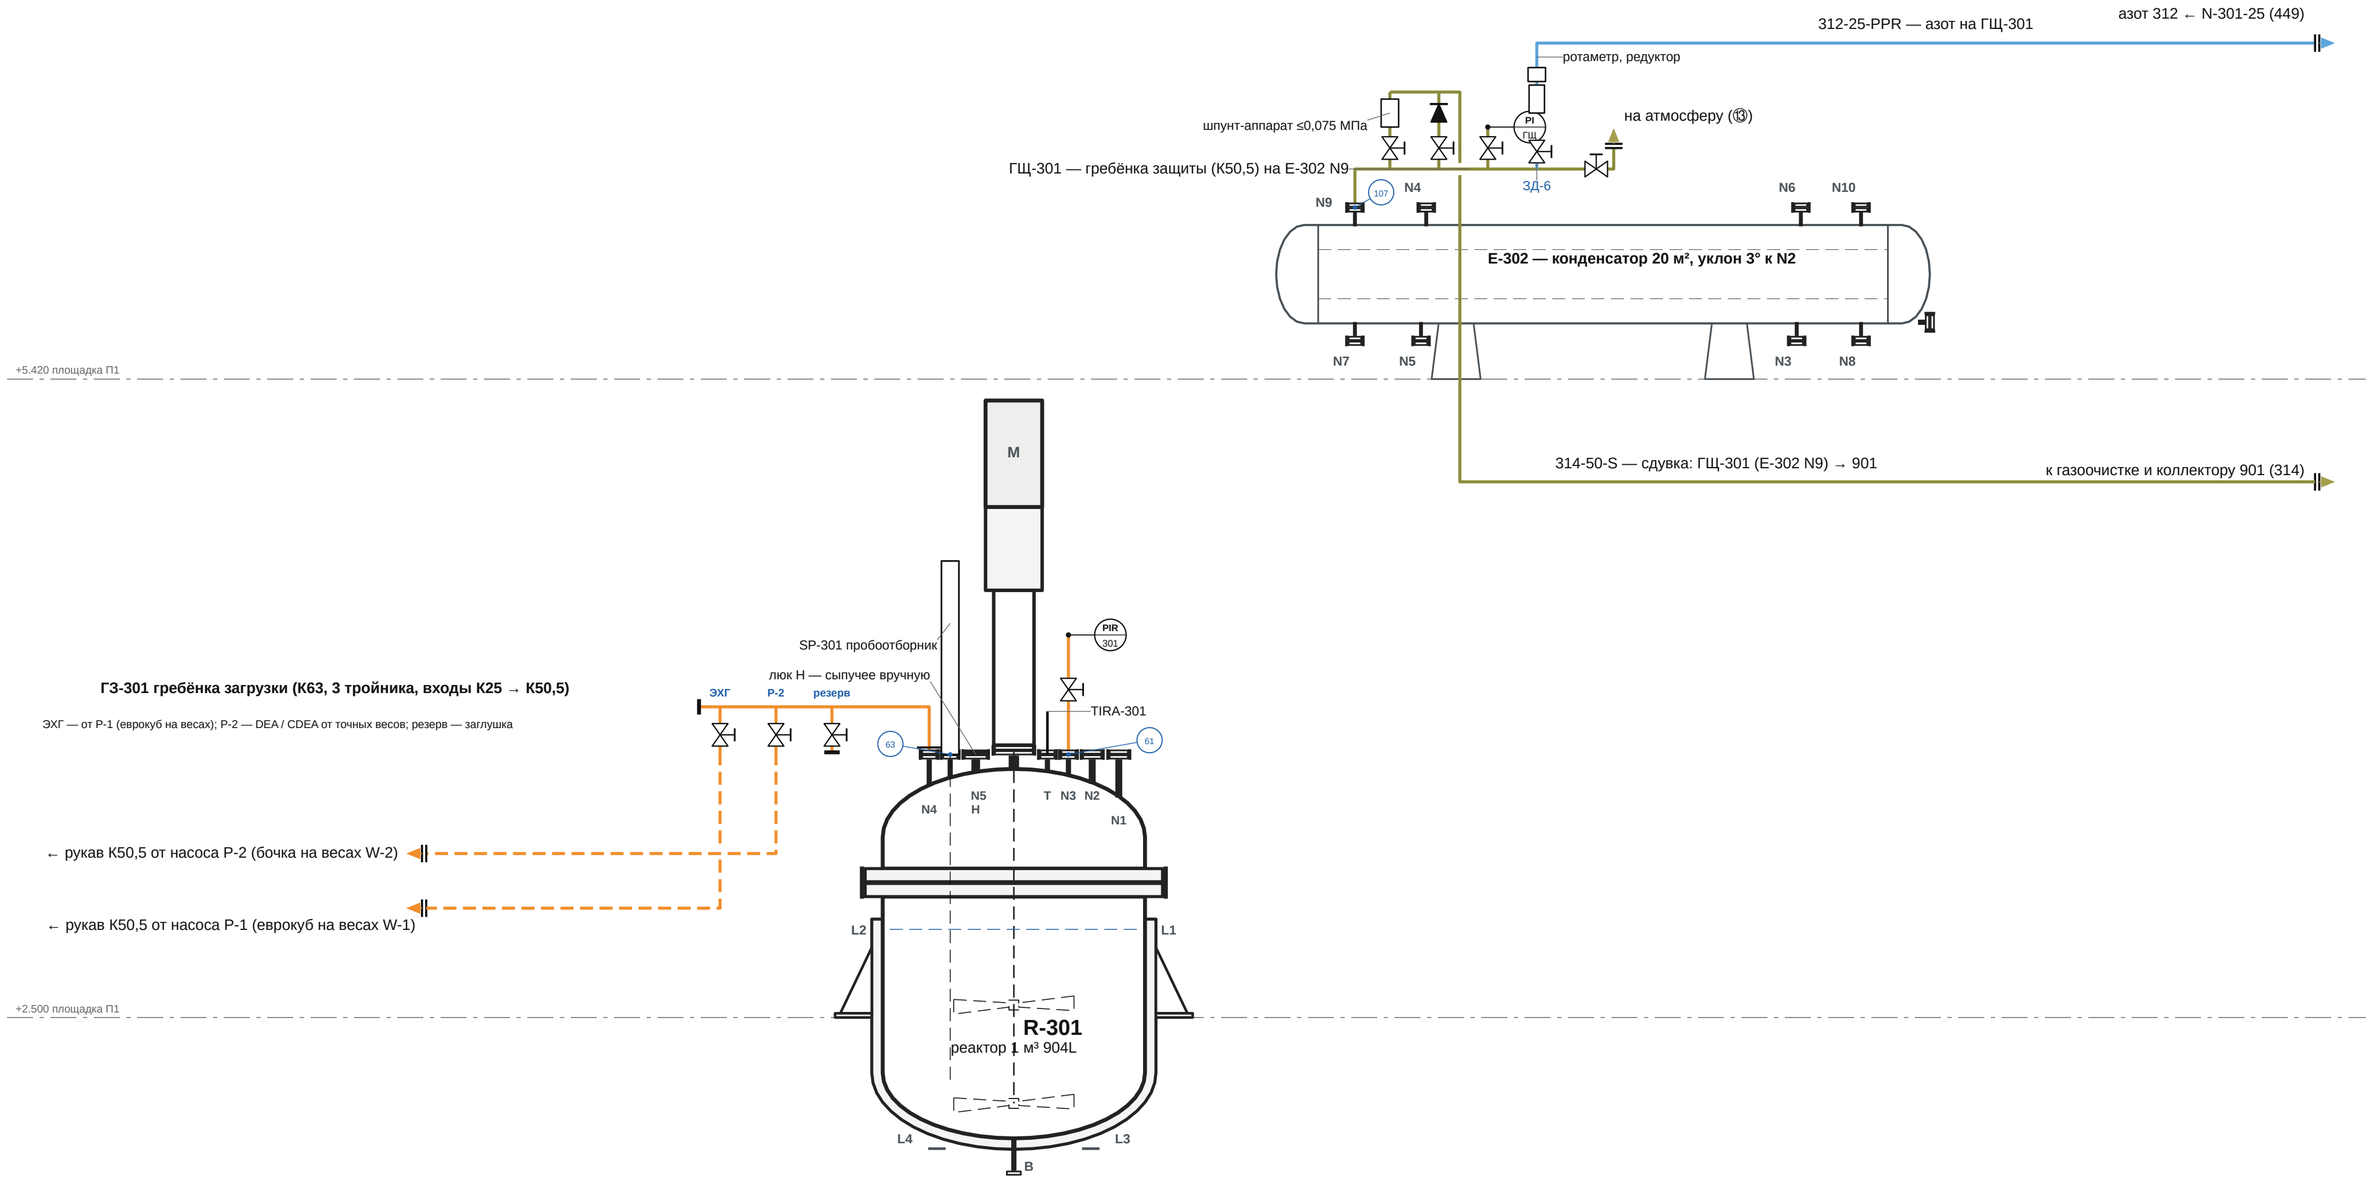

ГЗ-301 гребёнка загрузки (К63, 3 тройника, входы К25 → К50,5)

ЭХГ — от Р-1 (еврокуб на весах); Р-2 — DEA / CDEA от точных весов; резерв — заглушка


← рукав К50,5 от насоса Р-2 (бочка на весах W-2)

← рукав К50,5 от насоса Р-1 (еврокуб на весах W-1)

					ОПУ.ОБ.R-301.М.04	
Изм.	Лист	№ докум.	Подп.	Дата		
Разраб.					**Реактор 1 м³ 904L (R-301): крышка** реактора и гребёнки	Лит. П; Масса —; Масштаб б/м
Пров.						Лист 4; Листов 16
Т.контр.						
Н.контр.					Опытно-промышленный участок	**Опытно-промышленный участок**
Утв.						

Вакуум от конденсатора (E-302) N10 — 327; гребёнка защиты ГЩ-301 и сдувки 314 (N9 E-302); азот 312 на ГЩ-301, 323 и 335 на сборник (X-303)


Аппараты целиком, М 1:17; отметки — по 3D-модели; номера соединений — как в ведомости соединений

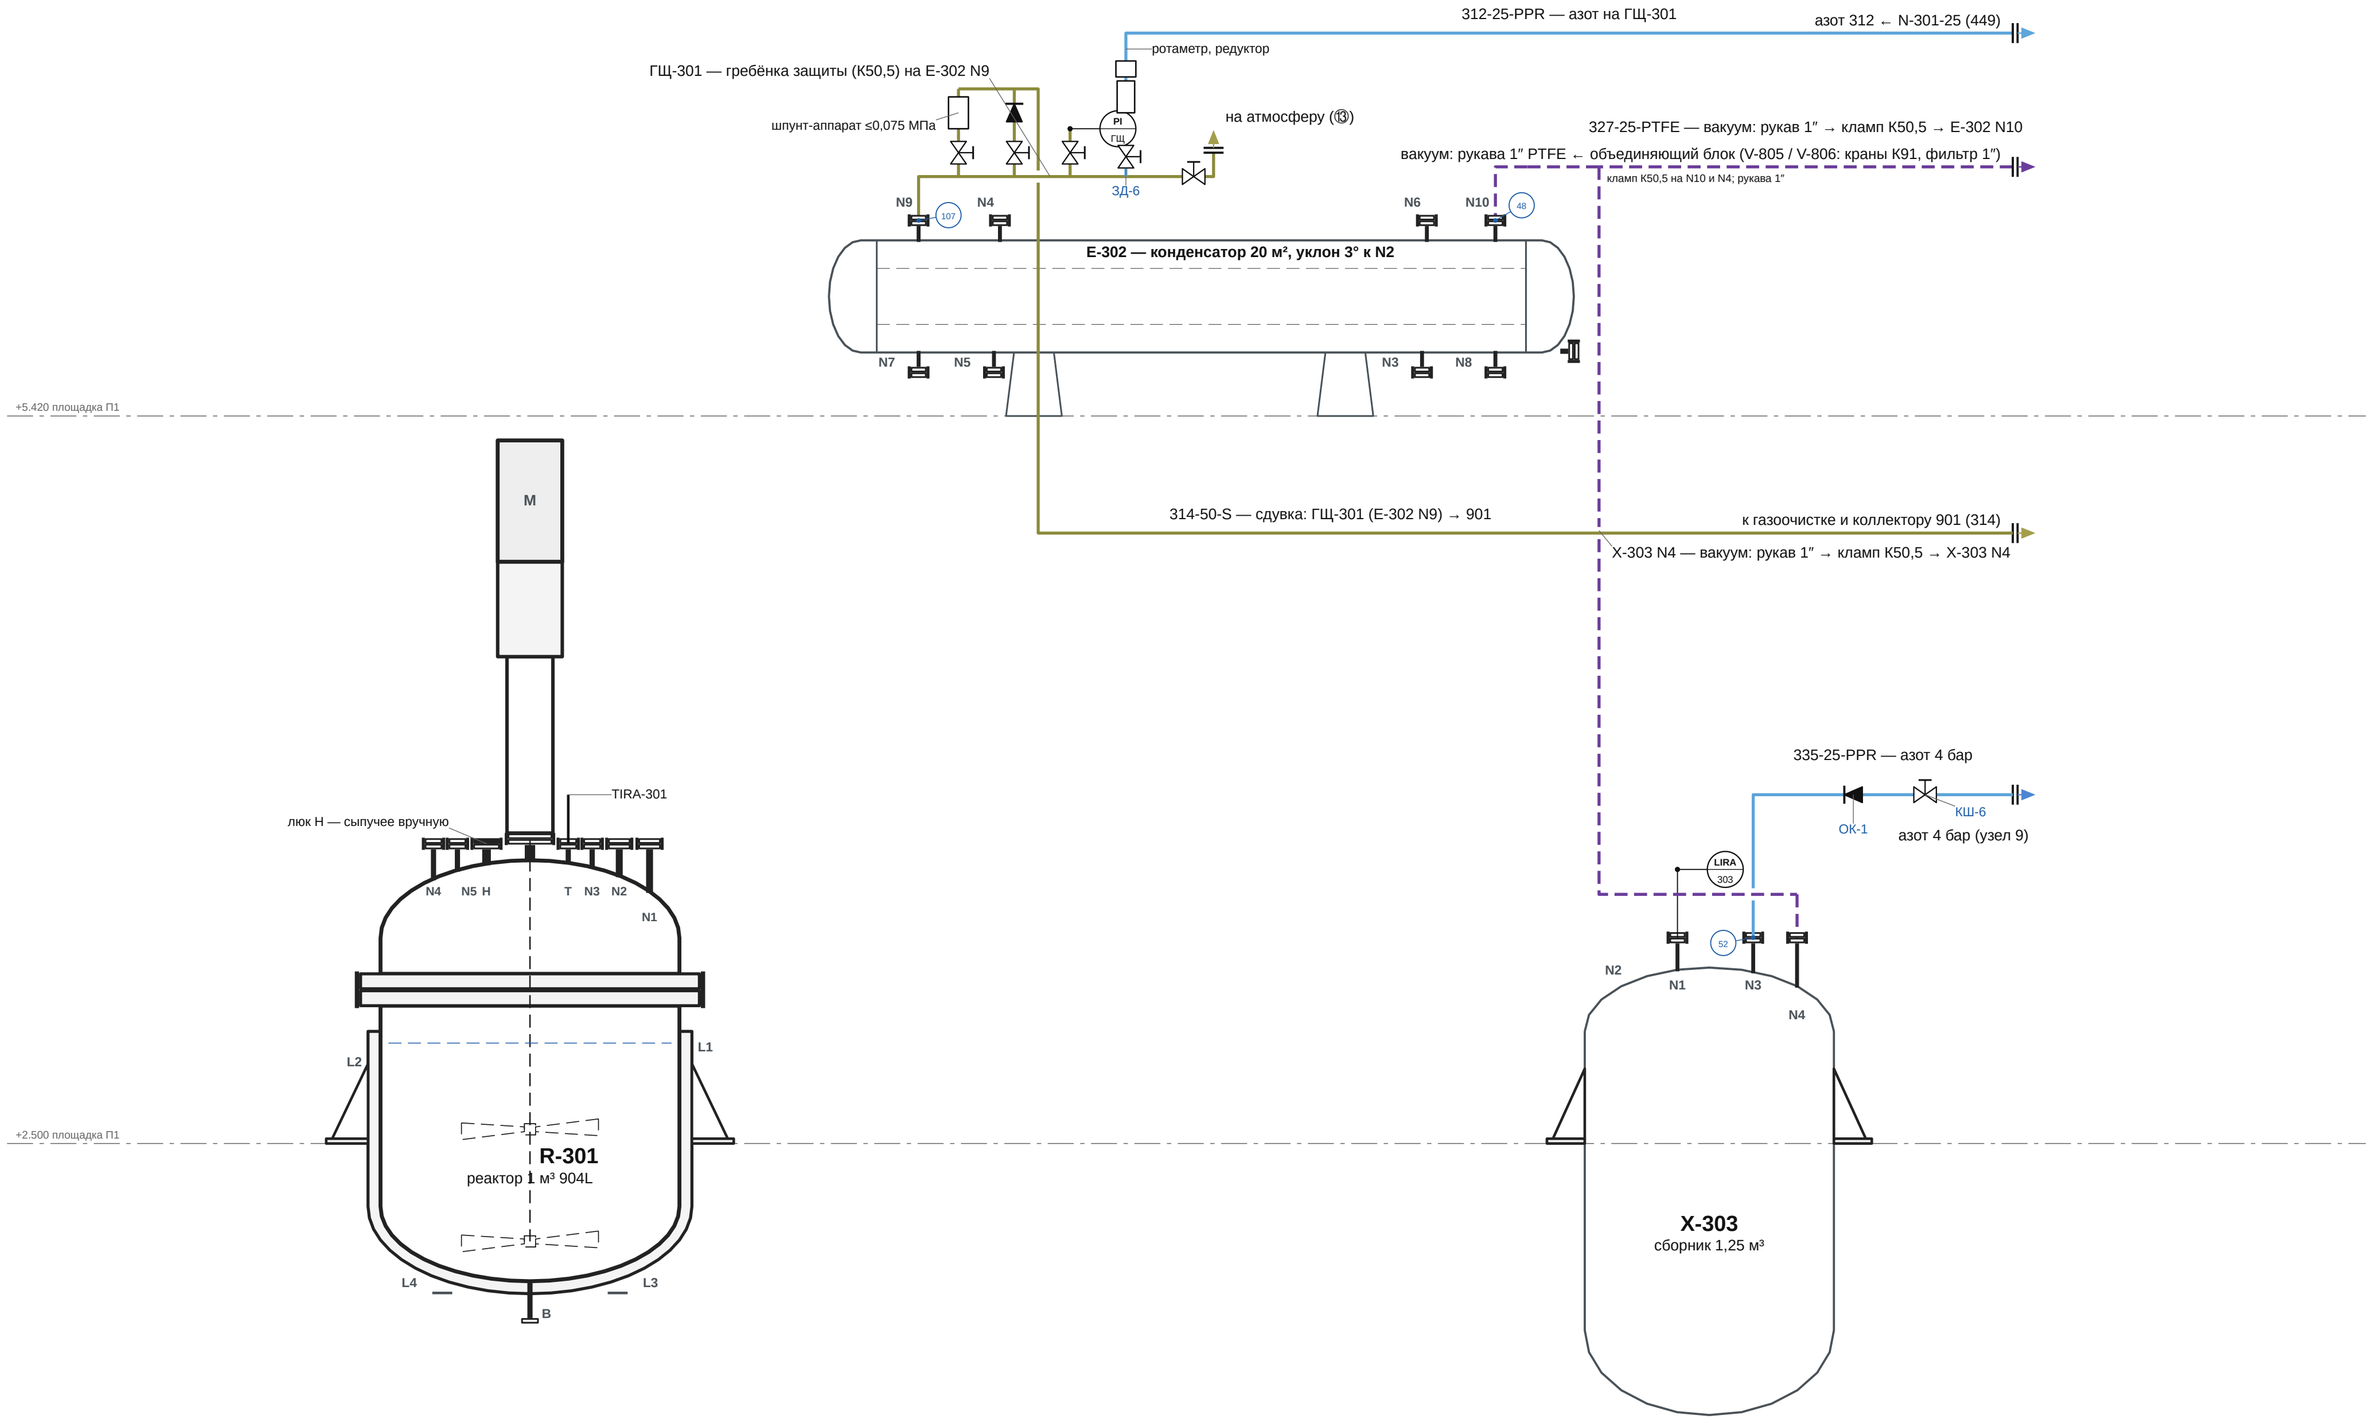

					ОПУ.ОБ.R-301.М.05	
Изм.	Лист	№ докум.	Подп.	Дата		
Разраб.					**Реактор 1 м³ 904L (R-301):** вакуум, сдувка, азот сборника	Лит. П; Масса —; Масштаб б/м
Пров.						Лист 5; Листов 16
Т.контр.						
Н.контр.					Опытно-промышленный участок	**Опытно-промышленный участок**
Утв.						

Вода охлаждения конденсатора (E-302): подача 317 на N3, возврат 318 с N4; дренаж и воздушник межтрубного N5, N6


Аппараты целиком, М 1:9; отметки — по 3D-модели; номера соединений — как в ведомости соединений

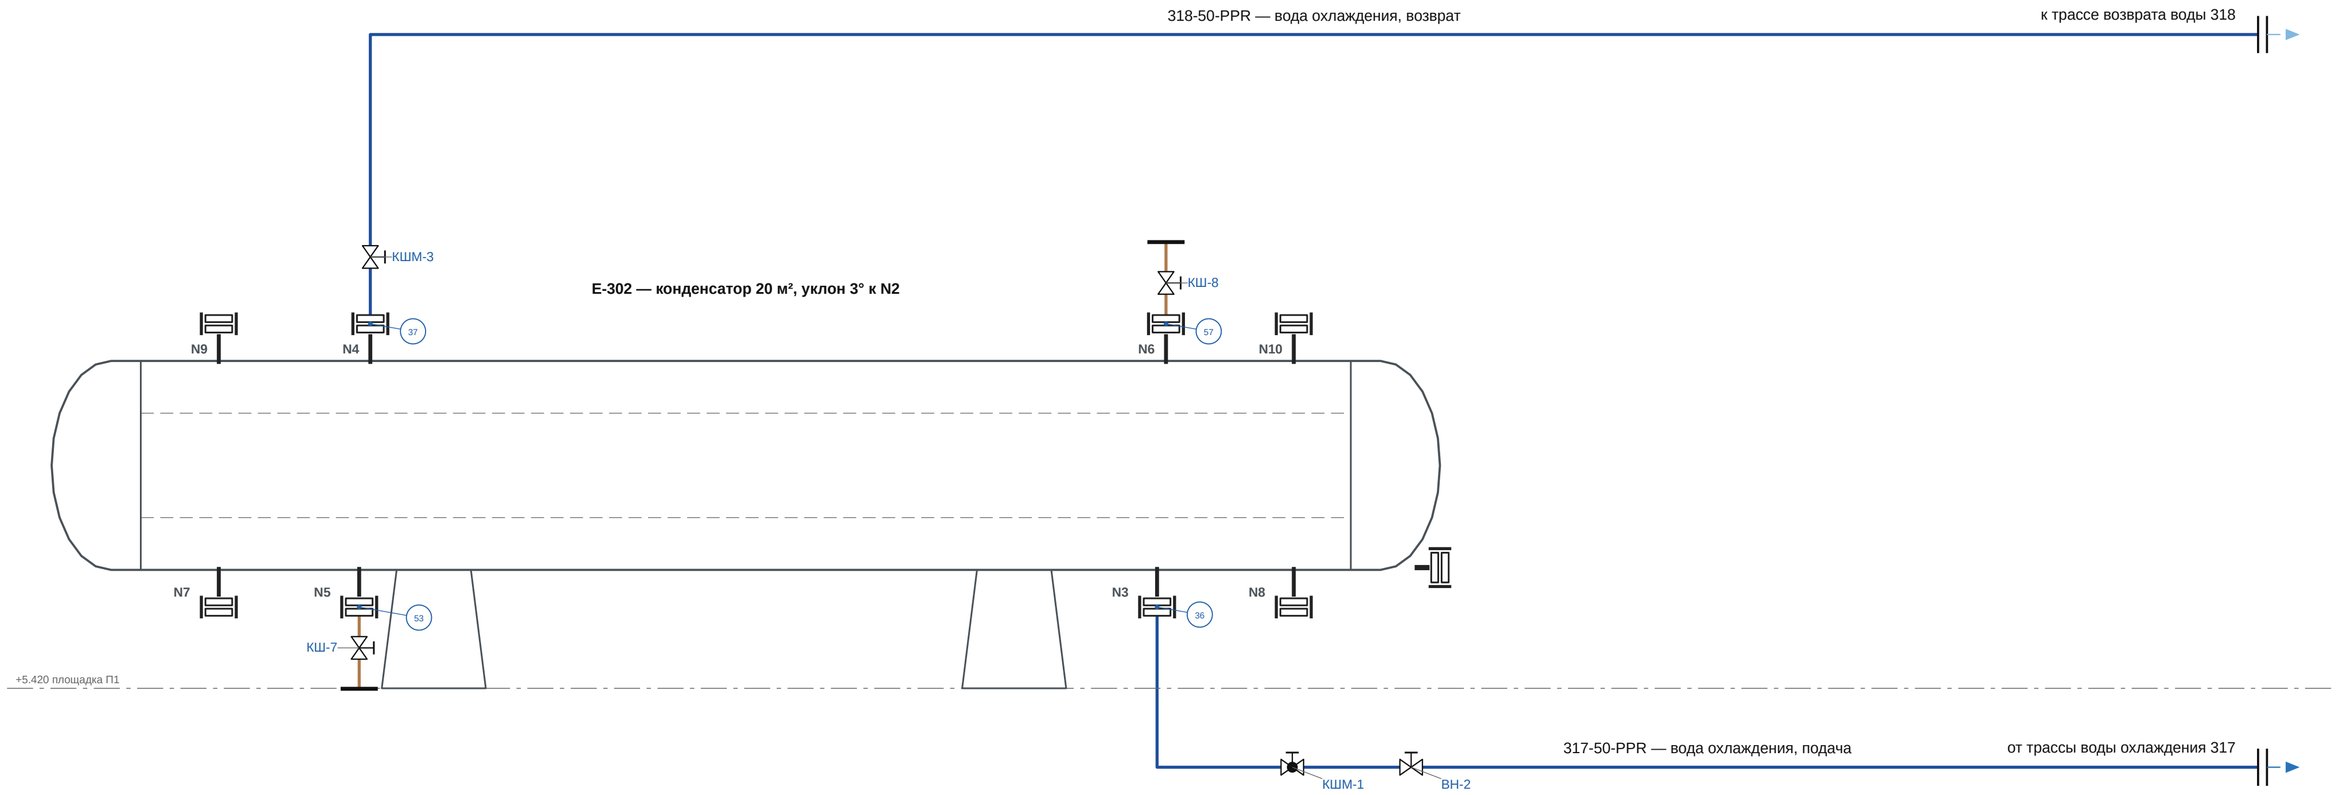

Изм.	Лист	№ докум.	Подп.	Дата	ОПУ.ОБ.R-301.М.06		
Разраб.					**Реактор 1 м³ 904L (R-301): вода охлаждения конденсатора**	Лит.	Масса	Масштаб
Пров.						П	—	б/м
Т.контр.						Лист 6		Листов 16
Н.контр.					Опытно-промышленный участок	**Опытно-промышленный участок**		
Утв.								

Рубашка реактора (R-301): масло — подача 325 в L3/L4, возврат 326 из L1/L2, воздушник g, дренаж k

Аппараты целиком, М 1:13; отметки — по 3D-модели; номера соединений — как в ведомости соединений

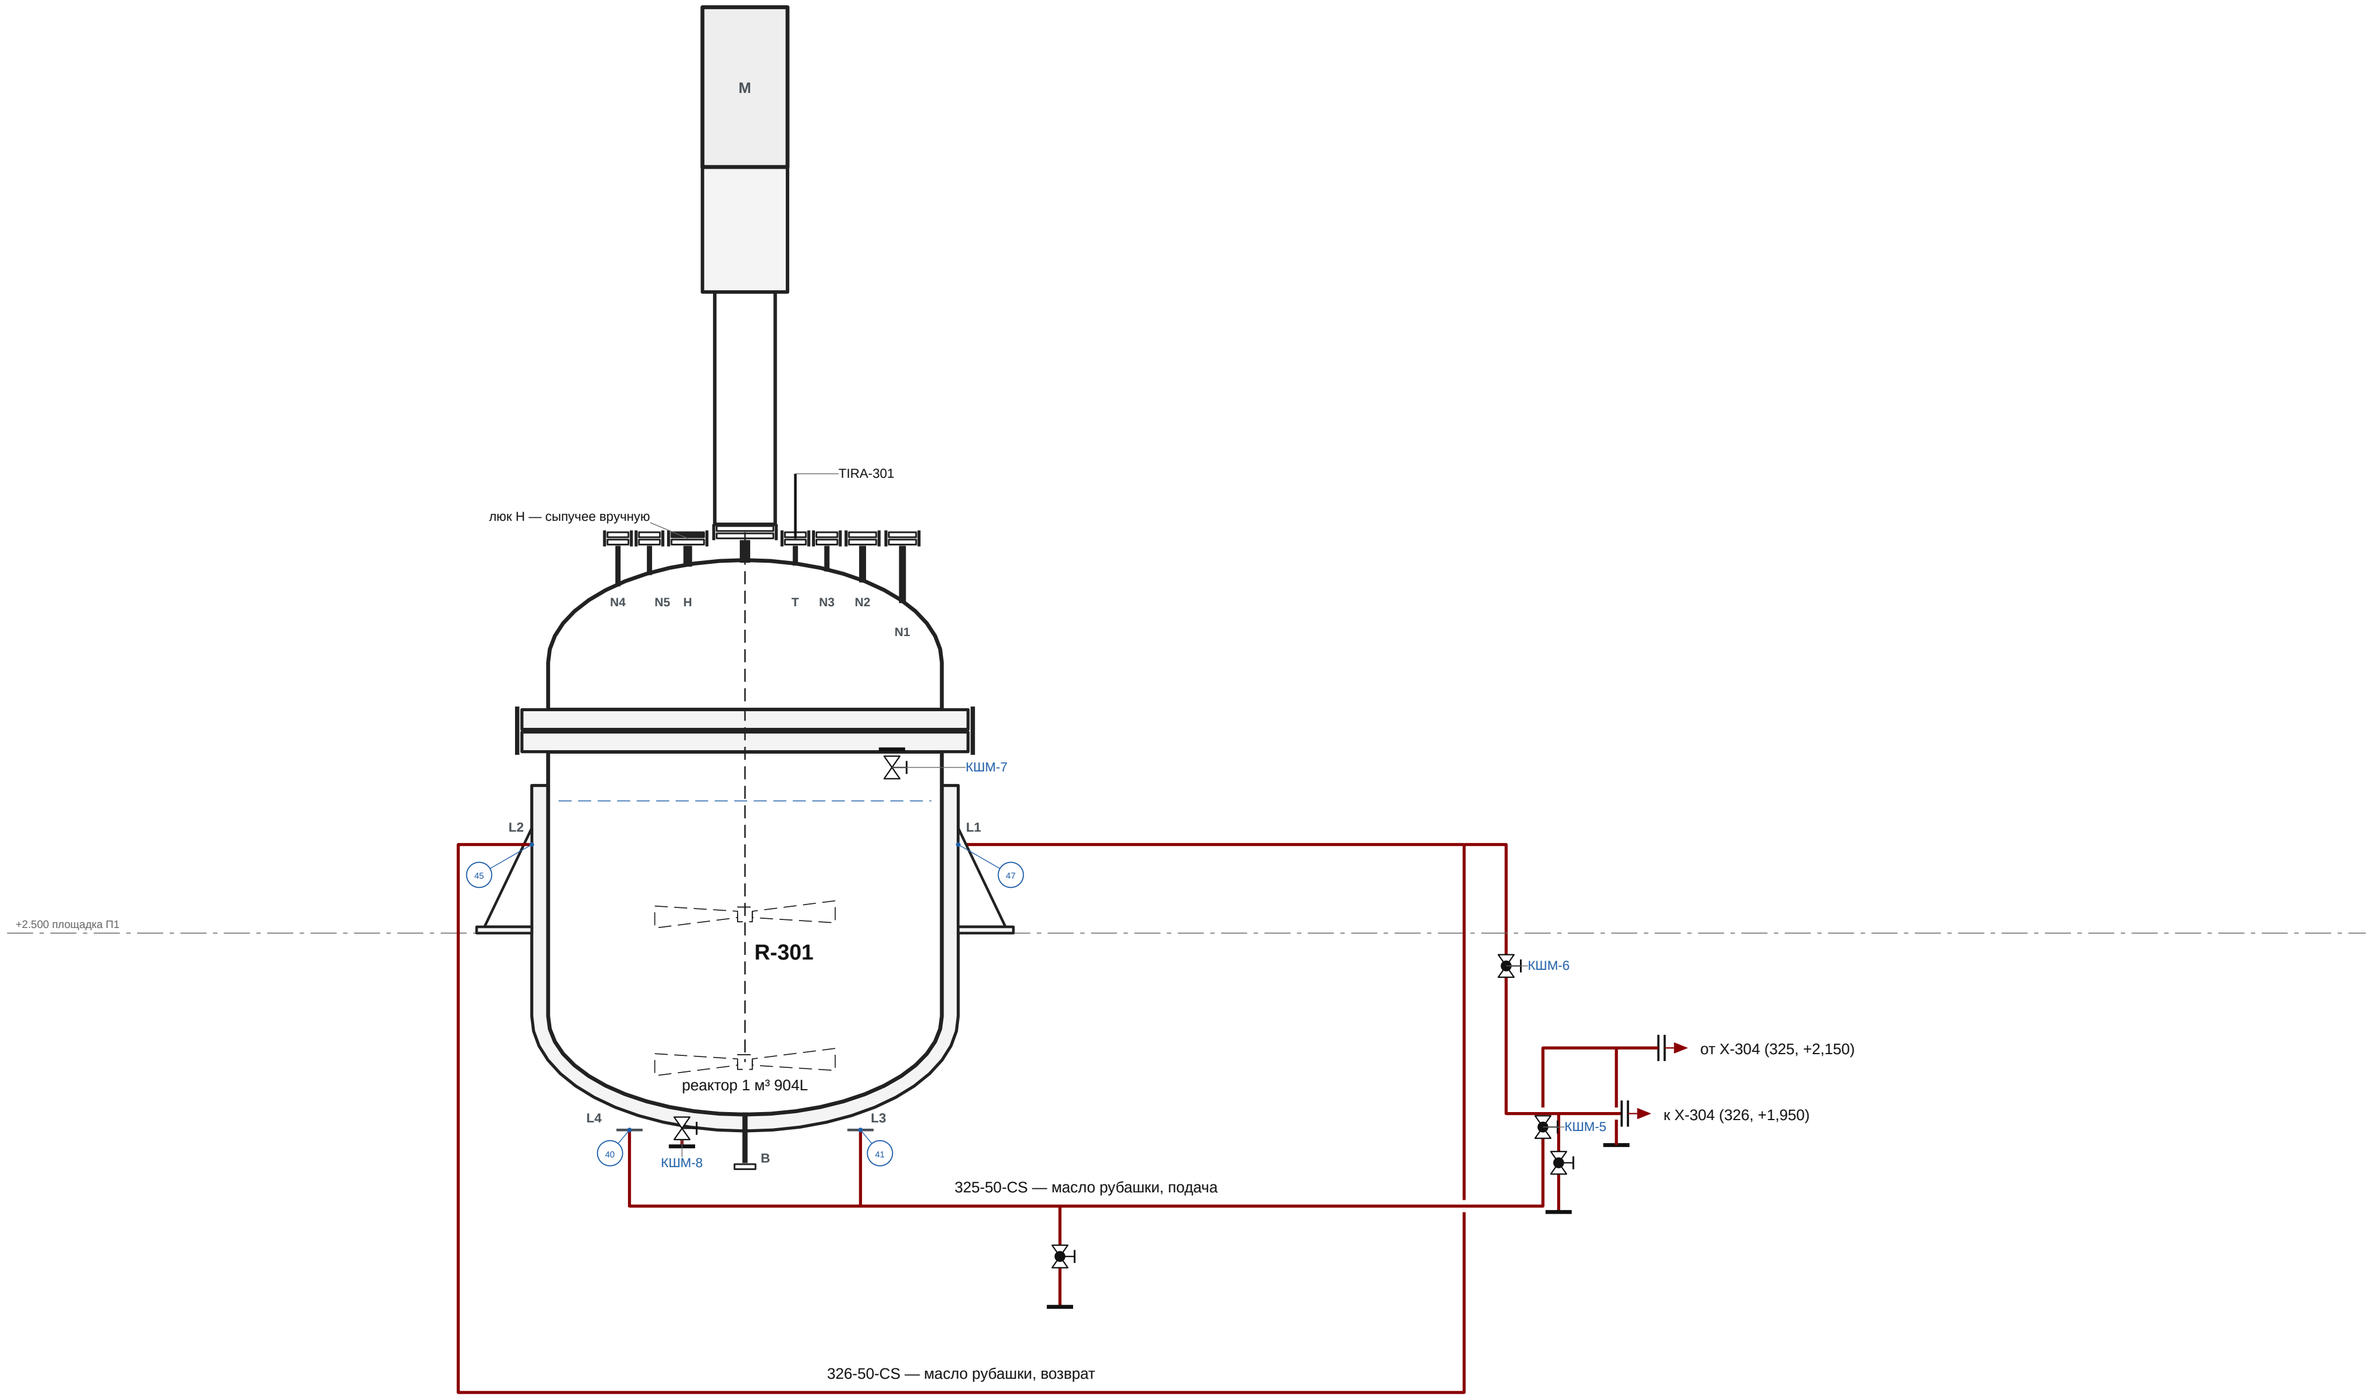

Изм.	Лист	№ докум.	Подп.	Дата	ОПУ.ОБ.R-301.M.07			
Разраб.					**Реактор 1 м³ 904L (R-301):** рубашка реактора	Лит.	Масса	Масштаб
Пров.						П	—	б/м
Т.контр.						Лист 7		Листов 16
Н.контр.								
Утв.					Опытно-промышленный участок	**Опытно-промышленный участок**		

Аварийный сброс 310-150-S: мембрана на N1 → своя ёмкость аварийная (V-301/3) на улице


Аппараты целиком, М 1:17; отметки — по 3D-модели; номера соединений — как в ведомости соединений


+5.420 площадка П1

+2.500 площадка П1

±0.000 пол

310-150-S — аварийный сброс в V-301/3 (по модели +5,000)

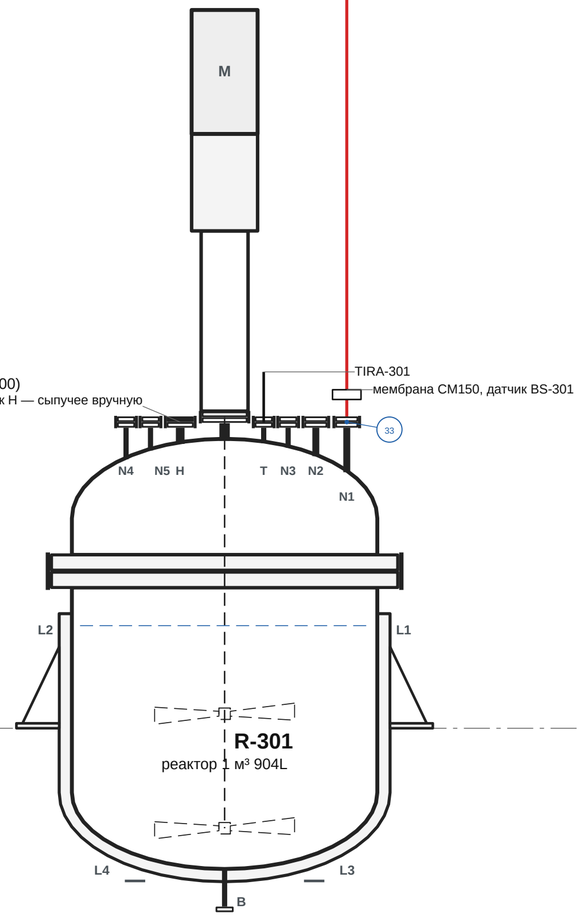

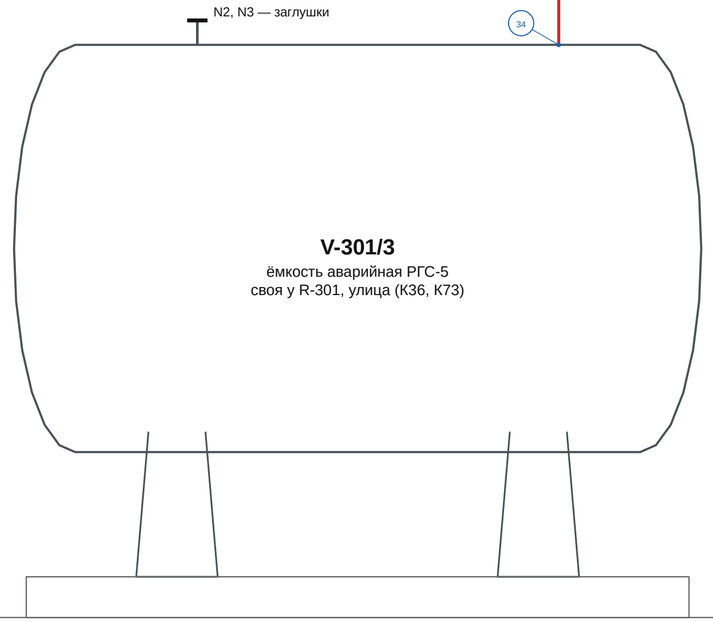

					ОПУ.ОБ.R-301.М.08	
Изм.	Лист	№ докум.	Подп.	Дата		
Разраб.					**Реактор 1 м³ 904L (R-301):** аварийный сброс 310	Лит. П; Масса —; Масштаб б/м
Пров.						Лист 8; Листов 16
Т.контр.						
Н.контр.						
Утв.					Опытно-промышленный участок	**Опытно-промышленный участок**

Центрифуга X-306 под реактором: суспензия 305 из донного клапана R-301, азот 324, фильтрат → P-306 → еврокуб; отгон X-303 → еврокуб

Аппараты целиком, М 1:19; отметки — по 3D-модели; номера соединений — как в ведомости соединений

+5.420 площадка П1

+2.500 площадка П1

±0.000 пол

M

люк H — сыпучее вручную

TIRA-301

N5 H

T N3 N2

N4

N1

L2

L1

L4

L3

62

B

R-301

реактор 1 м³ 904L

азот 324 ← коллектор 449

КШ-5

324-25-PPR — азот на X-306

клапан донный, кламп K63, рукав

305-50-S — слив суспензии в X-306

X-306

центрифуга PS800NA

M

P

P-305 насос AODD (Ex) — суспензия в X-306

X-306/фильтрат — фильтрат

P

КШ-10

LIRA 303

N2

N1

N3

N4

X-303

сборник 1,25 м³

66


КШ-9


кламп K63 с заглушкой; рукав в еврокуб — по месту (отгон → X-600)

еврокуб на тележке: фильтрат X-306 (насос P-306)

					ОПУ.ОБ.R-301.M.09	
Изм.	Лист	№ докум.	Подп.	Дата		
Разраб.					**Реактор 1 м³ 904L (R-301):** центрифуга и сливы	Лит. П; Масса —; Масштаб б/м
Пров.						
Т.контр.						Лист 9; Листов 16
Н.контр.						
Утв.					Опытно-промышленный участок	**Опытно-промышленный участок**

ГРЕБЁНКА ЗАГРУЗКИ ГЗ-301 НА N4 (М 1:15) И ГРЕБЁНКА ЗАЩИТЫ ГЩ-301 У N1 (М 1:10) — ВИДЫ С ЗАПАДА (север — слева)

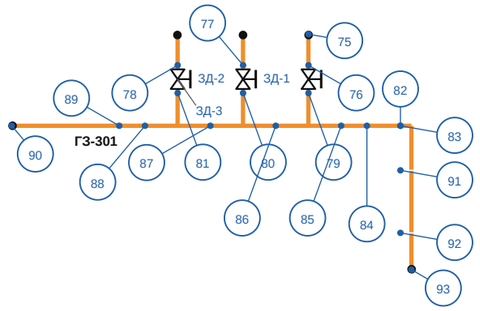

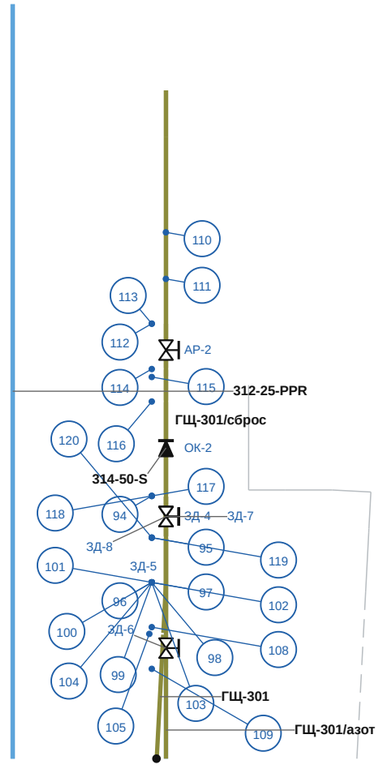

ВХОДЫ ГРЕБЁНКИ ЗАГРУЗКИ (коллектор К63, под тройником — кран К63 и переход К63→К25)

Вход ГЗ-301	Назначение	Подключение
RES	резерв	заглушка К25, табличка
P2	DEA / CDEA от точных весов (насос Р-2)	переход К25→К63, рукав К63 от насоса Р-1
ECH	ЭХГ	переход К25→К63, рукав К63 от насоса Р-1

ВЕТКИ ГРЕБЁНКИ ЗАЩИТЫ (коллектор К25 от врезки в 310 ниже мембраны)

Ветка ГЩ-301	Что стоит	Выход
обр	кран К25 → клапан обратный пружинный (кран закрыт только на время вакуумирования)	→ 314
шпунт	кран К25 → шпунт-аппарат с манометром, уставка ≤ 0,075 МПа (уточнить)	→ 314
азот	кран К25 → ротаметр с вентилем → редуктор ← 312 (коллектор 449)	азотная подушка
PI	кран К25 → мановакуумметр PI-ГЩ −0,1…0,15 МПа	—
атм	кран К25 → «гусак» с сеткой (сброс на атмосферу)	атмосфера (⚿3)

Кламп называется по феруле: К63 — ферула Ø64 (труба 51×1,5), К25 — ферула Ø25 (труба 19,05×1,65, 3/4″). Прокладки — PTFE; хомуты — AISI 304.

Гребёнку загрузки наращивают по мере надобности: конец коллектора — заглушка К63. Рукав К63 от поста дозирования перекидывается на нужный вход.

Мембрана разрывная на N1 и аварийный сброс 310 — без изменений; гребёнка защиты заменяет огнепреградитель КДЗТ-50А (К73).

Изм.	Лист	№ докум.	Подп.	Дата
Разраб.				
Пров.				
Т.контр.				
Н.контр.				
Утв.				

ОПУ.ОБ.R-301.М.10

Реактор 1 м³ 904L (R-301):
гребёнки загрузки и защиты

Лит.	Масса	Масштаб
П	—	1:10

Лист 10 | Листов 16

Опытно-промышленный участок

Опытно-промышленный участок

ВЕДОМОСТЬ СОЕДИНЕНИЙ (1)

№	Линия	DN	Тип	Крепёж и прокладка	X, мм	Y, мм	Отм., м
1	301-150-SS	150	фланцевое	8 шпилек M24×124 с гайками (A2-70), прокладка PTFE (фторопласт-4)	22538	13189	+6,00
2	301-150-SS	150	фланцевое	соединение фланцевое DN150 PN25 — разъём шлемовой трубы (по схеме поставщика), 8 шпилек M24, прокладка PTFE	22538	13557	+4,27
3	301-150-SS	150	фланцевое	8 шпилек M24×124 с гайками (A2-70), прокладка PTFE (фторопласт-4)	22538	13557	+3,70
4	302-80-SS	100	фланцевое	8 шпилек M20×106 с гайками (A2-70), прокладка PTFE (фторопласт-4)	22538	10199	+5,69
5	302-80-SS	80	фланцевое	8 шпилек M16×88 с гайками (A2-70), прокладка PTFE (фторопласт-4)	22538	9655	+4,88
6	302-80-SS	80	фланцевое	8 шпилек M16×88 с гайками (A2-70), прокладка PTFE (фторопласт-4)	22538	9655	+4,66
7	302-80-SS	80	фланцевое	8 шпилек M16×88 с гайками (A2-70), прокладка PTFE (фторопласт-4)	22538	9655	+4,45
8	302-80-SS	80	фланцевое	8 шпилек M16×88 с гайками (A2-70), прокладка PTFE (фторопласт-4)	22538	9655	+4,11
9	302-80-SS	80	фланцевое	8 шпилек M16×88 с гайками (A2-70), прокладка PTFE (фторопласт-4)	22538	9655	+3,81
10	302-80-SS	100	фланцевое	8 шпилек M20×106 с гайками (A2-70), прокладка PTFE (фторопласт-4)	22538	9655	+3,28
11	302Д-25-SS	25	фланцевое	4 шпилек M12×73 с гайками (A2-70), прокладка PTFE (фторопласт-4)	22538	11344	+3,45
12	302Д-25-SS	25	фланцевое	4 шпилек M12×73 с гайками (A2-70), прокладка PTFE (фторопласт-4)	22538	11471	+3,45
13	302Ф-50-SS	80	фланцевое	8 шпилек M16×88 с гайками (A2-70), прокладка PTFE (фторопласт-4)	22538	9805	+3,96
14	302Ф-50-SS	50	фланцевое	4 шпилек M16×84 с гайками (A2-70), прокладка PTFE (фторопласт-4)	22538	10021	+3,96
15	302Ф-50-SS	50	фланцевое	4 шпилек M16×84 с гайками (A2-70), прокладка PTFE (фторопласт-4)	22538	10213	+3,96
16	302Ф-50-SS	50	фланцевое	4 шпилек M16×84 с гайками (A2-70), прокладка PTFE (фторопласт-4)	22538	12843	+3,83
17	302Ф-50-SS	50	фланцевое	4 шпилек M16×84 с гайками (A2-70), прокладка PTFE (фторопласт-4)	22538	13075	+3,82
18	302Ф-50-SS	50	фланцевое	4 шпилек M16×84 с гайками (A2-70), прокладка PTFE (фторопласт-4)	22538	13367	+3,81
19	303-25-SS	25	фланцевое	4 шпилек M12×73 с гайками (A2-70), прокладка PTFE (фторопласт-4)	22538	12847	+5,64
20	303-25-SS	25	фланцевое	4 шпилек M12×73 с гайками (A2-70), прокладка PTFE (фторопласт-4)	22538	10535	+5,51
21	303-25-SS	25	фланцевое	4 шпилек M12×73 с гайками (A2-70), прокладка PTFE (фторопласт-4)	22538	10559	+5,05
22	303-25-SS	25	фланцевое	4 шпилек M12×73 с гайками (A2-70), прокладка PTFE (фторопласт-4)	22538	12877	+5,05
23	303-25-SS	25	фланцевое	4 шпилек M12×73 с гайками (A2-70), прокладка PTFE (фторопласт-4)	22538	10566	+4,92
24	303-25-SS	25	фланцевое	4 шпилек M12×73 с гайками (A2-70), прокладка PTFE (фторопласт-4)	22538	12884	+4,92
25	303-25-SS	25	фланцевое	4 шпилек M12×73 с гайками (A2-70), прокладка PTFE (фторопласт-4)	22538	9766	+4,55
26	305-50-S		кламповое	соединение кламповое Ø64 (хомут AISI 304 с барашковой гайкой, прокладка FFKM)	21164	13781	+1,79
27	305-50-S	50	фланцевое	4 шпилек M16×84 с гайками (A2-70), прокладка FFKM	21191	13781	+1,71
28	305-50-S	100	фланцевое	8 шпилек M20×106 с гайками (A2-70), прокладка PTFE (фторопласт-4)	22247	14000	+1,48
29	305-50-S		кламповое	соединение кламповое Ø64 (хомут AISI 304 с барашковой гайкой, прокладка FFKM)	22193	14000	+1,39
30	305-50-S		кламповое	соединение кламповое Ø50.5 (хомут AISI 304 с барашковой гайкой, прокладка PTFE)	21877	14650	+0,40
31	305-50-S		кламповое	соединение кламповое Ø50.5 (хомут AISI 304 с барашковой гайкой, прокладка PTFE)	21900	14500	+0,08
32	310-150-S	150	фланцевое	8 шпилек M20 насквозь, прокладки в держателе	22850	13775	+4,18
33	310-150-S	150	фланцевое	8 шпилек M24×124 с гайками (A2-70), прокладка PTFE (фторопласт-4)	22850	13775	+3,70
34	310-150-S	200	фланцевое	12 шпилек M20×106 с гайками (A2-70), прокладка PTFE (фторопласт-4)	23300	20000	+2,46
35	312-25-PPR	25	фланцевое	4 шпилек M12×98 с гайками (A2-70), прокладка EPDM	21630	12550	+5,60
36	317-50-PPR	50	фланцевое	4 шпилек M16×84 с гайками (A2-70), прокладка паронитовая ПОН-Б	22538	10829	+5,52
37	318-50-PPR	50	фланцевое	4 шпилек M16×84 с гайками (A2-70), прокладка паронитовая ПОН-Б	22538	12484	+6,32
38	324-25-PPR	15	фланцевое	4 шпилек M12×82 с гайками (A2-70), прокладка EPDM	21450	14330	+2,00
39	324-25-PPR		кламповое	соединение кламповое Ø34 (хомут AISI 304 с барашковой гайкой, прокладка PTFE)	20983	13902	+1,72
40	325-50-CS	40	фланцевое	4 шпилек M16×84 с гайками (A2-70), прокладка паронитовая ПОН-Б	22810	14000	+1,85

Изм.	Лист	№ докум.	Подп.	Дата
Разраб.				
Пров.				
Т.контр.				
Н.контр.				
Утв.				

ОПУ.ОБ.R-301.M.11

Реактор 1 м³ 904L (R-301):
ведомость соединений (1)

Лит.	Масса	Масштаб
П	—	б/м

Лист 11 | Листов 16

Опытно-промышленный участок

Опытно-промышленный участок

ВЕДОМОСТЬ СОЕДИНЕНИЙ (2)

№	Линия	DN	Тип	Крепёж и прокладка	X, мм	Y, мм	Отм., м
41	325-50-CS	40	фланцевое	4 шпилек M16×84 с гайками (A2-70), прокладка паронитовая ПОН-Б	22110	14000	+1,85
42	325-50-CS	40	фланцевое	4 шпилек M16×84 с гайками (A2-70), прокладка паронитовая ПОН-Б	22810	14000	+1,50
43	325-50-CS	40	фланцевое	4 шпилек M16×84 с гайками (A2-70), прокладка паронитовая ПОН-Б	22110	14000	+1,50
44	326-50-CS	40	фланцевое	4 шпилек M16×84 с гайками (A2-70), прокладка паронитовая ПОН-Б	21349	14000	+2,77
45	326-50-CS	40	фланцевое	4 шпилек M16×84 с гайками (A2-70), прокладка паронитовая ПОН-Б	21701	14000	+2,77
46	326-50-CS	40	фланцевое	4 шпилек M16×84 с гайками (A2-70), прокладка паронитовая ПОН-Б	23571	14000	+2,77
47	326-50-CS	40	фланцевое	4 шпилек M16×84 с гайками (A2-70), прокладка паронитовая ПОН-Б	23219	14000	+2,77
48	327-25-PTFE	25	фланцевое	4 шпилек M12×73 с гайками (A2-70), прокладка PTFE (фторопласт-4)	22538	10499	+6,21
49	335-25-PPR	25	фланцевое	4 шпилек M12×86 с гайками (A2-70), прокладка EPDM	22248	9733	+3,80
50	335-25-PPR	25	фланцевое	4 шпилек M12×73 с гайками (A2-70), прокладка PTFE (фторопласт-4)	22248	9733	+3,66
51	335-25-PPR	25	фланцевое	4 шпилек M12×73 с гайками (A2-70), прокладка PTFE (фторопласт-4)	22248	9733	+3,50
52	335-25-PPR	50	фланцевое	4 шпилек M16×84 с гайками (A2-70), прокладка PTFE (фторопласт-4)	22248	9733	+3,28
53	E-302 N5	25	фланцевое	4 шпилек M12×73 с гайками (A2-70), прокладка PTFE (фторопласт-4)	22538	12521	+5,61
54	E-302 N5	25	фланцевое	4 шпилек M12×73 с гайками (A2-70), прокладка PTFE (фторопласт-4)	22625	12525	+5,53
55	E-302 N5	25	фланцевое	4 шпилек M12×73 с гайками (A2-70), прокладка PTFE (фторопласт-4)	22752	12525	+5,53
56	E-302 N6	25	фланцевое	4 шпилек M12×73 с гайками (A2-70), прокладка PTFE (фторопласт-4)	22538	10785	+6,36
57	E-302 N6	25	фланцевое	4 шпилек M12×73 с гайками (A2-70), прокладка PTFE (фторопласт-4)	22538	10792	+6,23
58	LIRA-303	50	фланцевое	4 шпилек M16×84 с гайками (A2-70), прокладка PTFE (фторопласт-4)	22750	9867	+3,28
59	PIR-301	25	фланцевое	4 шпилек M12×73 с гайками (A2-70), прокладка PTFE (фторопласт-4)	22235	13610	+4,00
60	PIR-301	25	фланцевое	4 шпилек M12×73 с гайками (A2-70), прокладка PTFE (фторопласт-4)	22235	13610	+3,87
61	PIR-301	80	фланцевое	8 шпилек M16×96 с гайками (A2-70), прокладка PTFE (фторопласт-4)	22235	13610	+3,70
62	R-301 B	100	фланцевое	8 шпилек M20×106 с гайками (A2-70), прокладка PTFE (фторопласт-4)	22460	14000	+1,78
63	SP-301	80	фланцевое	8 шпилек M16×96 с гайками (A2-70), прокладка PTFE (фторопласт-4)	22142	14318	+3,70
64	TIRA-301	80	фланцевое	8 шпилек M16×96 с гайками (A2-70), прокладка PTFE (фторопласт-4)	22778	14318	+3,70
65	X-303 N4	50	фланцевое	4 шпилек M16×84 с гайками (A2-70), прокладка PTFE (фторопласт-4)	22170	10023	+3,28
66	X-303/слив	50	фланцевое	4 шпилек M16×84 с гайками (A2-70), прокладка PTFE (фторопласт-4)	22460	9945	+1,39
67	X-303/слив	50	фланцевое	4 шпилек M16×84 с гайками (A2-70), прокладка PTFE (фторопласт-4)	22460	9945	+1,24
68	X-303/слив		кламповое	соединение кламповое Ø64 (хомут AISI 304 с барашковой гайкой, прокладка PTFE)	22433	9945	+1,16
69	X-306/фильтрат		кламповое	соединение кламповое Ø64 (хомут AISI 304 с барашковой гайкой, прокладка PTFE)	20974	10900	+1,54
70	X-306/фильтрат	50	фланцевое	4 шпилек M16×84 с гайками (A2-70), прокладка PTFE (фторопласт-4)	21001	12671	+0,66
71	X-306/фильтрат	100	фланцевое	8 шпилек M16×88 с гайками (A2-70), прокладка PTFE (фторопласт-4)	21001	12902	+0,66
72	X-306/фильтрат	100	фланцевое	8 шпилек M16×88 с гайками (A2-70), прокладка PTFE (фторопласт-4)	21001	13094	+0,66
73	X-306/фильтрат		кламповое	соединение кламповое Ø50.5 (хомут AISI 304 с барашковой гайкой, прокладка PTFE)	20978	11700	+0,40
74	X-306/фильтрат		кламповое	соединение кламповое Ø50.5 (хомут AISI 304 с барашковой гайкой, прокладка PTFE)	21001	11850	+0,08
75	ГЗ-301		кламповое	соединение кламповое Ø50.5 (хомут AISI 304 с барашковой гайкой, прокладка PTFE)	21659	14330	+4,28
76	ГЗ-301		кламповое	соединение кламповое Ø64 (хомут AISI 304 с барашковой гайкой, прокладка PTFE)	21662	14330	+4,20
77	ГЗ-301		кламповое	соединение кламповое Ø64 (хомут AISI 304 с барашковой гайкой, прокладка PTFE)	21662	14490	+4,20
78	ГЗ-301		кламповое	соединение кламповое Ø64 (хомут AISI 304 с барашковой гайкой, прокладка PTFE)	21662	14650	+4,20
79	ГЗ-301		кламповое	соединение кламповое Ø64 (хомут AISI 304 с барашковой гайкой, прокладка PTFE)	21662	14330	+4,14
80	ГЗ-301		кламповое	соединение кламповое Ø64 (хомут AISI 304 с барашковой гайкой, прокладка PTFE)	21662	14490	+4,14

Изм.	Лист	№ докум.	Подп.	Дата
Разраб.				
Пров.				
Т.контр.				
Н.контр.				
Утв.				

ОПУ.ОБ.R-301.M.12

Реактор 1 м³ 904L (R-301):
ведомость соединений (2)

Лит.	Масса	Масштаб
П	—	б/м

Лист 12 | Листов 16

Опытно-промышленный участок

Опытно-промышленный участок

ВЕДОМОСТЬ СОЕДИНЕНИЙ (3)

№	Линия	DN	Тип	Крепёж и прокладка	X, мм	Y, мм	Отм., м
81	ГЗ-301		кламповое	соединение кламповое Ø64 (хомут AISI 304 с барашковой гайкой, прокладка PTFE)	21662	14650	+4,14
82	ГЗ-301		кламповое	соединение кламповое Ø64 (хомут AISI 304 с барашковой гайкой, прокладка PTFE)	21908	14105	+4,06
83	ГЗ-301		кламповое	соединение кламповое Ø64 (хомут AISI 304 с барашковой гайкой, прокладка PTFE)	21745	14105	+4,06
84	ГЗ-301		кламповое	соединение кламповое Ø64 (хомут AISI 304 с барашковой гайкой, прокладка PTFE)	21662	14187	+4,06
85	ГЗ-301		кламповое	соединение кламповое Ø64 (хомут AISI 304 с барашковой гайкой, прокладка PTFE)	21662	14250	+4,06
86	ГЗ-301		кламповое	соединение кламповое Ø64 (хомут AISI 304 с барашковой гайкой, прокладка PTFE)	21662	14410	+4,06
87	ГЗ-301		кламповое	соединение кламповое Ø64 (хомут AISI 304 с барашковой гайкой, прокладка PTFE)	21662	14570	+4,06
88	ГЗ-301		кламповое	соединение кламповое Ø64 (хомут AISI 304 с барашковой гайкой, прокладка PTFE)	21662	14730	+4,06
89	ГЗ-301		кламповое	соединение кламповое Ø64 (хомут AISI 304 с барашковой гайкой, прокладка PTFE)	21609	14793	+4,06
90	ГЗ-301		кламповое	соединение кламповое Ø64 (хомут AISI 304 с барашковой гайкой, прокладка PTFE)	21609	15056	+4,06
91	ГЗ-301		кламповое	соединение кламповое Ø64 (хомут AISI 304 с барашковой гайкой, прокладка PTFE)	22017	14105	+3,95
92	ГЗ-301		кламповое	соединение кламповое Ø64 (хомут AISI 304 с барашковой гайкой, прокладка PTFE)	22017	14105	+3,79
93	ГЗ-301	80	фланцевое	8 шпилек M16×96 с гайками (A2-70), прокладка PTFE (фторопласт-4)	22017	14078	+3,70
94	ГЩ-301		кламповое	соединение кламповое Ø50.5 (хомут AISI 304 с барашковой гайкой, прокладка PTFE)	23135	12811	+6,90
95	ГЩ-301		кламповое	соединение кламповое Ø50.5 (хомут AISI 304 с барашковой гайкой, прокладка PTFE)	23135	12811	+6,83
96	ГЩ-301		кламповое	соединение кламповое Ø50.5 (хомут AISI 304 с барашковой гайкой, прокладка PTFE)	22622	12811	+6,76
97	ГЩ-301		кламповое	соединение кламповое Ø50.5 (хомут AISI 304 с барашковой гайкой, прокладка PTFE)	22685	12811	+6,76
98	ГЩ-301		кламповое	соединение кламповое Ø50.5 (хомут AISI 304 с барашковой гайкой, прокладка PTFE)	22832	12811	+6,76
99	ГЩ-301		кламповое	соединение кламповое Ø50.5 (хомут AISI 304 с барашковой гайкой, прокладка PTFE)	22915	12811	+6,76
100	ГЩ-301		кламповое	соединение кламповое Ø50.5 (хомут AISI 304 с барашковой гайкой, прокладка PTFE)	23062	12811	+6,76
101	ГЩ-301		кламповое	соединение кламповое Ø50.5 (хомут AISI 304 с барашковой гайкой, прокладка PTFE)	23208	12811	+6,76
102	ГЩ-301		кламповое	соединение кламповое Ø50.5 (хомут AISI 304 с барашковой гайкой, прокладка PTFE)	23355	12811	+6,76
103	ГЩ-301		кламповое	соединение кламповое Ø50.5 (хомут AISI 304 с барашковой гайкой, прокладка PTFE)	23418	12811	+6,76
104	ГЩ-301		кламповое	соединение кламповое Ø50.5 (хомут AISI 304 с барашковой гайкой, прокладка PTFE)	23486	12811	+6,76
105	ГЩ-301		кламповое	соединение кламповое Ø50.5 (хомут AISI 304 с барашковой гайкой, прокладка PTFE)	22538	12815	+6,67
106	ГЩ-301		кламповое	соединение кламповое Ø50.5 (хомут AISI 304 с барашковой гайкой, прокладка PTFE)	22538	12829	+6,41
107	ГЩ-301	25	фланцевое	4 шпилек M12×73 с гайками (A2-70), прокладка PTFE (фторопласт-4)	22538	12810	+6,33
108	ГЩ-301/азот		кламповое	соединение кламповое Ø50.5 (хомут AISI 304 с барашковой гайкой, прокладка PTFE)	23282	12811	+6,68
109	ГЩ-301/азот		кламповое	соединение кламповое Ø50.5 (хомут AISI 304 с барашковой гайкой, прокладка PTFE)	23282	12811	+6,62
110	ГЩ-301/сброс		кламповое	соединение кламповое Ø64 (хомут AISI 304 с барашковой гайкой, прокладка PTFE)	22962	12788	+7,33
111	ГЩ-301/сброс		кламповое	соединение кламповое Ø50.5 (хомут AISI 304 с барашковой гайкой, прокладка PTFE)	22966	12788	+7,25
112	ГЩ-301/сброс		кламповое	соединение кламповое Ø50.5 (хомут AISI 304 с барашковой гайкой, прокладка PTFE)	22855	12811	+7,18
113	ГЩ-301/сброс		кламповое	соединение кламповое Ø50.5 (хомут AISI 304 с барашковой гайкой, прокладка PTFE)	22915	12811	+7,18
114	ГЩ-301/сброс		кламповое	соединение кламповое Ø50.5 (хомут AISI 304 с барашковой гайкой, прокладка PTFE)	22988	12811	+7,11
115	ГЩ-301/сброс		кламповое	соединение кламповое Ø50.5 (хомут AISI 304 с барашковой гайкой, прокладка PTFE)	22758	12811	+7,09
116	ГЩ-301/сброс		кламповое	соединение кламповое Ø50.5 (хомут AISI 304 с барашковой гайкой, прокладка PTFE)	22988	12811	+7,05
117	ГЩ-301/сброс		кламповое	соединение кламповое Ø50.5 (хомут AISI 304 с барашковой гайкой, прокладка PTFE)	22758	12811	+6,90
118	ГЩ-301/сброс		кламповое	соединение кламповое Ø50.5 (хомут AISI 304 с барашковой гайкой, прокладка PTFE)	22988	12811	+6,90
119	ГЩ-301/сброс		кламповое	соединение кламповое Ø50.5 (хомут AISI 304 с барашковой гайкой, прокладка PTFE)	22758	12811	+6,83
120	ГЩ-301/сброс		кламповое	соединение кламповое Ø50.5 (хомут AISI 304 с барашковой гайкой, прокладка PTFE)	22988	12811	+6,83

Изм.	Лист	№ докум.	Подп.	Дата
Разраб.				
Пров.				
Т.контр.				
Н.контр.				
Утв.				

ОПУ.ОБ.R-301.М.13

Реактор 1 м³ 904L (R-301):
ведомость соединений (3)

Лит.	Масса	Масштаб
П	—	б/м

Лист 13 | Листов 16

Опытно-промышленный участок

Опытно-промышленный участок

ВЕДОМОСТЬ ТОЧЕК СТЫКА И ГРАНИЦ УЗЛА

Линия / точка	DN	X, мм	Y, мм	Отм., м	Куда идёт (продолжение — общая модель)
312-25-PPR	25	21630	12550	+5,600	фланец общей трассы (N-301-25 (449), trassy/tochki.csv)
314-50-S	50	23350	12788	+2,102	сдувка вниз к V-308 и газоочистке — граница с трассой газоочистки
314-50-S	50	23504	17700	+8,890	сдувки R-301 и E-302 (гребёнка защиты на N9) в коллектор 901 — граница с …
317-50-PPR	50	21553	11018	+4,455	вода охлаждающая от чиллера на E-302 — граница с трассой воды 317
318-50-PPR	50	22111	12653	+6,908	вода охлаждающая с E-302 обратно к чиллеру — граница с трассой воды 318
324-25-PPR	25	21450	15000	+2,100	азот на центрифугу X-306 (инертизация) — граница с трассой азота (коллект…
325-50-CS	50	20700	16778	+2,150	термомасло подача от термостата X-304 (трасса +2.150, сталь 20) — граница…
326-50-CS	50	20700	16778	+1,950	термомасло возврат к термостату X-304 (трасса +1.950, сталь 20) — граница…
327-25-PTFE	25	22538	10494	+6,288	вакуум: рукав 1″ PTFE от объединяющего блока (магистрали V-805 / V-806) —…
335-25-PPR	25	23097	8668	+4,499	азот 4 бар на X-303 N3: выдавливание отгона по 304 — граница с трассой аз…
X-303 N4	25	22170	10023	+3,360	вакуум: рукав 1″ PTFE от объединяющего блока (кран K50,5 «на ресивер») — …
ГЗ-301/ECH	25	21636	14650	+4,278	вход «ЭХГ»: кламп K50,5 вверх, хомут на штуцер рукава K50,5 от насоса P-1…
ГЗ-301/P2	25	21636	14490	+4,278	вход «DEA / CDEA от точных весов (насос P-2)»: кламп K50,5 вверх, хомут н…
СВ-301	20	20750	9000	+1,900	стык с магистралью воздуха КИП IA-20 (узел X-500 / общая трасса) — сжатый…
СВ-301 → блок подготовки воздуха …	15	23328	15000	+1,800	СВ-301 → блок подготовки воздуха насоса поста дозирования (узел «загрузка…
СВ-301 → блок подготовки воздуха …	20	20922	17400	+1,800	СВ-301 → блок подготовки воздуха насоса поста дозирования (узел «загрузка…

Изм.	Лист	№ докум.	Подп.	Дата	ОПУ.ОБ.R-301.М.14			
Разраб.					**Реактор 1 м³ 904L (R-301):** ведомость точек стыка и границ узла	Лит.	Масса	Масштаб
Пров.						П	—	б/м
Т.контр.						Лист 14		Листов 16
Н.контр.					Опытно-промышленный участок	**Опытно-промышленный участок**		
Утв.								

ВЕДОМОСТЬ АРМАТУРЫ И КИП

Тег	Наименование	Линия	X, мм	Y, мм	Отм., м
АР-1	PCV R-301 — редуктор давления азота с манометром, G1/2, AISI 316	ГЩ-301/азот	23282	12788	+6,21
АР-2	шпунт-аппарат угловой с манометром К50,5 (0,2…2,2 бар, гильза со шкалой; манометр 0…4 бар на разделителе), AISI 304, EPDM — каталог R-301	ГЩ-301/сброс	22806	12788	+7,14
ВН-1	клапан запорный (вентиль) фланцевый DN50 PN16 AISI 316L, сильфонное уплотнение штока (EN 558 сер.1) — 302Ф: у реактора	302Ф-50-SS	22538	12959	+3,83
ВН-2	вентиль запорно-регулирующий PP-R d63 PN20 (PPRF/SV) — 317	317-50-PPR	22318	11018	+4,45
ЗД-1	кран-бабочка (затвор дисковый) под кламп 2″ (К63), AISI 304, рукоятка с фиксатором — каталог — вход «резерв»	ГЗ-301	21636	14330	+4,17
ЗД-2	кран-бабочка (затвор дисковый) под кламп 2″ (К63), AISI 304, рукоятка с фиксатором — каталог — вход «DEA / CDEA от точных весов (насос Р-2)»	ГЗ-301	21636	14490	+4,17
ЗД-3	кран-бабочка (затвор дисковый) под кламп 2″ (К63), AISI 304, рукоятка с фиксатором — каталог — вход «ЭХГ»	ГЗ-301	21636	14650	+4,17
ЗД-4	кран-бабочка (затвор дисковый) под кламп 1½″ (К50,5), AISI 304, рукоятка с фиксатором — каталог R-301 — перед мановакуумметром	ГЩ-301	23135	12788	+6,86
ЗД-5	кран-бабочка (затвор дисковый) под кламп 1½″ (К50,5), AISI 304, рукоятка с фиксатором — каталог R-301 — сброс на атмосферу	ГЩ-301	23452	12788	+6,76
ЗД-6	кран-бабочка (затвор дисковый) под кламп 1½″ (К50,5), AISI 304, рукоятка с фиксатором — каталог R-301 — ввод азота (азотная подушка)	ГЩ-301/азот	23282	12788	+6,65
ЗД-7	кран-бабочка (затвор дисковый) под кламп 1½″ (К50,5), AISI 304, рукоятка с фиксатором — каталог R-301 — перед шпунт-аппаратом	ГЩ-301/сброс	22758	12788	+6,86
ЗД-8	кран-бабочка (затвор дисковый) под кламп 1½″ (К50,5), AISI 304, рукоятка с фиксатором — каталог R-301 — перед обратным клапаном аварийного сброса (за…	ГЩ-301/сброс	22988	12788	+6,86
КТ-1	кран шаровой трёхходовой фланцевый DN80 PN16 AISI 316L/PTFE, L-проход, редуктор с маховиком — 302: в сборник Х-303 / флегма 302Ф в реактор (по схеме …	302-80-SS	22538	9655	+3,96
КШ-1	кран шаровой фланцевый DN25 PN16 AISI 316L/PTFE, полнопроходной (EN 558 сер.27) — 302Д: дренаж гидрозатвора	302Д-25-SS	22538	11407	+3,45
КШ-2	кран шаровой фланцевый DN25 PN25 AISI 316L/PTFE, полнопроходной (EN 558 сер.27) — 303: дренаж Е-302 N7	303-25-SS	22538	12881	+4,99
КШ-3	кран шаровой фланцевый DN25 PN25 AISI 316L/PTFE, полнопроходной (EN 558 сер.27) — 303: дренаж Е-302 N8	303-25-SS	22538	10562	+4,99
КШ-4	кран шаровой полипропиленовый PP-R d32 PN20 — 312, азот на гребёнку защиты ГЩ-301	312-25-PPR	23282	12788	+6,01
КШ-5	кран шаровой полипропиленовый PP-R d32 PN20 — 324 (азот на Х-306)	324-25-PPR	21450	14475	+2,10
КШ-6	кран шаровой фланцевый DN25 PN16 AISI 316L/PTFE, полнопроходной (EN 558 сер.27) — 335 (азот 4 бар)	335-25-PPR	22248	9733	+3,73
КШ-7	кран шаровой фланцевый DN25 PN10 AISI 316L/PTFE, полнопроходной (EN 558 сер.27) — Е-302 N5	Е-302 N5	22688	12525	+5,53
КШ-8	кран шаровой фланцевый DN25 PN10 AISI 316L/PTFE, полнопроходной (EN 558 сер.27) — Е-302 N6	Е-302 N6	22538	10788	+6,29
КШ-9	кран шаровой фланцевый DN50 PN10 AISI 316L/PTFE, полнопроходной (EN 558 сер.27) — слив отгона Х-303 В (в еврокуб рукавом по месту)	Х-303/слив	22460	9945	+1,32
КШ-10	кран шаровой фланцевый DN100 PN16 AISI 316L/PTFE, полнопроходной (EN 558 сер.27) — слив фильтрата Х-306	Х-306/фильтрат	21001	12998	+0,66
КШ-11	Р-305: блок подготовки воздуха — кран шаровой G½″, фильтр-регулятор с манометром (Ex), выход G½″	СВ-305			
КШ-12	Р-306: блок подготовки воздуха — кран шаровой G½″, фильтр-регулятор с манометром (Ex), выход G½″	СВ-306			
КШМ-1	кран шаровой муфтовый полнопроходной G2 (ВР-ВР), PN16 317, Е-302 N3	317-50-PPR	22538	10858	+4,97
КШМ-2	кран шаровой муфтовый DN15 (G1/2) AISI 316/PTFE, PN40 — 317 (слив)	317-50-PPR	22092	11018	+4,32
КШМ-3	кран шаровой муфтовый полнопроходной G2 (ВР-ВР), PN16 318, Е-302 N4	318-50-PPR	22538	12479	+6,43
КШМ-4	кран шаровой муфтовый DN15 (G1/2) AISI 316/PTFE, PN40 — 318 (воздушник)	318-50-PPR	22382	12653	+7,05
КШМ-5	кран шаровой муфтовый DN15 (G1/2) AISI 316/PTFE, PN40 — дренаж 325 (у границы) (G1/2)	325-50-CS	21000	16778	+2,02
КШМ-6	кран шаровой муфтовый DN15 (G1/2) AISI 316/PTFE, PN40 — дренаж 326 (нижняя точка у границы) (G1/2)	326-50-CS	21000	16778	+1,82
КШМ-7	кран шаровой муфтовый DN15 (G1/2) AISI 316/PTFE, PN40 — g (воздушник рубашки)	рубашка g	22460	14750	+2,89
КШМ-8	кран шаровой муфтовый DN15 (G1/2) AISI 316/PTFE, PN40 — k (дренаж рубашки)	рубашка k	22306	13577	+1,91
ОК-1	клапан обратный подъёмный фланцевый DN25 PN16 AISI 316L (EN 558 сер.1) — 335 (азот 4 бар)	335-25-PPR	22248	9733	+3,58
ОК-2	клапан обратный пружинный К50,5 с клампами (AISI 316L / PTFE), поток → R-301 — аварийный сброс	ГЩ-301/сброс	22988	12788	+6,98

Изм.	Лист	№ докум.	Подп.	Дата
Разраб.				
Пров.				
Т.контр.				
Н.контр.				
Утв.				

ОПУ.ОБ.R-301.М.15

Реактор 1 м³ 904L (R-301):
ведомость арматуры и кип

Лит.	Масса	Масштаб
П	—	б/м

Лист 15 | Листов 16

Опытно-промышленный участок

Опытно-промышленный участок

УСЛОВНЫЕ ОБОЗНАЧЕНИЯ


Потоки (цвет линии)

- сырьё и загрузка
- пары (реактор → конденсатор)
- конденсат и флегма
- продукт, слив реактора
- дренажи
- аварийный сброс
- вакуум
- азот
- сжатый воздух
- сдувки и дыхание
- вода охлаждающая (оборотная)
- теплоноситель — масло
- рукав (цвет — по потоку)
- очертания аппаратов — проекция 3D-модели
- внутренние устройства (мешалки, вал, гильза, перегородки)
- 12 — номер соединения (ведомость соединений)

Символы (ГОСТ 2.785, ГОСТ 21.206)



кран, вентиль, клапан запорный

 

клапан обратный (по потоку)

конец линии: штуцер, точка стыка, граница, заглушка



рабочий уровень в аппарате

Сокращение	Что это
КШ	кран шаровой фланцевый
КШК	кран шаровой санитарный (кламп К63 / К25)
АР	прочая арматура: шпунт-аппарат, редуктор
КШМ	кран шаровой муфтовый
ОК	клапан обратный
ВН	вентиль (клапан запорный)
КТ	кран трёхходовой
КД	клапан донный F41
КИ	клапан игольчатый
PIR, TIRA, LIRA	контуры АСУ ТП: давление, температура, уровень
PI	манометр (мановакуумметр) показывающий
ГЗ-301	гребёнка загрузки (К63, входы К25)
ГЩ-301	гребёнка защиты (К25)
N1…N10, T, B, M, L1…L4	штуцеры аппаратов (по чертежам поставщика)

Изм.	Лист	№ докум.	Подп.	Дата	ОПУ.ОБ.R-301.M.16			
Разраб.					Условные обозначения монтажных	Лит.	Масса	Масштаб
Пров.					листов	П	—	б/м
Т.контр.						Лист 16		Листов 16
Н.контр.					Опытно-промышленный участок	Опытно-промышленный участок		
Утв.								