




Наименование	Комп.	Единиц
Р-1	Ремкомплект Wiggins 50 л (усл.)	1
С-1	Конфигуратор маршрутов	1
W-1	Воды 12,5 л + моет. NaOH, + FOMS-CH	1
G-1	Пеностроитель без Аппарат ЕК-40	1
V-1	Каннестра 3-ра металамина	1
P-1	Насос мопер. пневм. (до P=2)	1
С-1	Каннестра, сит. 20-1,8 м СН60-600	1
C-2	Каннестра, сит. 20-1,8 м СН60-600	1
C-2	Каннестра, NaOH +2,7 м СН60-600	1
AB-1	Баллон AB 40 л	1
AB-1	Ремонт и стачивание металамина, до -10 мм	1
K-40	Каннестра	4
С-1	Штанг-аппарат + манометры	1
NPV-1	Каннестра обфран. сит. DN15, С30 мбар	1
FSV-1	Каннестра, пневм. 1/2, 3,6 м	1
SV-1, 3, AV-1	Каннестра (насос DN15 (проток))	1
V-1	Каннестра (насос DN15 (проток))	1
PU-1, 4	Манометры	4
PU-1, 4	Манометры	4
PU-1, 4	Манометры	4
T-1	Будильная система 23 л	1
T-1	Сирена 20 л	1
CP-1	Насос вакуумный мембранный	1
CT-1	Сепаратор вакуумный	1
CT-1	Чаша	1
NPV-1	Каннестра пневм. воды	1
CVX	Каннестра металамина	2
C-1	Насос мопер. пневм. (проток)	1
C-1	Насос мопер. пневм. (удержание)	1
P-1	Нут-СН600 (7) под каннестру	1
FSV-4	Сборный каннестра нутча 0,3 м	1
W-1, 4	Каннестра для чистки 1,2 м	1
W-1, 4	Воды	4
NPV-3	Обр. каннестра 3-х мбар (под газ)	1
NPV-3	Препор. каннестра AB 1/4-1	1

Примечания


1. Схема в сборе без масштаба; Е-1, колонны – в едином условном масштабе -1:5. Детали – листы 2-7, ведомость клапнов – лист 8
2. Все размеры «?» (расстояния между аппаратами, высоты, длины руковок и т.п., присоединения) – уточнить по месту.
3. Прокладки: PTFE – продукт, растворители, газ, EPDM – только водные/щелочные линии генератора. Хомуты клапанные – нерж.
4. Штросовые линии бирюзового цвета – теплоносители; штросовые черные – гибкие рукава; тонкие сплошные – трубки PTFE 7/10-12

				ИНУМ.770-50.00.01		
Лист	Лист	№ докум.	Подп.	Дата		
Разработ	Установка синтеза ТЕФКОТ 770 на реакторе 50 л. Монтажная схема в сборе			Лист	Масшта	Масштаб
Проект				П	—	б/м
Техниче				Лист 1		Листов 8
Исполне						
Утв.				АО «ИНУМит»		
				ТЕФКОТ 770 - реактор 50 л		

РЕАКТОР R-1 (Wiggins, 50 л) — ВИД СПЕРЕДИ

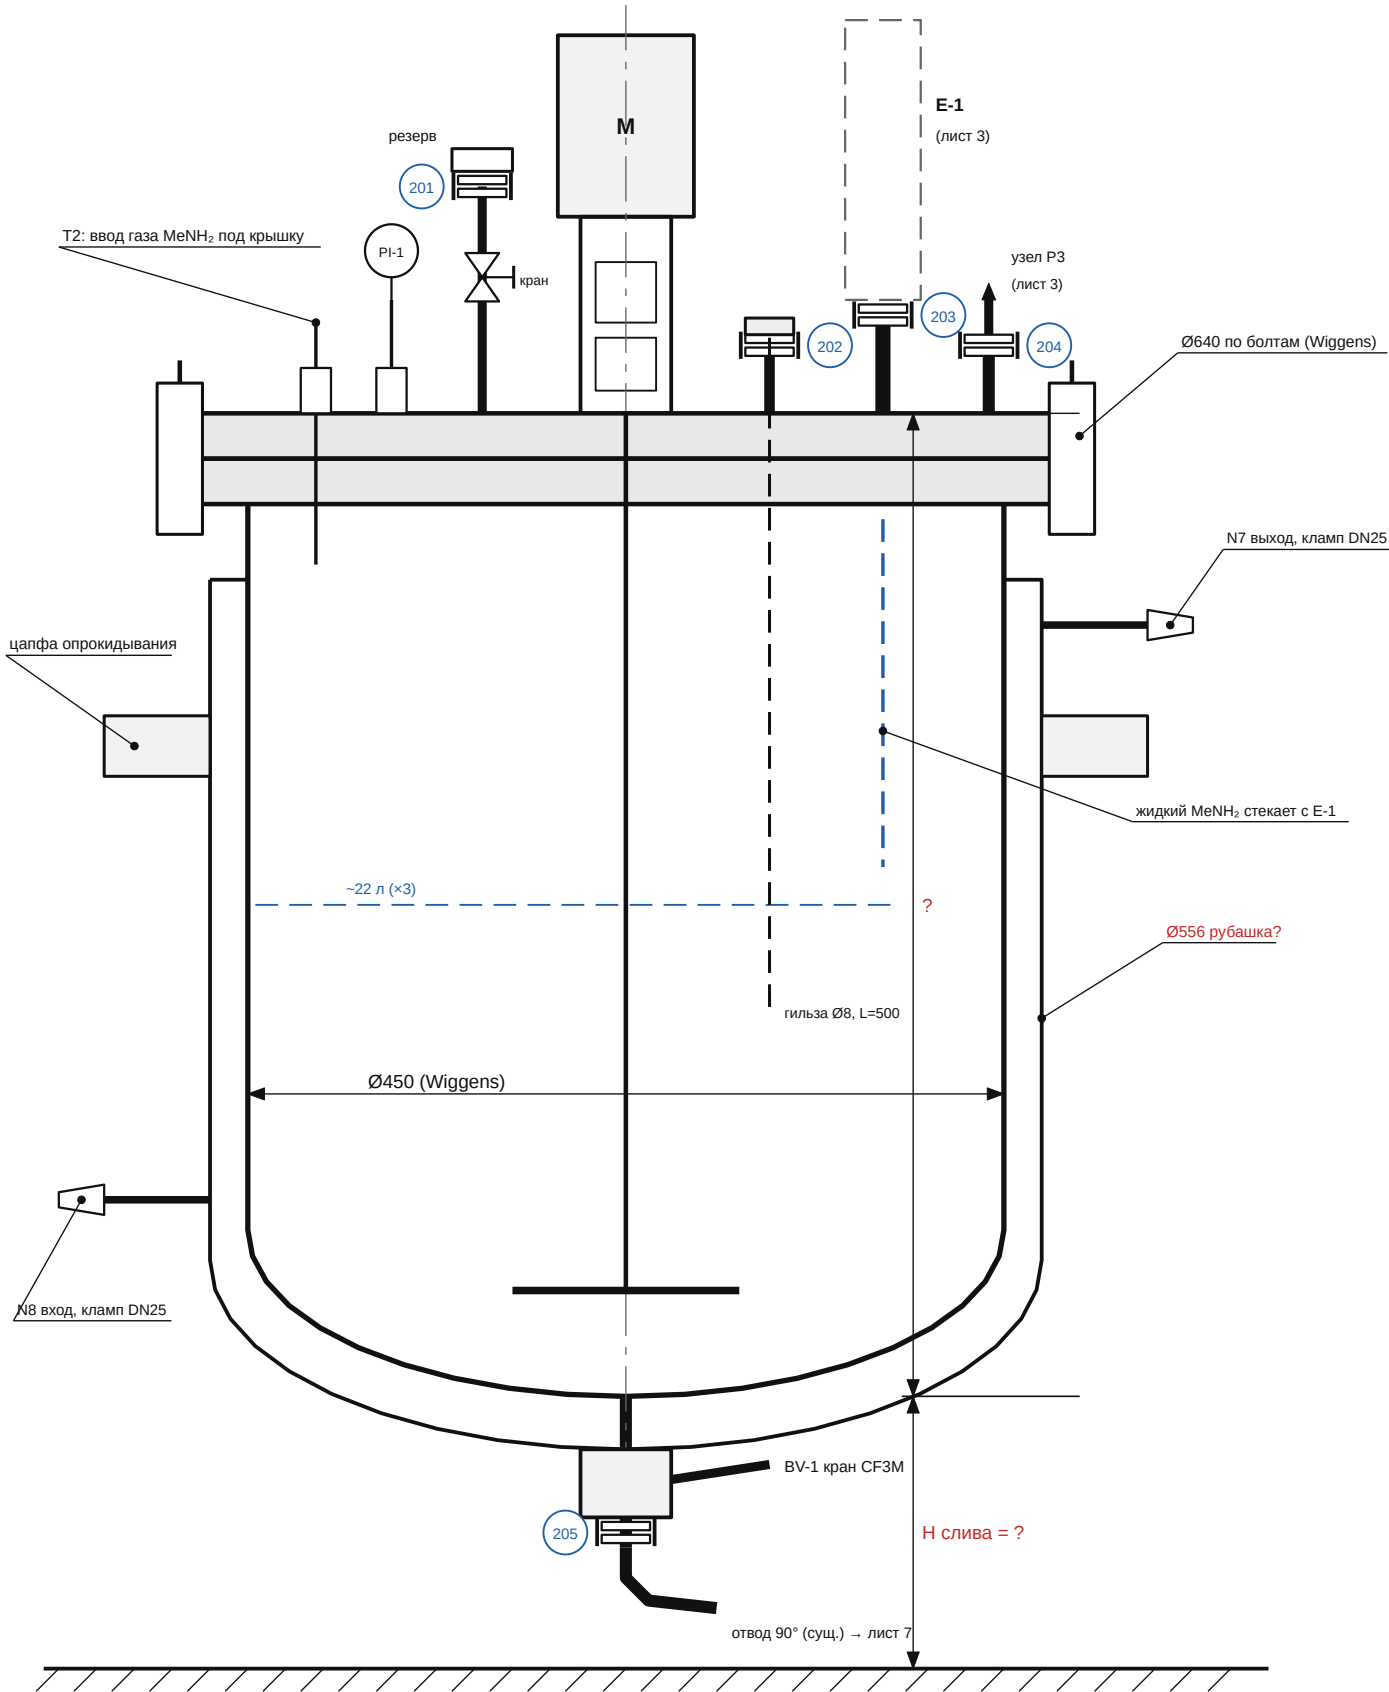

КРЫШКА R-1 — ВИД СВЕРХУ (по черт. Wiggins 8813650C)

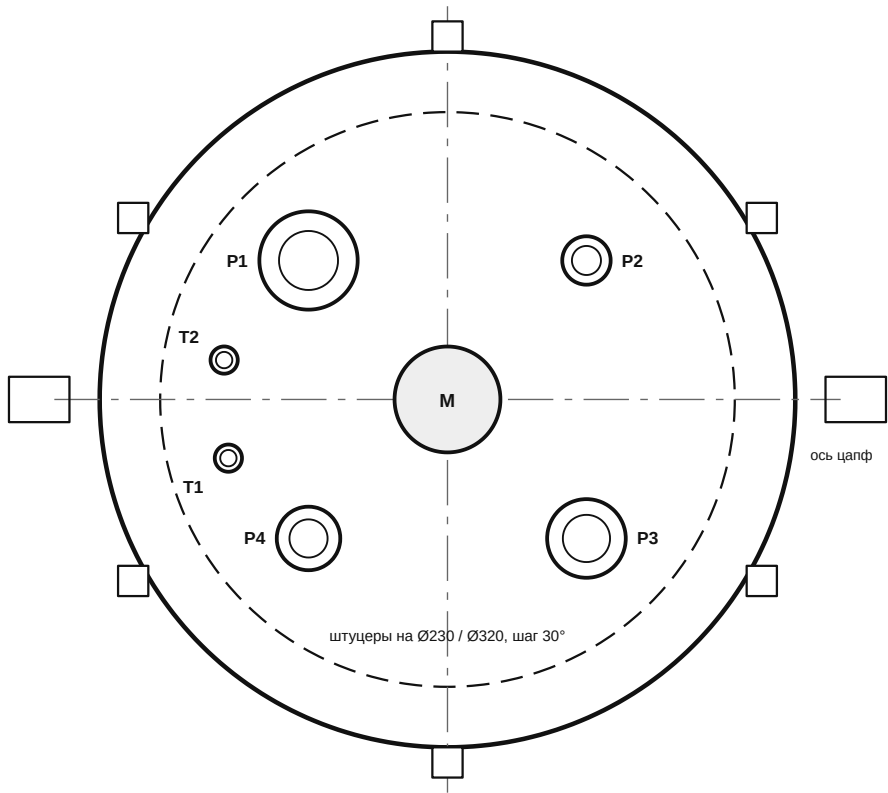

ФРОНТ (сторона оператора) ↓
откидные болты по Ø640; привязку N1...N6 к P1...T2 сверить

ТАБЛИЦА ШТУЦЕРОВ R-1

Обозн.	Wiggins	Назначение (у нас)	Присоед.: чертёж / фото	DN	Что устанавливается
P1	N3	конденсатор E-1	кламп Ø50,5	25	E-1 (лист 3)
P2	N4	термогильза T1 (Pt100)	кламп Ø50,5	25	заглушка DN25 с гильзой Ø8×500
P3	N5	дозирование P-3 (был рН)	кламп Ø50,5	25	узел P3 (лист 3)
P4	N1	ввод Ar (A1), резерв	кламп Ø50,5	25	заглушка + обжим ¼"
T1	N2	мановакуумметр P1-1	обжим ¼"	8	существующий
T2	N6	ввод газа MeNH ₂ под крышку	игольч. вентиль	8	без погружной трубки
M	M	мешалка, мотор WB400	фланец	133	существующая, вал Ø26
BV-1	L	нижний слив	кламп Ø50,5	38	тройник + SP-1 (лист 7)
JI/JO	N8/N7	рубашка вход / выход	кламп Ø50,5	25	переходник кламп – ёлочка
—	—	разъём крышки	откидные болты	Ø640	кольцо в оболочке FEP

Примечания

- Размеры «?» — уточнить замером.
Wiggins: Н общ. 1140, 414, 410.
- Ø ферулы кламп по DN: DN15 («к25») — 25; DN25, DN38 — 50,5; DN40 — 64; DN65 (3") — 91; DN100 (4") — 119.
- Шильдик: Р раб., полный вакуум, материал корпуса (нужен 316L).
- Проверить тип уплотнения вала.
- Дыхательный фильтр со стояка P4 снять (не стоек к р-лю).
- Все прокладки в контакте с продуктом — PTFE. PN всех — 0,5.
- Все штуцеры — трикламп; DN по DIN 11851 (Wiggins). DN25 и DN38 — ферула Ø50,5.


Условные обозначения:
—II— кламповое соединение, № — ведомость (лист 8)
— гибкий рукав; — тонкая — трубка ¼" / 12 мм
красным «?» — уточнить замером / у поставщика

					ИНУМ.770-50.00.02			
Изм.	Лист	№ докум.	Подп.	Дата				
Разраб.					Реактор R-1. Общий вид, штуцеры	Лит.	Масса	Масштаб
Пров.						П	—	б/м
Т.контр.								
Н.контр.						Лист 2		Листов 8
Утв.					ТЕФКОТ 770 · реактор 50 л	АО «ИНУМИТ»		

Е-1 КОНДЕНСАТОР ЗМЕЕВИКОВЫЙ (изгот.), М 1:3

ПОДАЧА MeSiCl_3 / PDMS-ОН НАСОСОМ Р-3, б/м


УЗЕЛ Р3, б/м

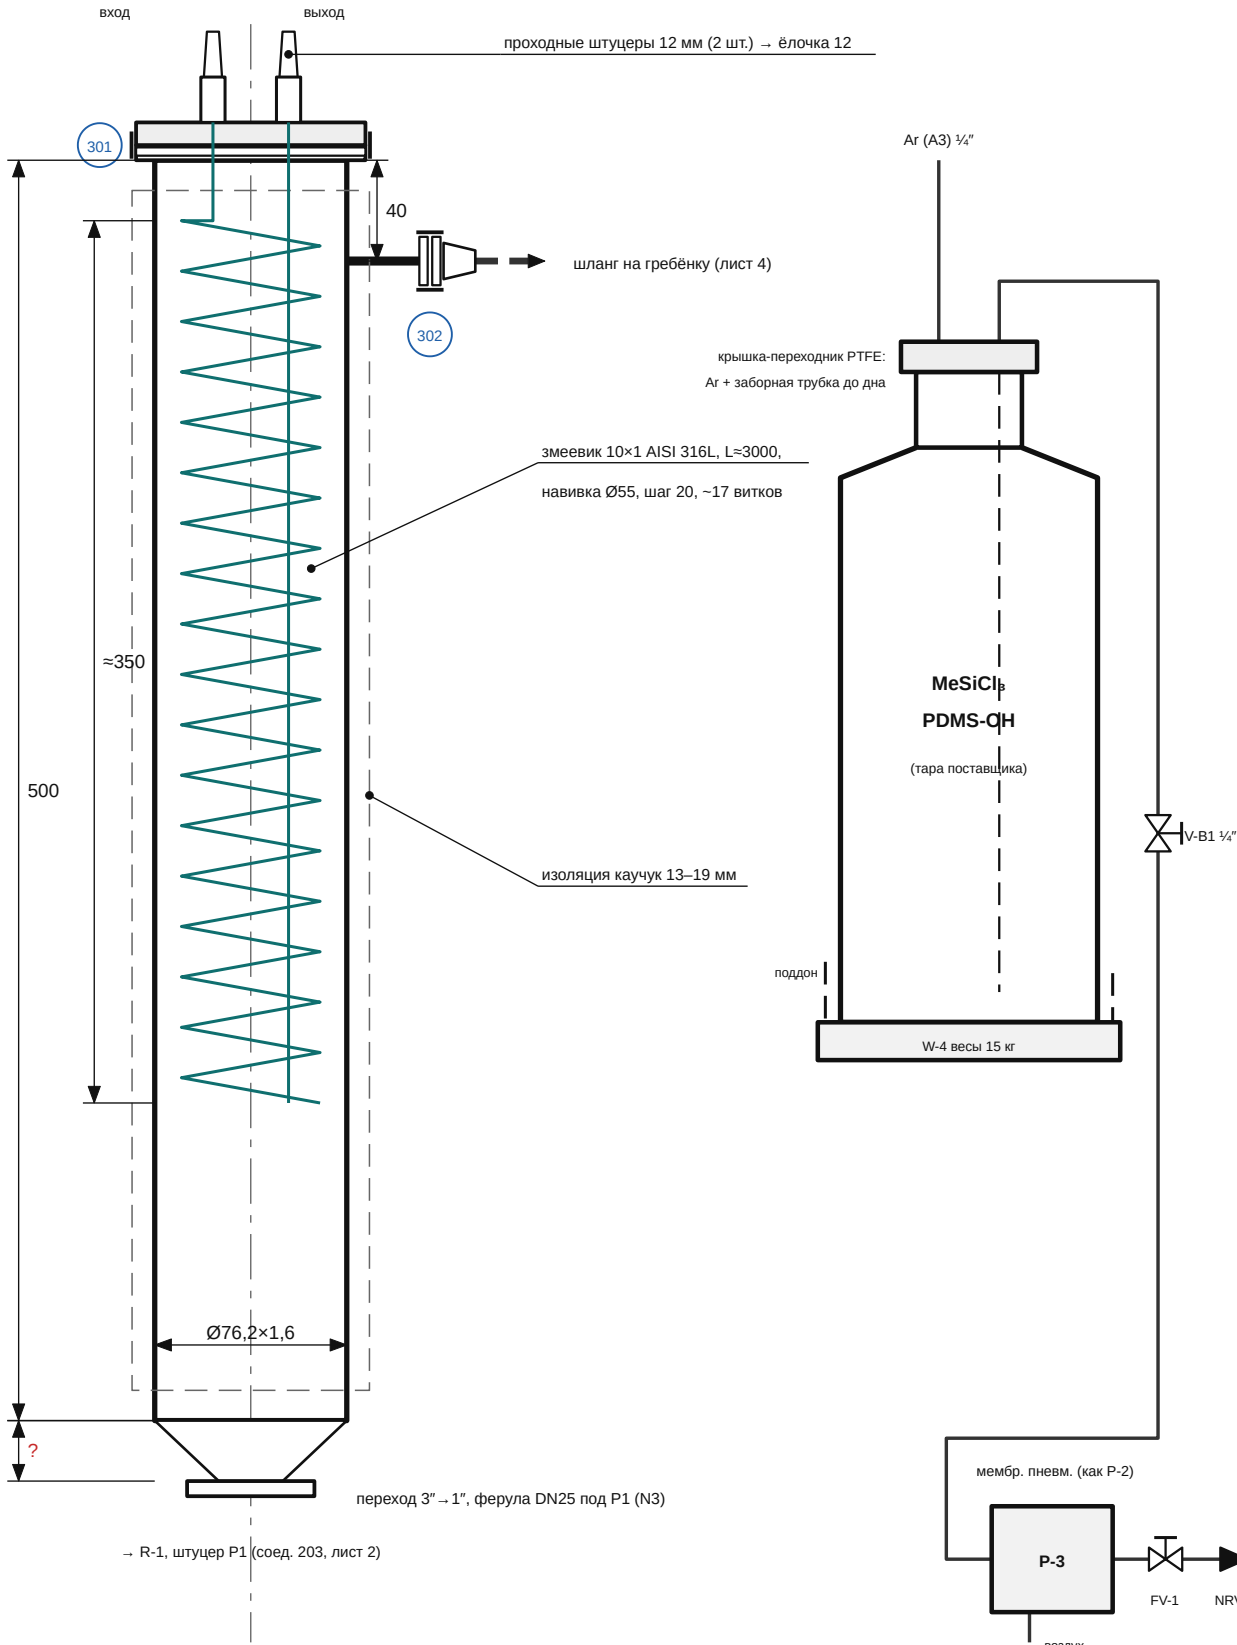


Примечания

- Е-1 — сталь AISI 316L; сварка TIG, пищевая полировка внутр. поверхности.
- Змеевик Е-1: опрессовка 3 бар (теплонос.).
- Е-1 вертикально: конденсат стекает в R-1.
- Теплоноситель Е-1: от ТС-1 (–25 °С); на стадии 7 — ледяная вода IW-1.
- Строительные длины кранов, тройников, переходов — по каталогу Гросснер (?).
- Все прокладки кламп — PTFE.
- MeSiCl_3 / PDMS-ОН — насосом Р-3 прямо из тары на W-4; объем замещается Ar (A3). Расход по W-4, темп — по T1 (≤ -10 °С).


УЗЕЛ Р2 (T1), б/м

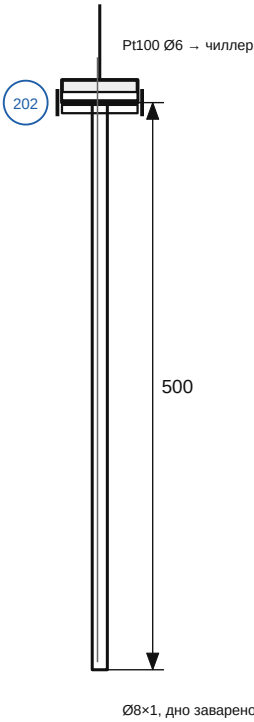

УЗЕЛ Р4 (резерв), б/м

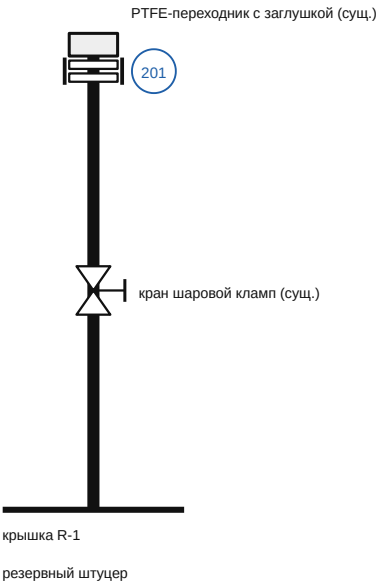


					ИНУМ.770-50.00.03			
Изм.	Лист	№ докум.	Подп.	Дата	Конденсатор Е-1, подача Р-3, узлы Р2, Р3, Р4	Лит.	Масса	Масштаб
Разраб.						П	—	б/м
Пров.								
Т.контр.								
Н.контр.						Лист 3		Листов 8
Утв.					ТЕФКОТ 770 · реактор 50 л		АО «ИНУМИТ»	

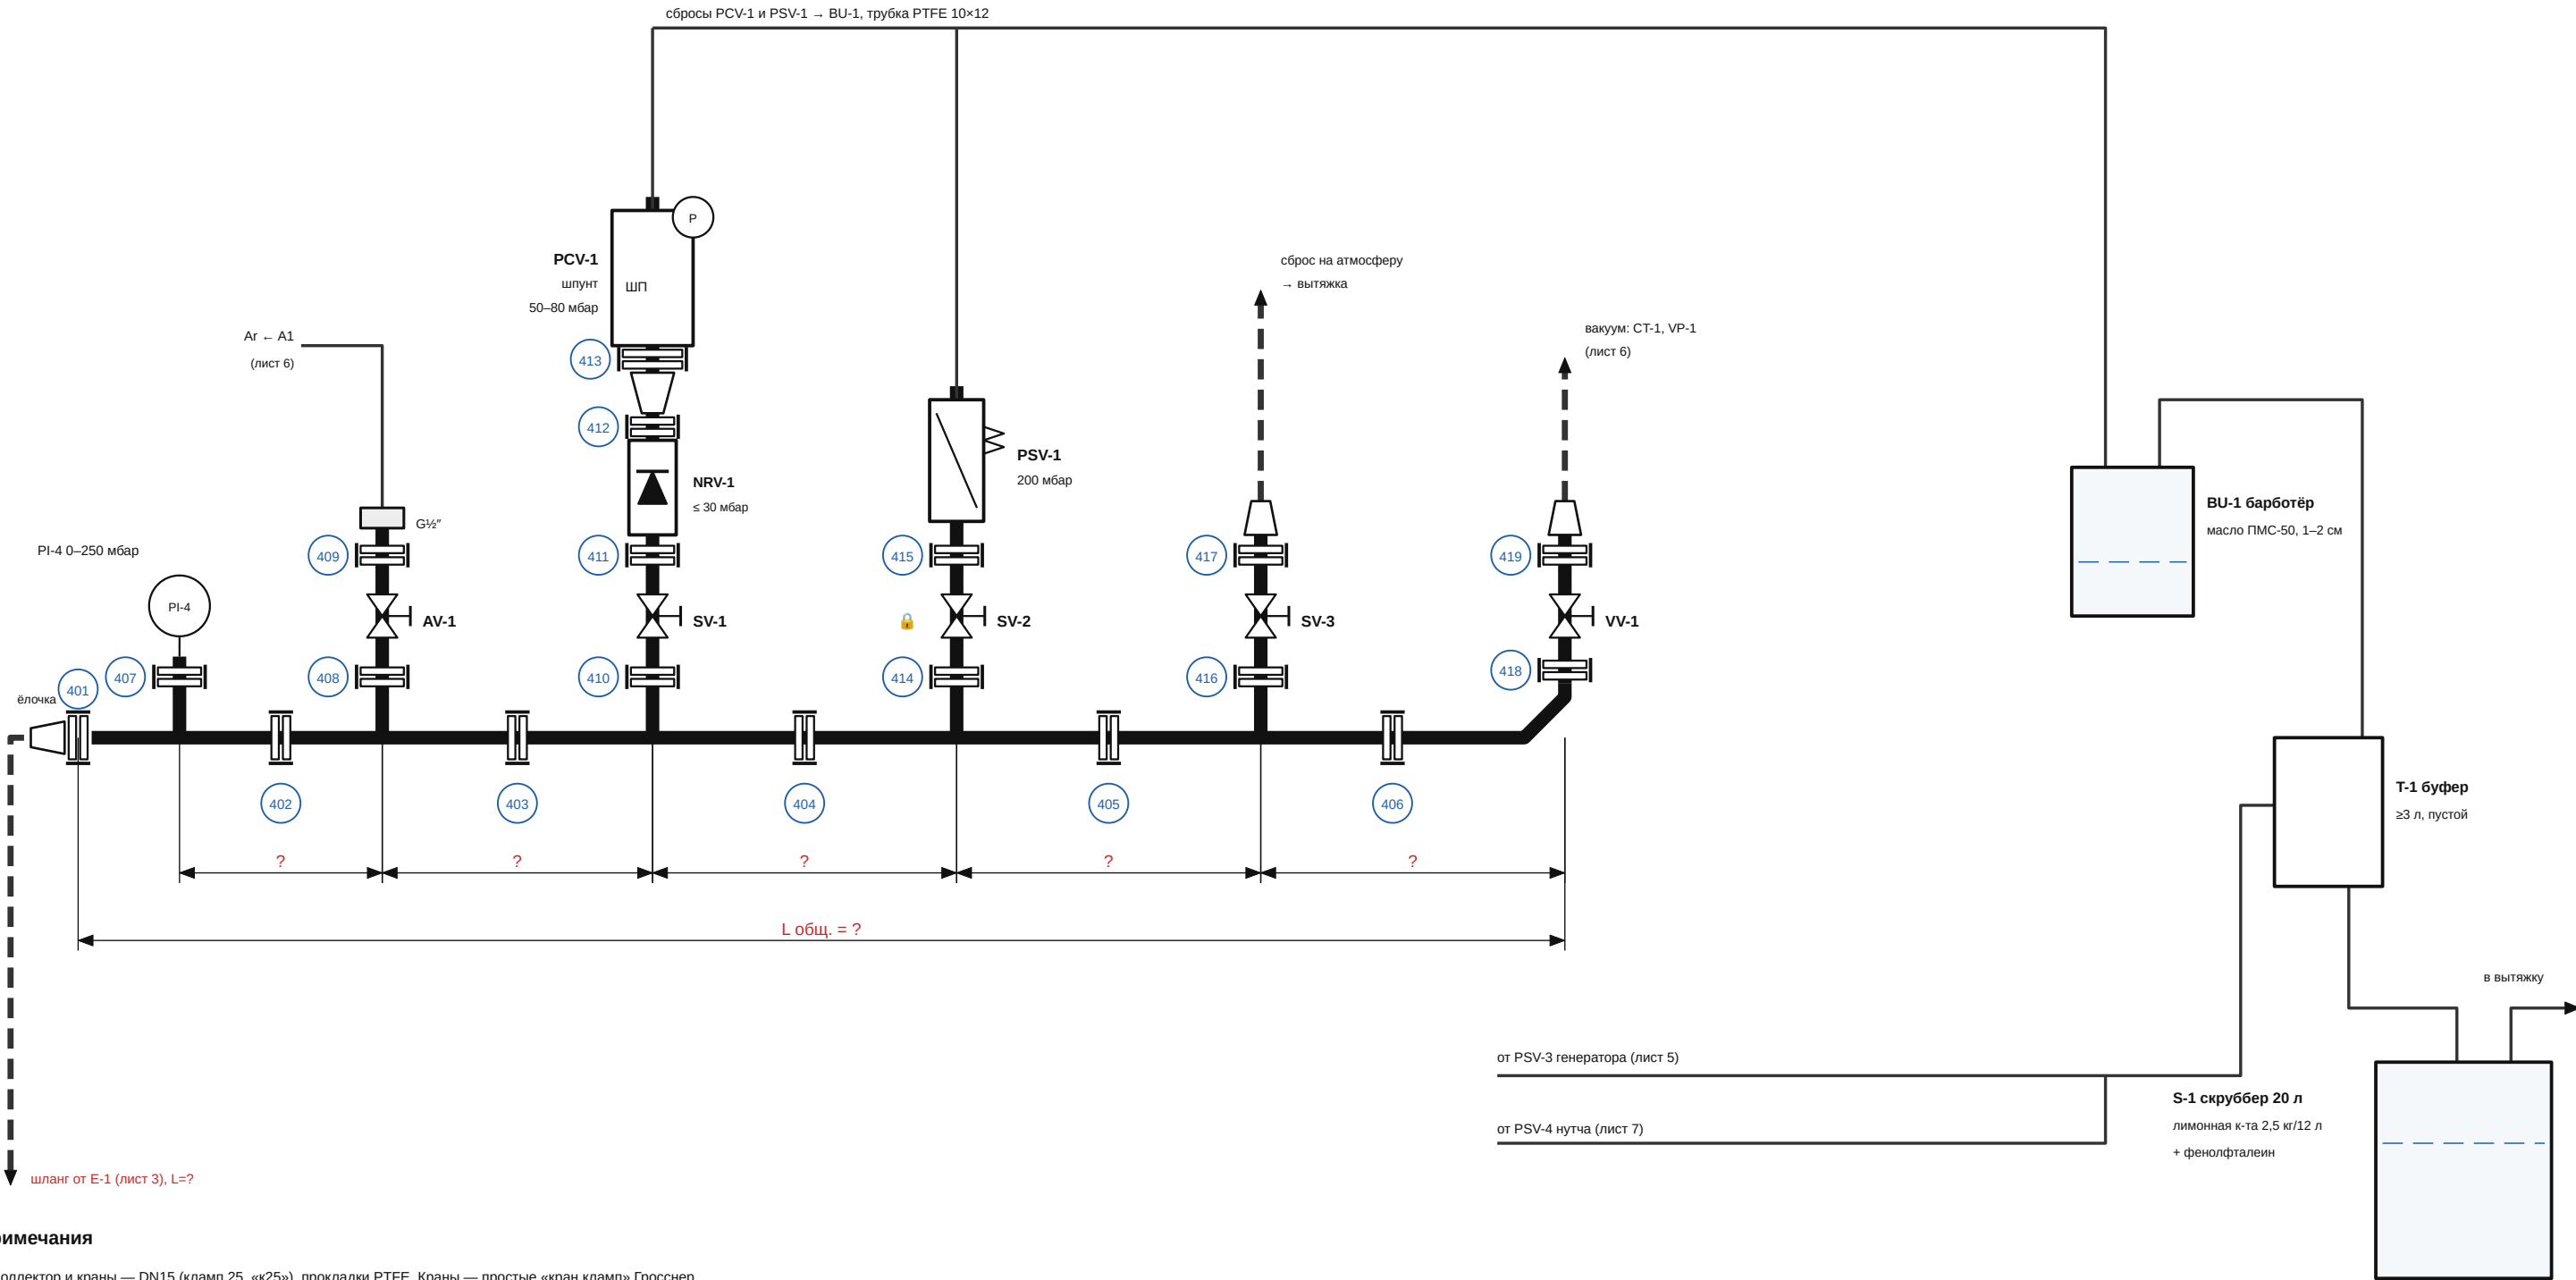

Примечания

- Коллектор и краны — DN15 (кламп 25, «к25»), прокладки PTFE. Краны — простые «кран кламп» Гросснер.
- Переход DN15/DN25 (25/50,5) только у шпунт-аппарата; отвод E-1 сразу DN15.
- SV-2 опломбирован «открыт»; закрывать только при вакуумировании. SV-3 открывать только при P ≥ 0.
- Гребёнка отдельно, на уголках к раме Wiggins; к E-1 — шлангом на ёлочках (или 1/2"). Место — по месту.
- Порядок веток и шаг тройников — по строительным длинам кранов (?).

					ИНУМ.770-50.00.04			
Изм.	Лист	№ докум.	Подп.	Дата	Гребёнка: шпунт, сброс, вакуум, аргон, атмосфера			
Разраб.								
Пров.								
Т.контр.								
Н.контр.								
Утв.					Лист 4			
					Листов 8			
					ТЕФКОТ 770 · реактор 50 л			
					АО «ИНУМиТ»			

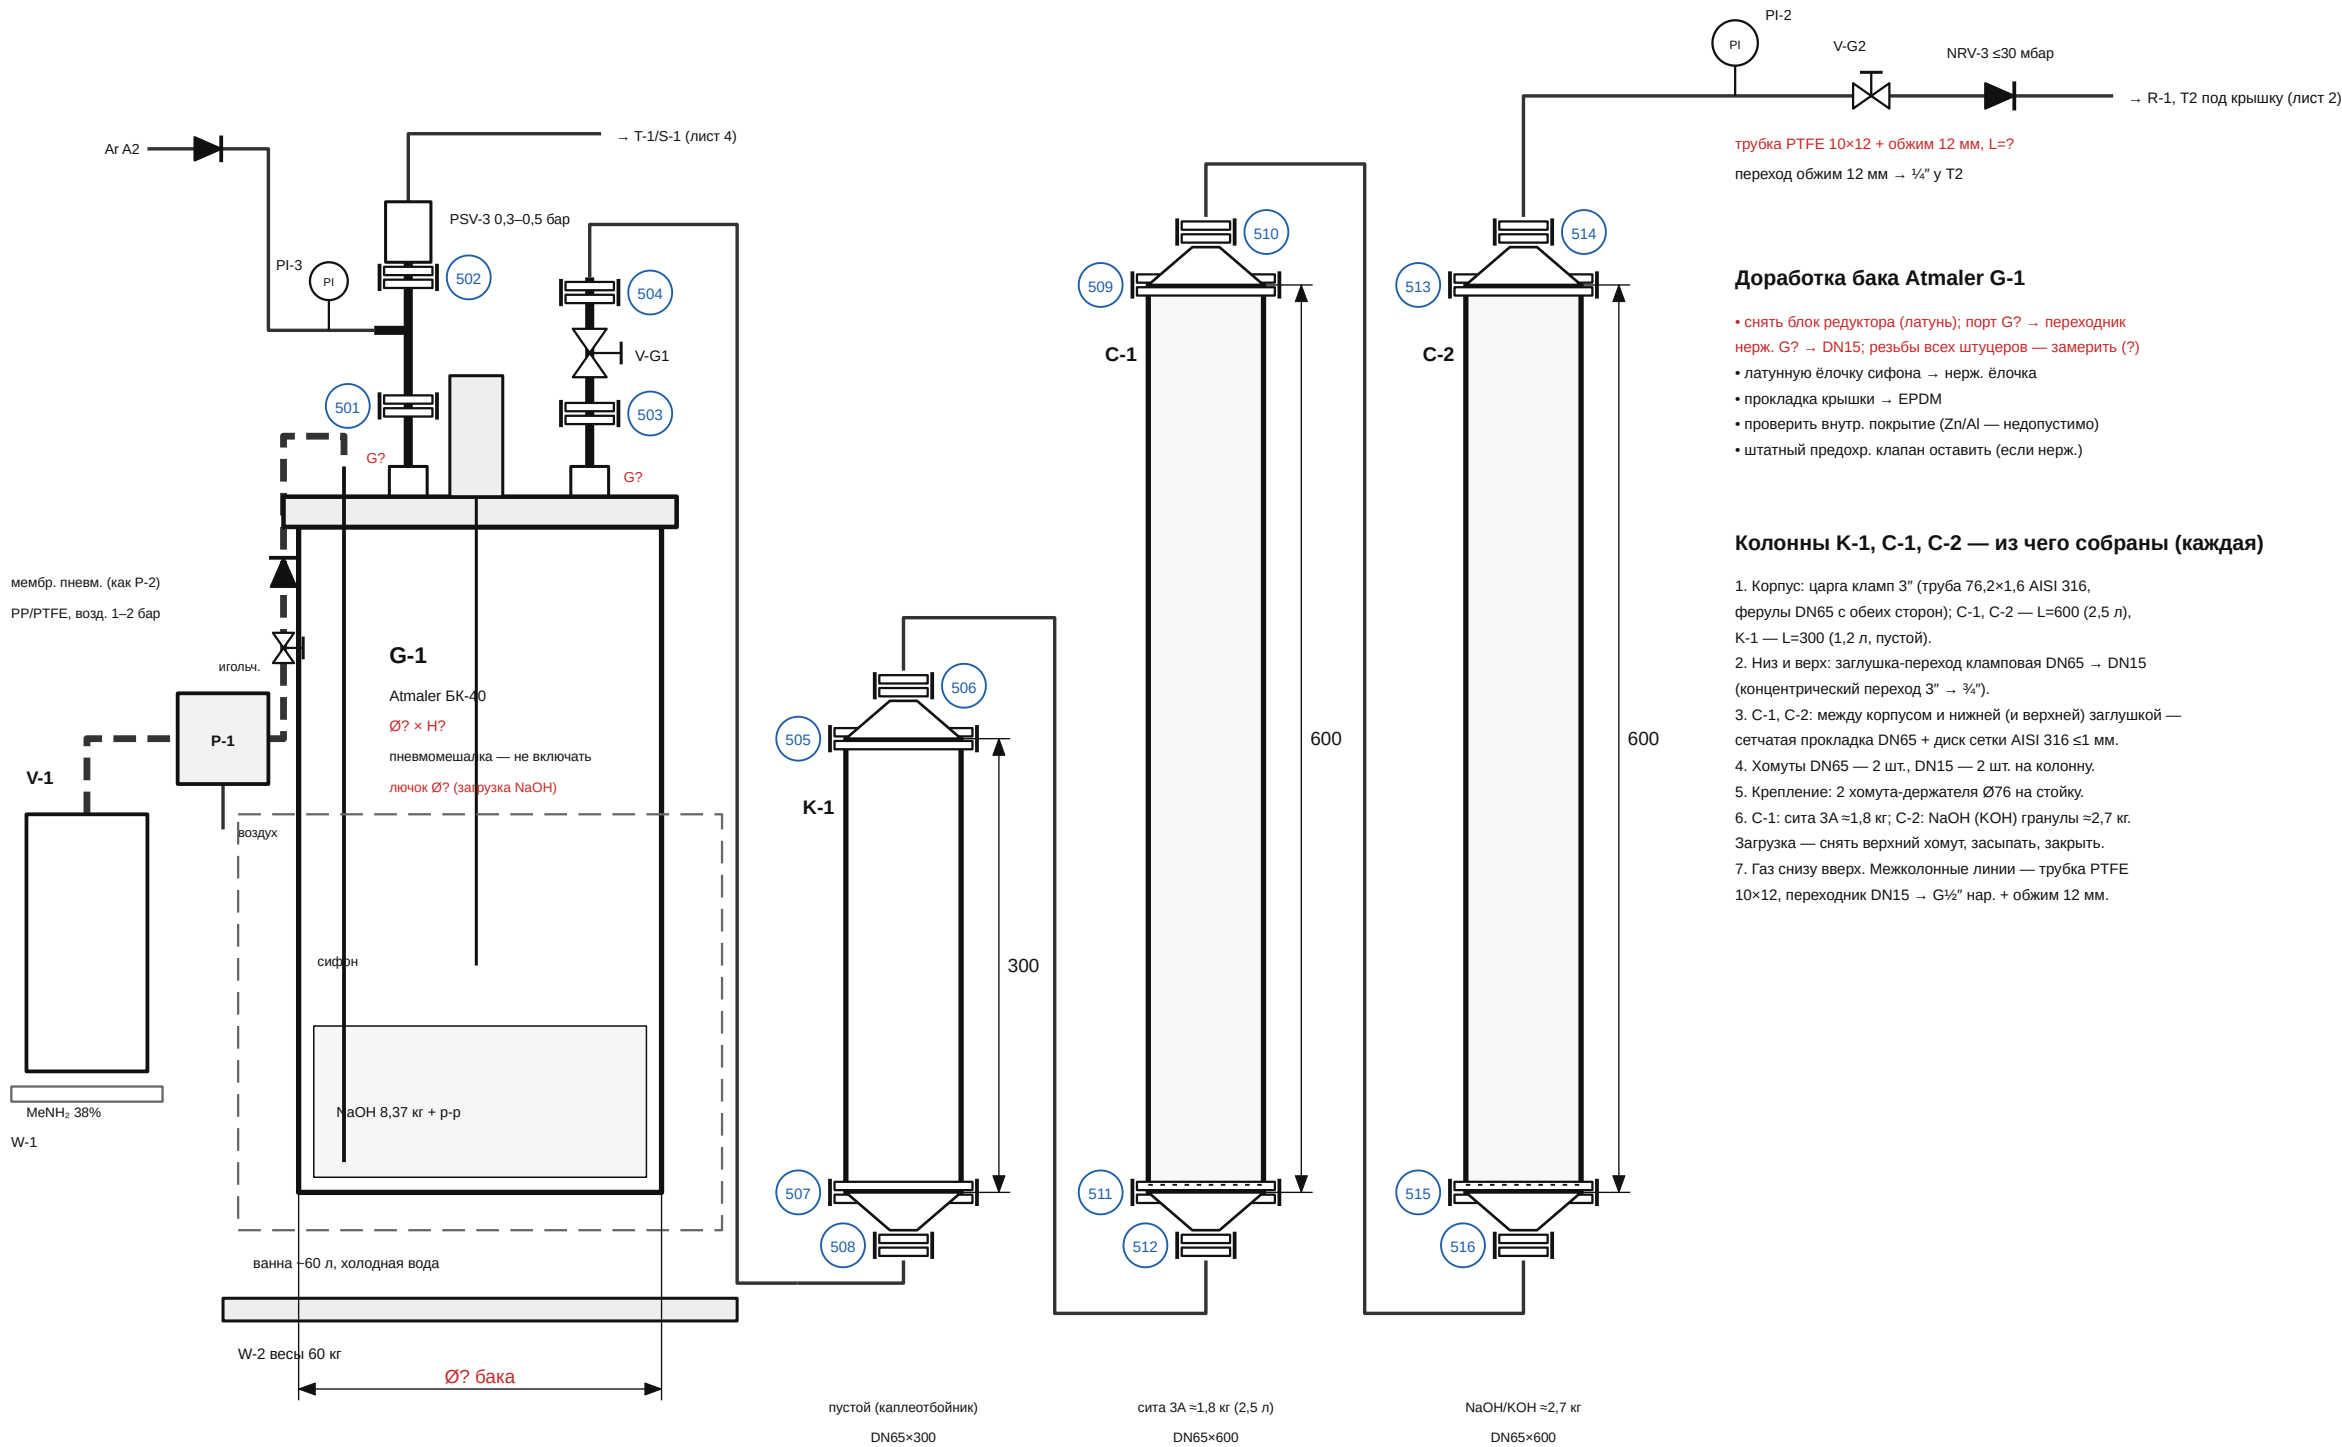

Доработка бака Atmaler G-1

- снять блок редуктора (латунь); порт G? → переходник нерж. G? → DN15; резьбы всех штуцеров — замерить (?)
- латунную ёлочку сифона → нерж. ёлочка
- прокладка крышки → EPDM
- проверить внутр. покрытие (Zn/Al — недопустимо)
- штатный предохранительный клапан оставить (если нерж.)

Колонны К-1, С-1, С-2 — из чего собраны (каждая)

1. Корпус: цага кламп 3" (труба 76,2×1,6 AISI 316, ферулы DN65 с обеих сторон); С-1, С-2 — L=600 (2,5 л), К-1 — L=300 (1,2 л, пустой).
2. Низ и верх: заглушка-переход кламповая DN65 → DN15 (концентрический переход 3" → ¼").
3. С-1, С-2: между корпусом и нижней (и верхней) заглушкой — сетчатая прокладка DN65 + диск сетки AISI 316 ≤1 мм.
4. Хомуты DN65 — 2 шт., DN15 — 2 шт. на колонну.
5. Крепление: 2 хомута-держателя Ø76 на стойку.
6. С-1: сита 3А ≈1,8 кг; С-2: NaOH (КОН) гранулы ≈2,7 кг. Загрузка — снять верхний хомут, засыпать, закрыть.
7. Газ снизу вверх. Межколонные линии — трубка PTFE 10×12, переходник DN15 → G½" нар. + обжим 12 мм.

ИНУМ.770-50.00.05


Генератор метиламина G-1, осушка
К-1, С-1, С-2

Лит. Масса Масштаб
П — б/м

Лист 5 Листов 8


АО «ИНУМИТ»

АРГОН: баллон → редуктор → раздаточный коллектор 1/4", б/м

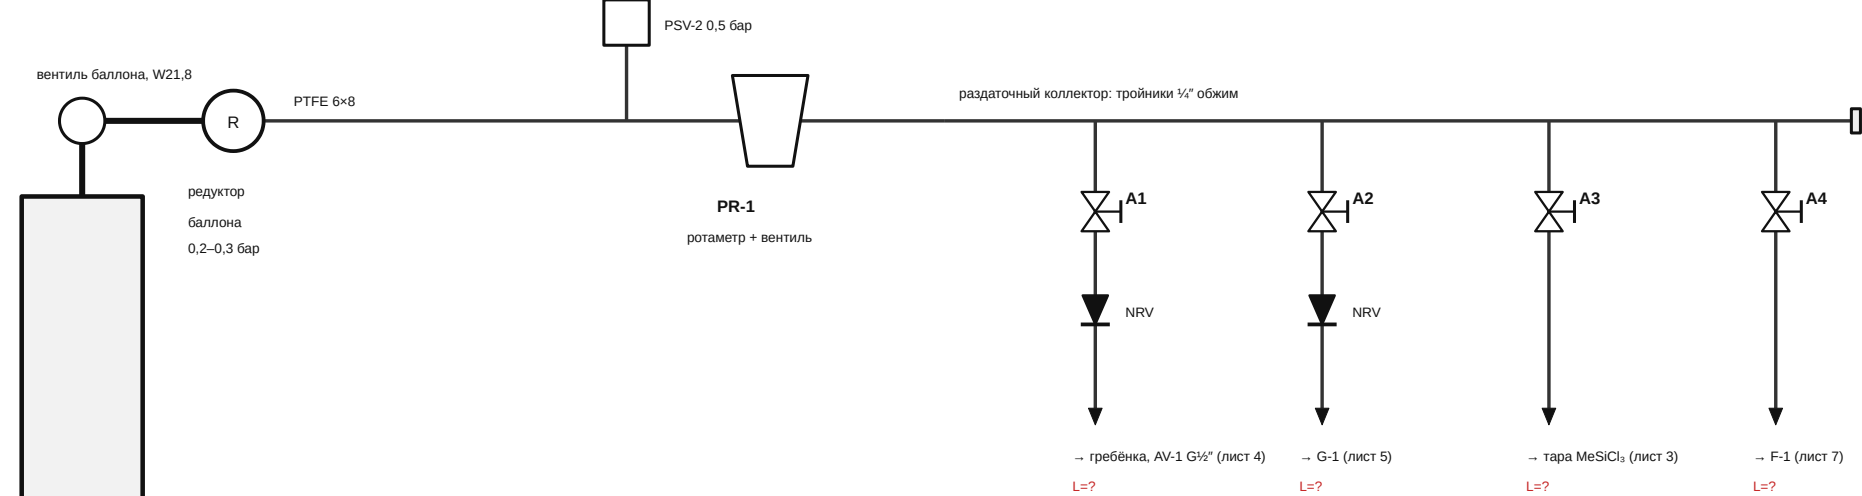

AR-1 Ar 99,998 %


ВАКУУМ

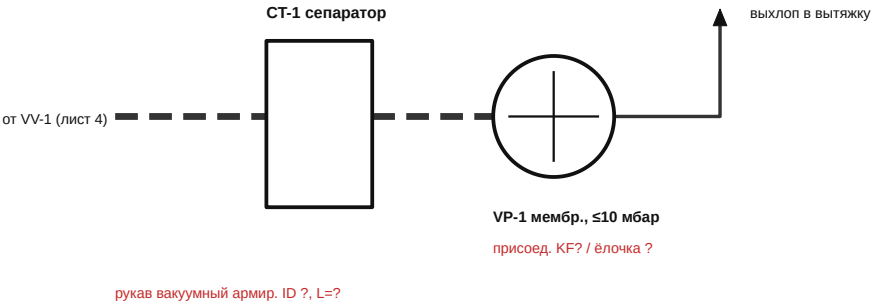

Примечания

- 1. Аргонные линии — трубка PTFE 6×8 или нерж. 1/4", обжимные фитинги.
- 2. Обратные клапаны на A1 и A2 — обязательно.
- 3. PR-1 (ротаметр с вентилем): синтез 0,1–0,2 л/мин, продувки 3–5, выгрузка ~10.
- 4. Резьбы редукторов/ротаметра — ?
- 5. Вакуум только на пустые сухие аппараты; выхлоп VP-1 — в вытяжку.

ТЕПЛОНОСИТЕЛЬ: ТС-1 → рубашка R-1 || E-1; стадия 7: E-1 на IW-1, б/м

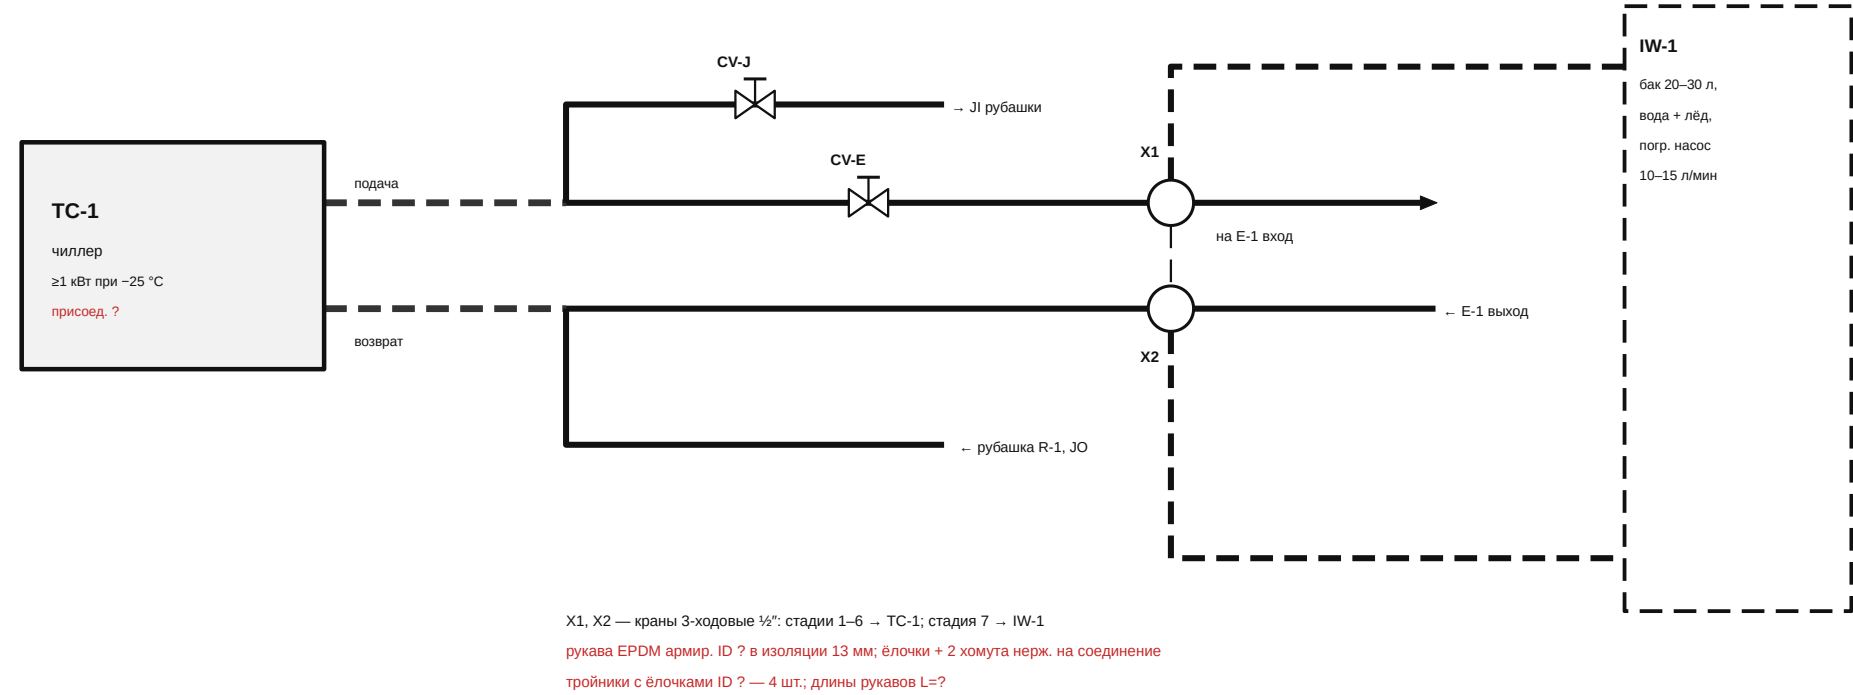


X1, X2 — краны 3-ходовые 1/2": стадии 1–6 → ТС-1; стадия 7 → IW-1
рукава EPDM армир. ID ? в изоляции 13 мм; ёлочки + 2 хомута нерж. на соединение
тройники с ёлочками ID ? — 4 шт.; длины рукавов L=?

					ИНУМ.770-50.00.06			
Изм.	Лист	№ докум.	Подп.	Дата				
Разраб.					Линии аргона, вакуума, теплоносителя	Лит.	Масса	Масштаб
Пров.						П	—	б/м
Т.контр.								
Н.контр.						Лист 6	Листов 8	
Утв.					ТЕФКОТ 770 · реактор 50 л	АО «ИНУМИТ»		

Примечания

- 1. Рукава продукта — PTFE ¾" антистат. в нерж. оплётке, заводские клампы.
- 2. Присоединение P-2 (G?) и F-1 — уточнить.
- 3. Скорость в трубках ≤1 м/с.
- 4. Все прокладки — PTFE.

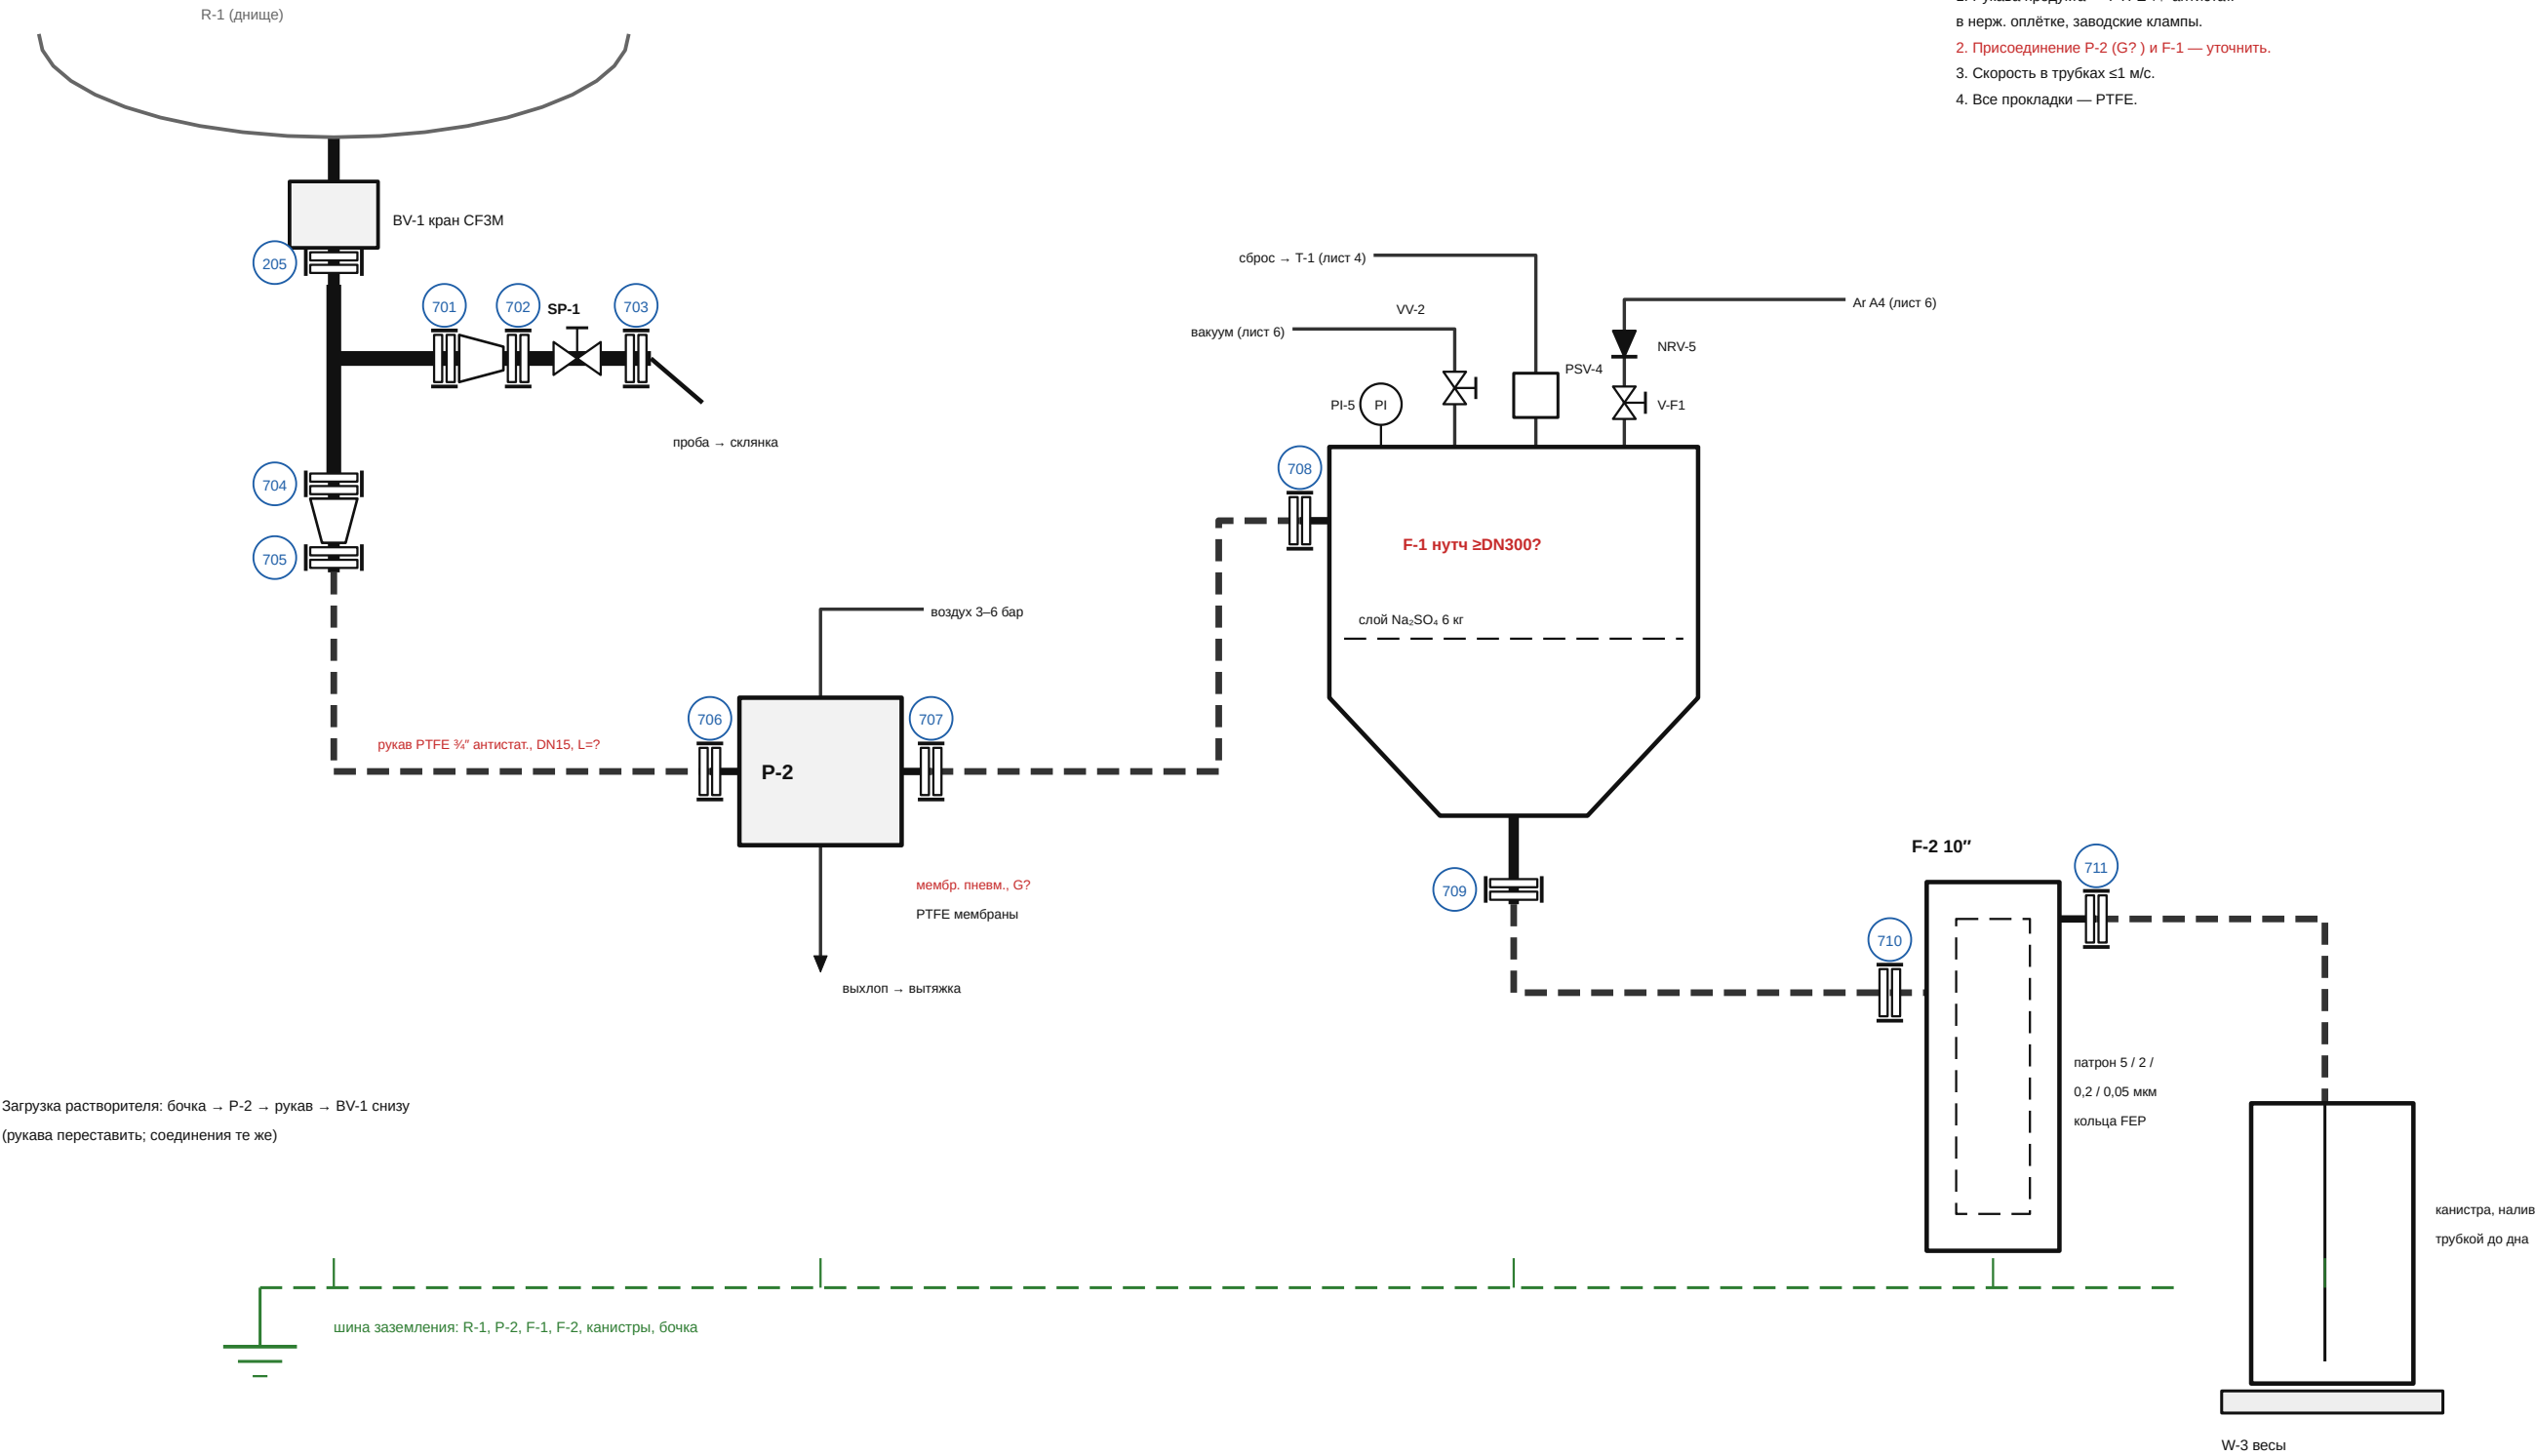

Загрузка растворителя: бочка → P-2 → рукав → BV-1 снизу
(рукава переставить; соединения те же)

					ИНУМ.770-50.00.07			
Изм.	Лист	№ докум.	Подп.	Дата				
Разраб.					Выгрузка, фильтрация, фасовка	Лит.	Масса	Масштаб
Пров.						П	—	б/м
Т.контр.								
Н.контр.						Лист 7		
Утв.					ТЕФКОТ 770 · реактор 50 л	АО «ИНУМИТ»		

ВЕДОМОСТЬ КЛАМПОВЫХ СОЕДИНЕНИЙ (номера — в кружках на листах 1–7)

№	Л.	Место	Размер	Прокл.
201	2	P4 — кран (сущ.) → PTFE-переходник с заглушкой	DN25 (P4, N1)	PTFE
202	2	P2 — заглушка с термогильзой	DN25 (P2, N4)	PTFE
203	2	P1 — конденсатор E-1	DN25 (P1, N3)	PTFE
204	2	P3 — узел дозирования (лист 3)	DN25 (P3, N5)	PTFE
205	2	BV-1 → тройник DN38 (лист 7)	DN38 (L)	PTFE
301	3	E-1 верх — заглушка змеевика	DN65 (3")	PTFE
302	3	E-1 отвод газа → переходник на ёлочку	DN15	PTFE
303	3	переход → кран V-P3	DN15	PTFE
304	3	V-P3 → тройник DN15	DN15	PTFE
305	3	тройник → септовая заглушка	DN15	PTFE
306	3	тройник → заглушка с обжимом ¼"	DN15	PTFE
401	4	ёлочка входа → тройник PI-4	DN15	PTFE
402	4	тройник PI-4 → тройник AV-1	DN15	PTFE
403	4	тройник AV-1 → тройник SV-1	DN15	PTFE
404	4	тройник SV-1 → тройник SV-2	DN15	PTFE
405	4	тройник SV-2 → тройник SV-3	DN15	PTFE
406	4	тройник SV-3 → отвод 90° на VV-1	DN15	PTFE
407	4	тройник → манометр PI-4	DN15	PTFE
408	4	тройник → кран AV-1	DN15	PTFE
409	4	AV-1 → переходник кламп/G½"	DN15	PTFE
410	4	тройник → кран SV-1	DN15	PTFE
411	4	SV-1 → NRV-1	DN15	PTFE
412	4	NRV-1 → переход DN15/DN25	DN15	PTFE
413	4	переход → шлунт PCV-1	DN25	PTFE
414	4	тройник → кран SV-2	DN15	PTFE
415	4	SV-2 → PSV-1	DN15	PTFE
416	4	тройник → кран SV-3	DN15	PTFE
417	4	SV-3 → ёлочка (атмосфера)	DN15	PTFE
418	4	отвод → кран VV-1	DN15	PTFE
419	4	VV-1 → ёлочка вакуумная	DN15	PTFE
501	5	G-1 порт регулятора (переходник G? → DN15) → тройник	DN15	EPDM
502	5	тройник → PSV-3	DN15	EPDM
503	5	G-1 выход газа (переходник G? → DN15) → V-G1	DN15	EPDM
504	5	V-G1 → ёлочка / трубка на K-1	DN15	EPDM
505	5	K-1 верх — заглушка-переход DN65/DN15	DN65	EPDM
506	5	K-1 верхний выход DN15	DN15	PTFE
507	5	K-1 низ — заглушка-переход DN65/DN15	DN65	EPDM
508	5	K-1 нижний вход DN15	DN15	PTFE
509	5	C-1 верх — заглушка-переход DN65/DN15	DN65	PTFE
510	5	C-1 верхний выход DN15	DN15	PTFE
511	5	C-1 низ — заглушка-переход DN65/DN15 + сетч. прокладка	DN65	PTFE
512	5	C-1 нижний вход DN15	DN15	PTFE
513	5	C-2 верх — заглушка-переход DN65/DN15	DN65	PTFE
514	5	C-2 верхний выход DN15	DN15	PTFE

№	Л.	Место	Размер	Прокл.
515	5	C-2 низ — заглушка-переход DN65/DN15 + сетч. прокладка	DN65	PTFE
516	5	C-2 нижний вход DN15	DN15	PTFE
701	7	тройник → переход DN38/DN15 (проба)	DN38	PTFE
702	7	переход → кран SP-1	DN15	PTFE
703	7	SP-1 → носик пробоотборника	DN15	PTFE
704	7	тройник → переход DN38/DN15 (выгрузка)	DN38	PTFE
705	7	переход → рукав PTFE (выгрузка)	DN15	PTFE
706	7	рукав → переходник DN15/резьба ? на P-2 (вход)	DN15	PTFE
707	7	P-2 выход (переходник резьба ?/DN15) → рукав	DN15	PTFE
708	7	рукав → вход нутча F-1	DN15?	PTFE
709	7	выход нутча → рукав на F-2	DN?	PTFE
710	7	рукав → вход F-2	DN15?	PTFE
711	7	выход F-2 → рукав на налив	DN15?	PTFE

СВОДКА: заказ = по схеме + 2 шт. каждого размера

Размер	Соед.	Хомутов	PTFE	EPDM	Примечание
DN15	41	43	39	6	
DN25	7	9	7	4	рубашка N7/N8: +2 EPDM
DN38	3	5	5	—	
DN65	7	9	7	4	
DN?	1	3	3	—	

Хомуты и прокладки — по схеме + 2 шт.; DN25 и DN38 — одна ферула 50,5.

					ИНУМ.770-50.00.08			
Изм.	Лист	№ докум.	Подп.	Дата				
Разраб.					Ведомость кламповых соединений	Лит.	Масса	Масштаб
Пров.						П	—	б/м
Т.контр.								
Н.контр.						Лист 8		Листов 8
Утв.					ТЕФКОТ 770 · реактор 50 л	АО «ИНУМИТ»		