

ВАКУУМНАЯ СТАНЦИЯ (УЗЕЛ 7) — СХЕМА ТЕХНОЛОГИЧЕСКАЯ: ресиверы V-805, V-806, агрегаты P-801…P-804

СИСТЕМА 1 — КВ-1 (327): R-101, R-201, R-301 → V-805 → P-801, P-802

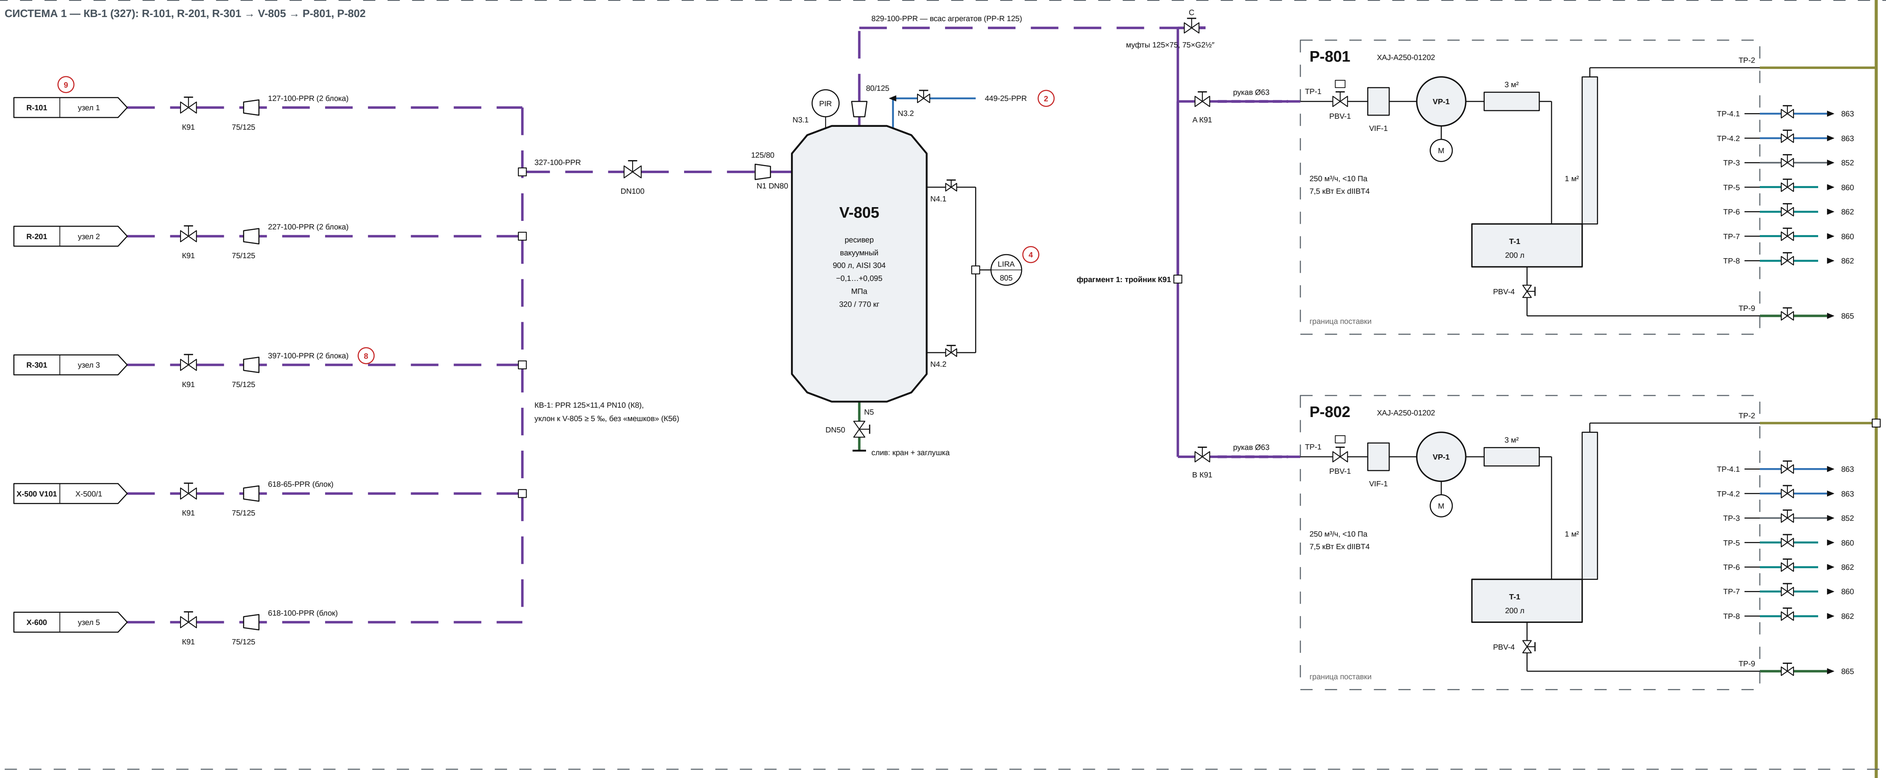

СИСТЕМА 2 — КВ-2 (333) и X-600 (618) → V-806 → P-803, P-804

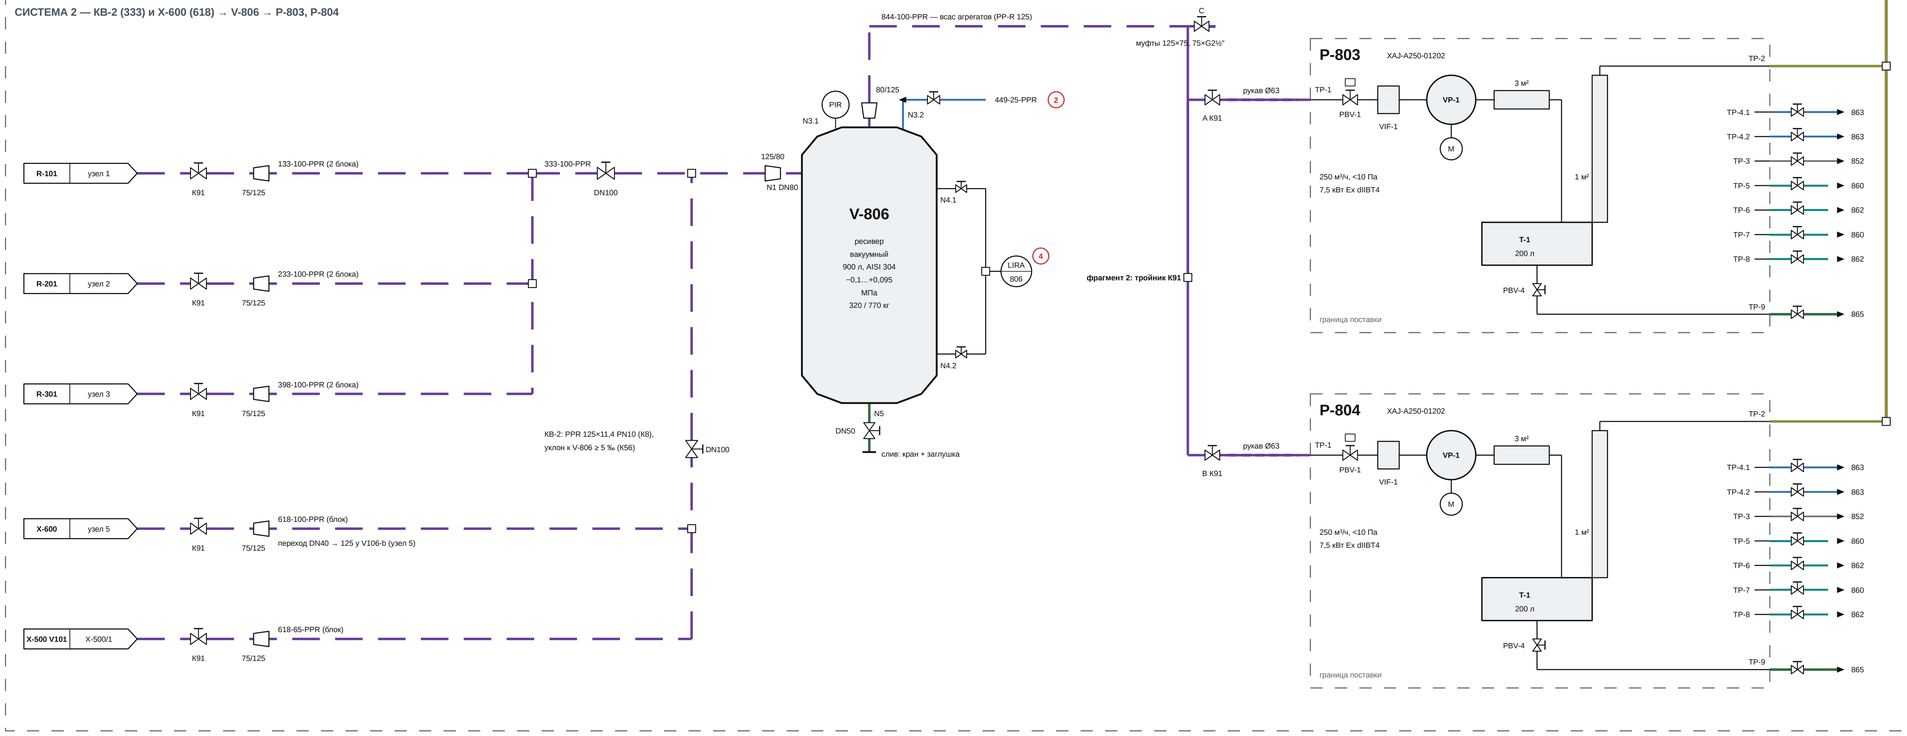

ПОДКЛЮЧЕНИЯ КАЖДОГО АГРЕГАТА

ТР	Среда	DN	Линия
1	вакуум, вход	50 RF	829 / 844
2	выхлоп	50 RF	861
4.1	N_2 продувка	10 мм	863
4.2	N_2 уплотн. 0,5–1 бар	8 мм	863
3	CDA 5–8 бар	G¼"	852
5 / 6	вода насоса	G½"	860 / 862
7 / 8	вода конденсаторов	25 RF	860 / 862
9	слив конденсата	25 RF	865

Вода 0,6 т/ч на агрегат, 2–32 °C, ΔP > 2 бар

860 / 862 — от магистрали PP 160×21,9 (K61) (7)

Расход N_2 и CDA — запросить у поставщика (6)

863, 852, 449 — узел 9 (азот и воздух)

865, 866, 867 — в сборник конденсата (1)

УСЛОВНЫЕ ОБОЗНАЧЕНИЯ

- вакуум (327, 333, 618, 829, 844)
- выхлоп агрегатов (861)
- азот (863, 449)
- вода оборотная (860, 862)
- сжатый воздух КИП (852)
- слив конденсата (865–867)
- граница поставки / зона
- кран шаровой
- клапан обратный (K15)
- кран с пневмоприводом (поставка XAJ)
- переход концентрический
- тройник
- PIR — прибор (КИП — раздел kipia)
- поз. узел — стык с другим узлом
- (1) — открытый вопрос (README, voprosy.md)

Номер линии: номер-DN-материал. PPR 125×11,4 = DN100.

Номера ТХ 37-02/26-ТХ 14.07 сохранены;

новые номера 397, 398, 865, 866, 867 — согласовать. (8)

K8, K15, K56, K61 — решения заказчика.

ПРИМЕЧАНИЯ

1. Вакуум — PPR 125×11,4 PN10 (K8); у агрегатов — блок отсечения (11.11, комплект «Вакуум_цех»): краны и тройник K91, рукава Ø63, муфты 75×G2½" и 125×75.
2. Ресиверы — нижняя точка (K56). 12.11: магистрали PP-R 125 — под площадкой П1 +5.420; на выходе N1 каждого ресивера — тройник: к реакторам и к X-500 (V101) → X-600.
3. У каждого потребителя (E-x02 N10, X-x03 N4) — свой объединяющий блок ≤ 1,5 м от входа: краны 1/2 K91, тройник, перемычка «U» Ø63, кран 4, фильтр 1", рукав 1".
4. От магистралей к блокам — отводы PP-R 75 (подвесы к низу площадки). Агрегаты — фрагменты на стойках 500 мм у пола, рукава Ø63 к насосам и к муфтам G2½".
5. Выхлоп ТР-2 — без арматуры (противодавление агрегата ≤ 30 кПа изб.). Отключение агрегата — заглушкой.
6. Внутри пунктира — поставка XAJ: PBV-1, VIF-1, VP-1, конденсаторы, T-1 200 л ниже насоса, PBV-4, КИП.
7. Агрегаты — компрессорная +4.000; ресиверы — площадка П1 +2.500 у оси 3 (04.11, Мареев: этажом ниже, ниже агрегатов; см. razmeshchenie.md).

Изм.	Лист.	№ докум.	Подп.	Дата	37-02/26-ТХ.ОБ7
Разраб.					Вакуумная станция (узел 7). Схема технологическая
Пров.					
Т.контр.					
Н.контр.					
Утв.					

Лит.	Масса	Масштаб
Р	—	б/м

Лист 1 — Листов 1

Обвязка, узел 7: вакуумная станция

Опытно-промышленный участок